
 
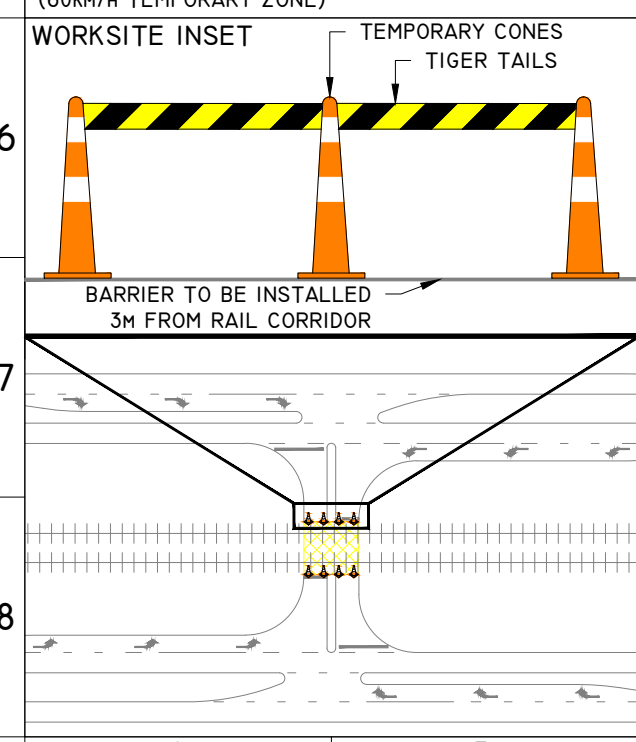


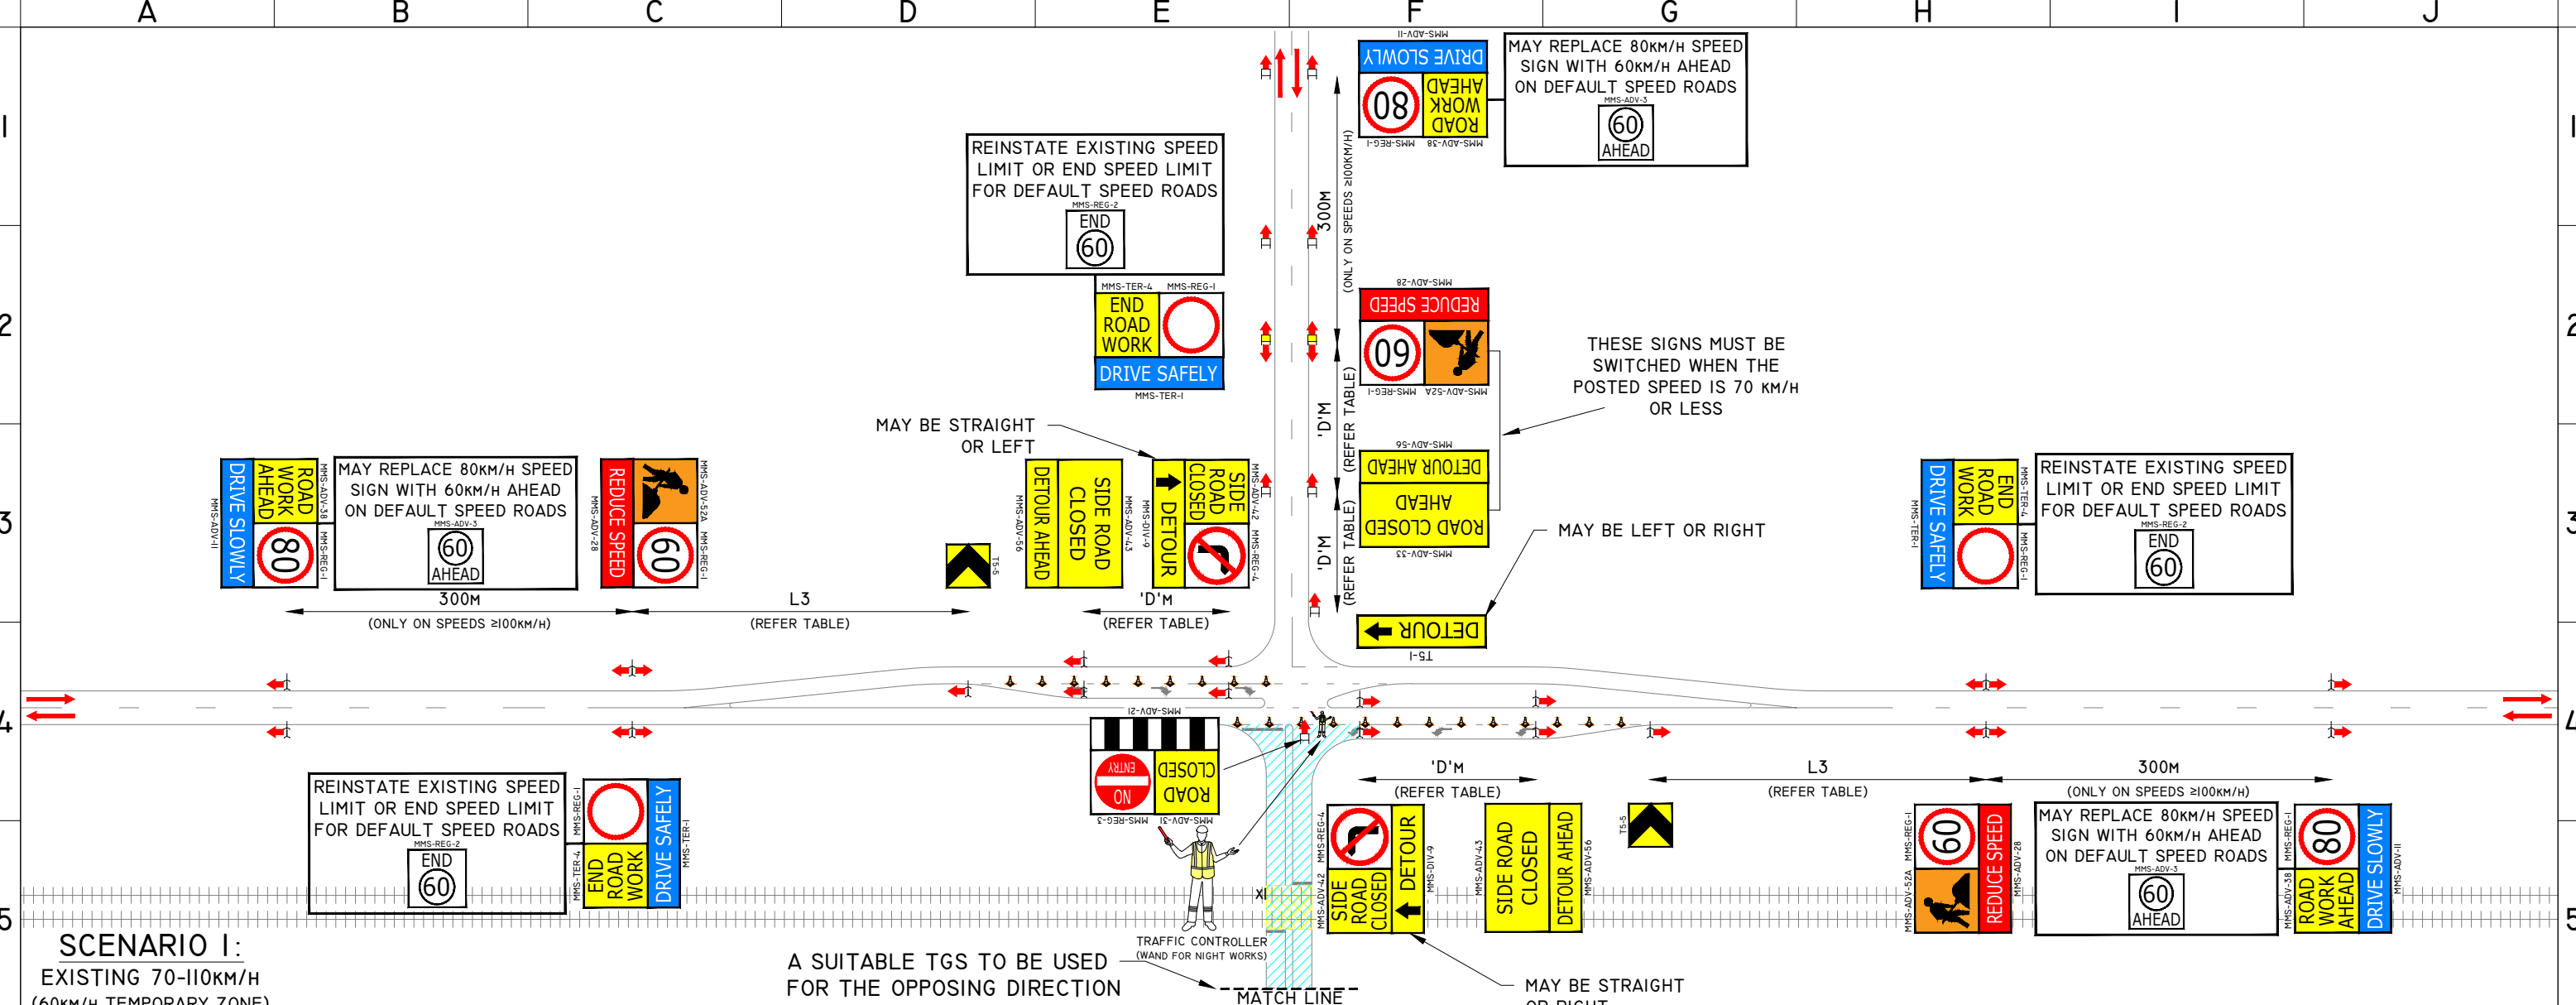

SIGN SPACING	
AGTTM PART 3 - TABLE 2.2	
SPEED LIMIT (KM/H)	DISTANCE ('D') (M)
55 OR LESS	15
56 TO 65	45
GREATER THAN 65	EQUAL TO SPEED OF TRAFFIC IN KM/H
MAIN ROADS WA CoP SECTION 6.5.2 - TABLE 6	
SPEED LIMIT (KM/H)	L3 (M)
70	70
80	160
90	180
100 & 110	160

RECOMMENDED CONE SPACING	
AGTTM PART 3 - TABLE 5.3	
ALL PURPOSES: (60 - 70km/h): 12M PROTECTING FRESHLY PAINTED LINES: (≤ 70km/h): 24M	
RECOMMENDED LANE WIDTHS	
MAIN ROADS WA CoP SECTION 6.7 - TABLE 9	
RECOMMENDED LANE WIDTHS: ≤ 60km/h: 3.2M MINIMUM LANE WIDTHS: ≤ 60km/h: 3.0M	

- NOTES**
- TOLERANCES**
POSITION OF SIGNS:
MINIMUM 10% LESS THAN THE DISTANCE OR LENGTHS GIVEN.
MAXIMUM 25% MORE THAN THE DISTANCES OR LENGTHS GIVEN.
SPACING OF DELINEATING DEVICES:
MAXIMUM 10% MORE THAN THE SPACING GIVEN.
NO MINIMUM.
AGTTM PART 6 SECTION 6.8.
- DOCUMENTATION**
ON-SITE VARIATIONS MUST BE APPROVED BY THE TRAFFIC MANAGEMENT SUPERVISOR, THAN AN ON-SITE VARIATION MADE AND CHANGES RECORDED IN THE DAILY DAIRY. FOR MORE INFORMATION REFER TO SECTION 9.3 OF THE TMP.
- A RISK ASSESSMENT MUST BE CARRIED OUT TO DETERMINE THE REQUIREMENTS OF AFTERCARE.
 - ALL SIGN LOCATIONS ARE TO BE CHECKED ON SITE PRIOR TO SETOUT AND POSITIONS ADJUSTED AS PER THE 'TOLERANCES'.
 - ALL CONTRADICTORY SIGNS WITHIN THE TM SETUP TO BE COVERED BY SUITABLY OPAQUE MATERIAL.
 - FOR BOX EDGED SIGN ALTERNATIVES, CONSULT AWTM PRIOR TO IMPLEMENTATION.
 - WORKERS TO REMAIN 10M CLEAR OF RAILWAY TRACKS AT ALL TIMES.
 - ACCREDITED FLAG PERSON TO MONITOR AND WARN OF INCOMING TRAINS OVER TWO-WAY RADIO. TCS WILL HOLD ALL TRAFFIC TO ALLOW TRAIN TO PASS.
 - REFER TO SECTION 4.1.8 OF THE TMP FOR THE MANDATORY USE OF SPEED FEEDBACK SIGNAGE
- PEDESTRIAN MANAGEMENT**
- 'PEDESTRIAN WATCH YOUR STEP' SIGN TO BE INSTALLED ON EACH APPROACH WHERE WORKS MAY ENCR OACH ONTO OR ADJACENT TO EXISTING FOOTPATH FACILITIES.
 - TM PERSONNEL TO MONITOR AND ESCORT PEDESTRIANS THROUGH THE WORK AREA AS REQUIRED.
 - PEDESTRIANS MAY BE HELD ON EITHER END OF THE WORKSITE UNTIL IT IS SAFE TO PASS AS REQUIRED.