


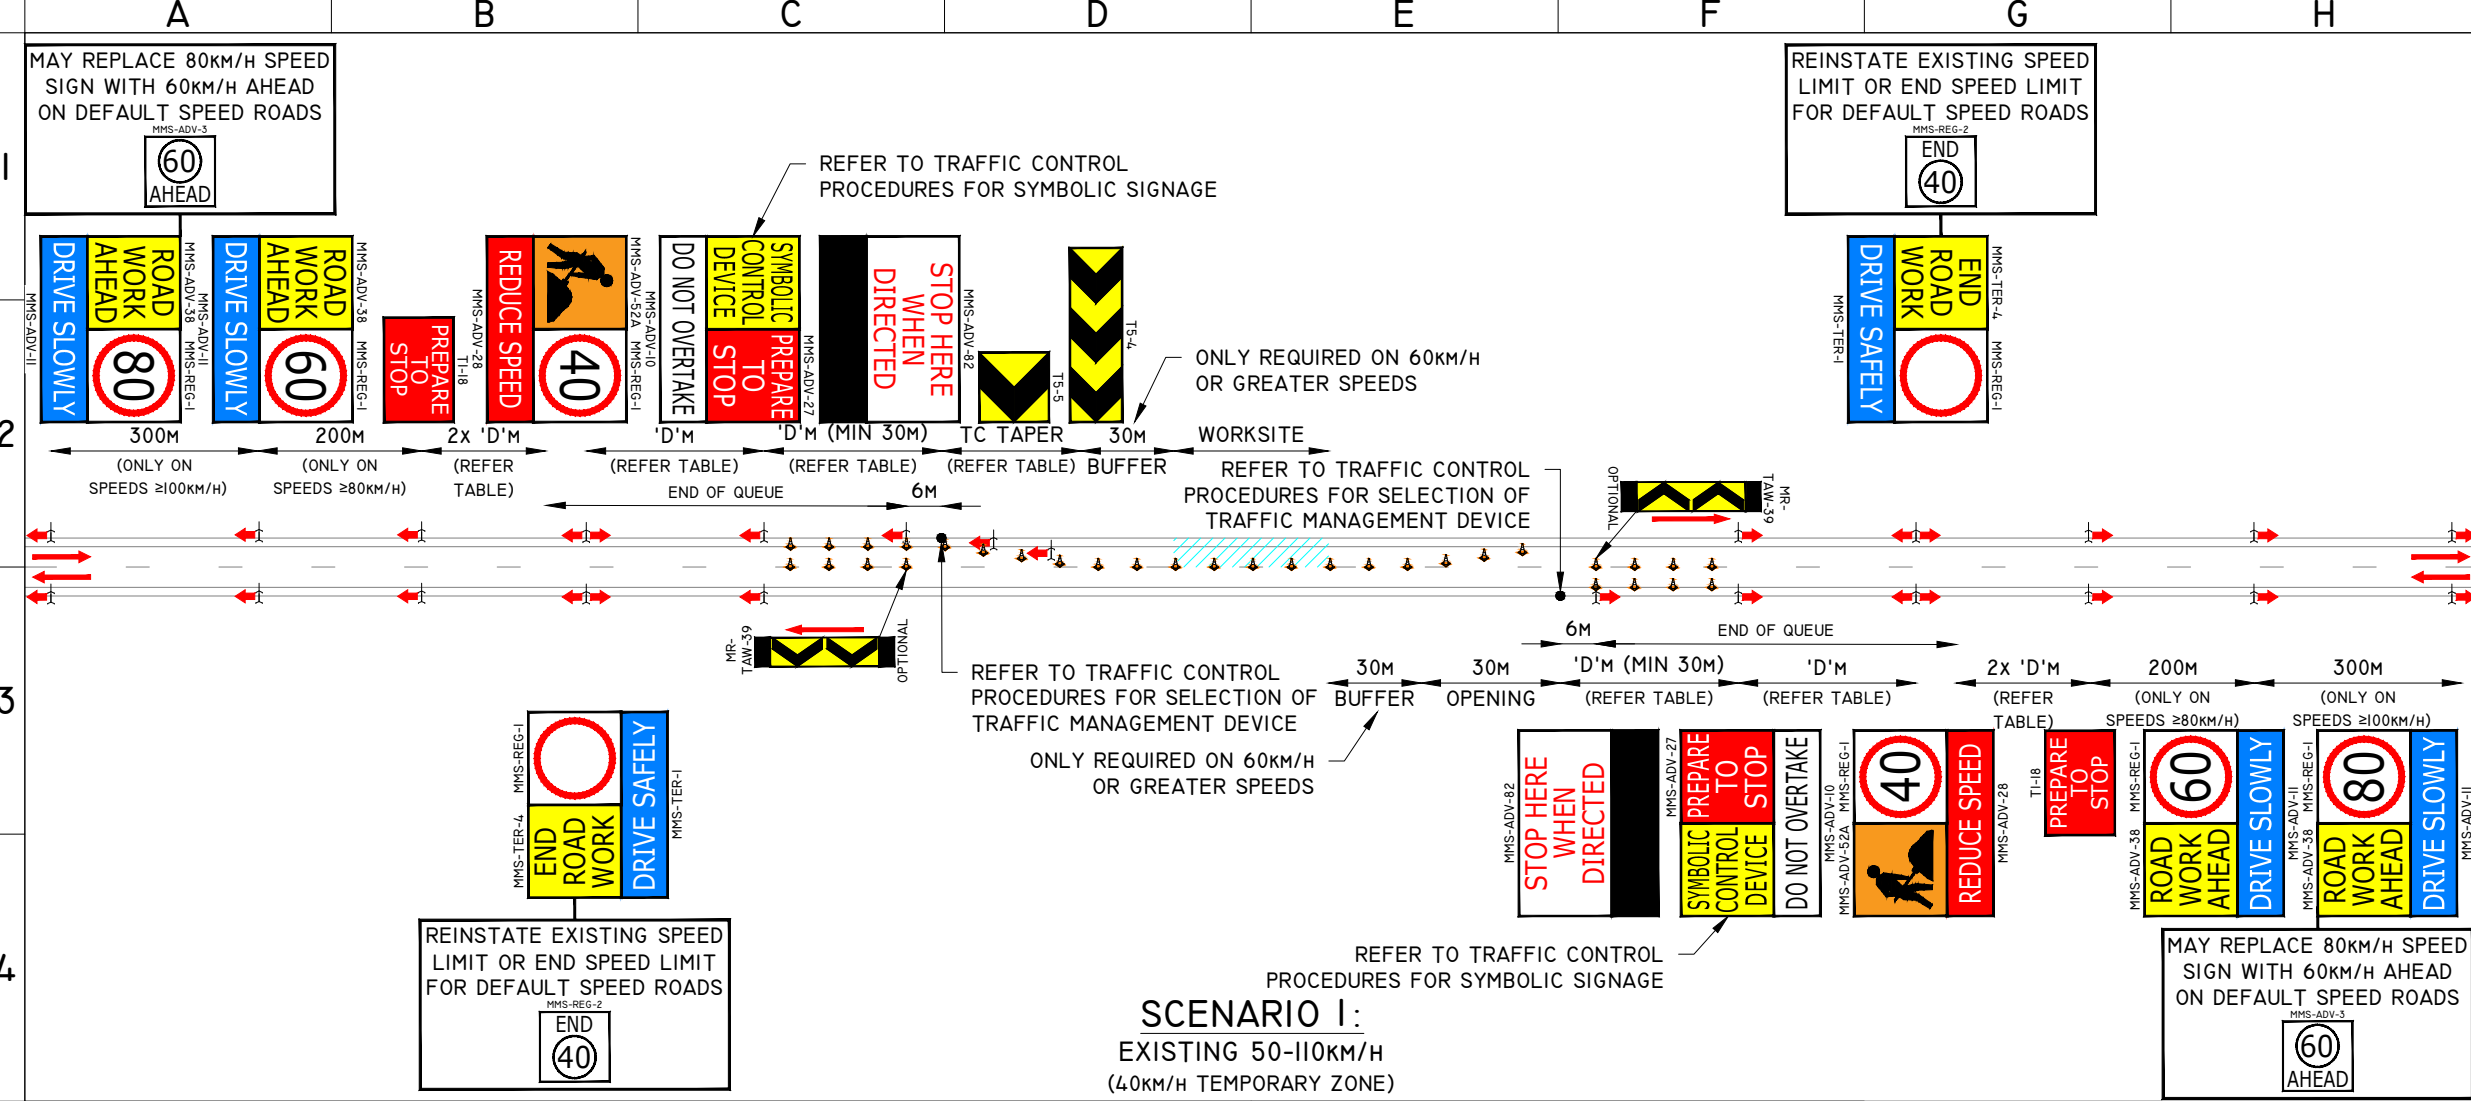

NOTES

TOLERANCES
POSITION OF SIGNS:
MINIMUM 10% LESS THAN THE DISTANCE OR LENGTHS GIVEN.
MAXIMUM 25% MORE THAN THE DISTANCES OR LENGTHS GIVEN.
SPACING OF DELINEATING DEVICES:
MAXIMUM 10% MORE THAN THE SPACING GIVEN.
NO MINIMUM.
AGTTM PART 6 SECTION 6.8.

DOCUMENTATION
ON-SITE VARIATIONS MUST BE APPROVED BY THE TRAFFIC MANAGEMENT SUPERVISOR, THAN AN ON-SITE VARIATION MADE AND CHANGES RECORDED IN THE DAILY DAIRY. FOR MORE INFORMATION REFER TO SECTION 9.3 OF THE TMP.

GENERAL NOTES

1. A RISK ASSESSMENT MUST BE CARRIED OUT TO DETERMINE THE REQUIREMENTS OF AFTERCARE.
2. ALL SIGN LOCATIONS ARE TO BE CHECKED ON SITE PRIOR TO SETOUT AND POSITIONS ADJUSTED AS PER THE 'TOLERANCES'.
3. ALL CONTRADICTIONARY SIGNS TO BE COVERED BY SUITABLY OPAQUE MATERIAL.
4. FOR BOX EDGED SIGN ALTERNATIVES, CONSULT AWTM PRIOR TO IMPLEMENTATION.
5. MAXIMUM LENGTH OF 40km/h SPEED ZONE MUST BE 500M.
6. REFER TO SECTION 4.1.8 OF THE TMP FOR THE MANDATORY USE OF SPEED FEEDBACK SIGNAGE

PEDESTRIAN MANAGEMENT

1. 'PEDESTRIAN WATCH YOUR STEP' SIGN TO BE INSTALLED ON EACH APPROACH WHERE WORKS MAY ENCROACH ONTO OR ADJACENT TO EXISTING FOOTPATH FACILITIES.
2. TM PERSONNEL TO MONITOR AND ESCORT PEDESTRIANS THROUGH THE WORK AREA AS REQUIRED.
3. PEDESTRIANS MAY BE HELD ON EITHER END OF THE WORKSITE UNTIL IT IS SAFE TO PASS AS REQUIRED.

RECOMMENDED CONE SPACING
AGTTM PART 3 - TABLE 5.3
ALL PURPOSES:
(≤ 50km/h): 4m
PROTECTING FRESHLY PAINTED LINES:
(≤ 70km/h): 24m
CENTRELINE ON APPROACH TO TC POSITION: 4m
TAPER AT TRAFFIC CONTROL STATION: 4m

RECOMMENDED LANE WIDTHS
MAIN ROADS WA CoP SECTION 6.7 - TABLE 9
SHUTTLE FLOW WITH CONTROL: 3.2m

TRAFFIC CONTROL PROCEDURES
REFER TO TMP SECTION 4.1.7 PORTABLE TRAFFIC CONTROL DEVICES FOR MORE DETAILS

MANUAL TRAFFIC CONTROL

5. ACCREDITED TRAFFIC CONTROLLER (MMS-ADV-47, MMS-ADV-27, MMS-ADV-82, MMS-ADV-10)

6. PORTABLE TRAFFIC CONTROL DEVICE (PTCD) (MMS-ADV-79, MMS-ADV-27, MMS-ADV-82, MMS-ADV-10)

7. PORTABOOM (MMS-ADV-79, MMS-ADV-27, MMS-ADV-82, MMS-ADV-10)

8. TEMPORARY TRAFFIC SIGNAL (MMS-ADV-48, MMS-ADV-27, R6-6, MMS-ADV-10)

SHADOW VEHICLE INSET
SHADOW VEHICLE MAY BE DISPENSED WITH UNDER A RISK ASSESSMENT BY AN RTM AS PART OF THE TM ADVISE. IN THE ABSENCE OF THE SHADOW VEHICLE A LOOKOUT PERSON IS REQUIRED. REFER TO SECTION 4.5 OF THE TMP FOR MORE DETAILS.

SHADOW VEHICLE
FLASHING ARROW
20-40M BUFFER
WORK SITE

FLASHING ARROWBOARD ON TMA
FLASHING ARROW
VARIABLE MESSAGE BOARD
DISPLAY 1
DISPLAY 2
TEMPORARY SPEED ZONE
REFER TO SECTION 4.5.1 OF THE TMP FOR TMA REQUIREMENTS

TABLES	
TAPER LENGTHS	
AGTTM PART 3 - TABLE 5.7	
SPEED LIMIT (KM/H)	TRAFFIC CONTROL TAPER (M)
45 OR LESS	15
46 TO 55	15
56 TO 65	30
66 TO 75*	N/A
76 TO 85*	
86 TO 95*	
96 TO 105*	
GREATER THAN 105*	
*TAPER LENGTHS ARE BASED ON A: • 3.5M WIDTH OF THE LANE TO BE CLOSED • LATERAL SHIFT TAPER LENGTH EQUAL TO 1.0M/s • MEDIAN SPEED FOR EACH RANGE (I.E 76 - 85 = 80KM/H)	
SIGN SPACING	
AGTTM PART 3 - TABLE 2.2	
SPEED LIMIT (KM/H)	DISTANCE ('D') (M)
55 OR LESS	15
56 TO 65	45
GREATER THAN 65	EQUAL TO SPEED OF TRAFFIC IN KM/H
MAXIMUM LENGTH OF SHUTTLE FLOW	
MAIN ROADS WA CoP SECTION 6.8.6 - TABLE 15	
VOLUMES (BOTH DIRECTION) (VPH)	LENGTH (BETWEEN Tcs) (M)
RESIDENTIAL STREET	60
701 - 800	70
601 - 700	100
501 - 600	150
401 - 500	250
351 - 400	400
301- 350	600
251 - 300	800
201 - 250	1200
151 - 200	1600
≤150	2200
G	H

LEGEND

- EXISTING ROAD
- PROPOSED CONES
- WORKSITE

mainroads WESTERN AUSTRALIA

METROPOLITAN REGIONS TRAFFIC MANAGEMENT BRANCH
WATERLOO CRESCENT
TELEPHONE (08) 138 138
EAST PERTH 6004

DATE OF DRAWING	2025 JULY	SCALE	-
LOCAL GOVERNMENT AUTHORITY	-	POSTED SPEED	50-110km/h
ROAD AUTHORITY	MAIN ROADS WA	WORKSITE SPEED	40km/h
CHECKED BY	TYLER HARTLEY	SIGNATURE	Tyler Hartley
ACCREDITATION	RTM-0066	SIGNATURE	Michael Reed
DESIGNED BY	MICHAEL REED	SIGNATURE	Michael Reed
ACCREDITATION	AWTM-23-11536-02	GENERIC TRAFFIC GUIDANCE SCHEME REVERSIBLE FLOW SETUPS SINGLE LANE ROAD WITH EoQ WORKSITE WITHIN 1.2M	
DRAWING NO	0922-01531-RF-002	REVISION	6