


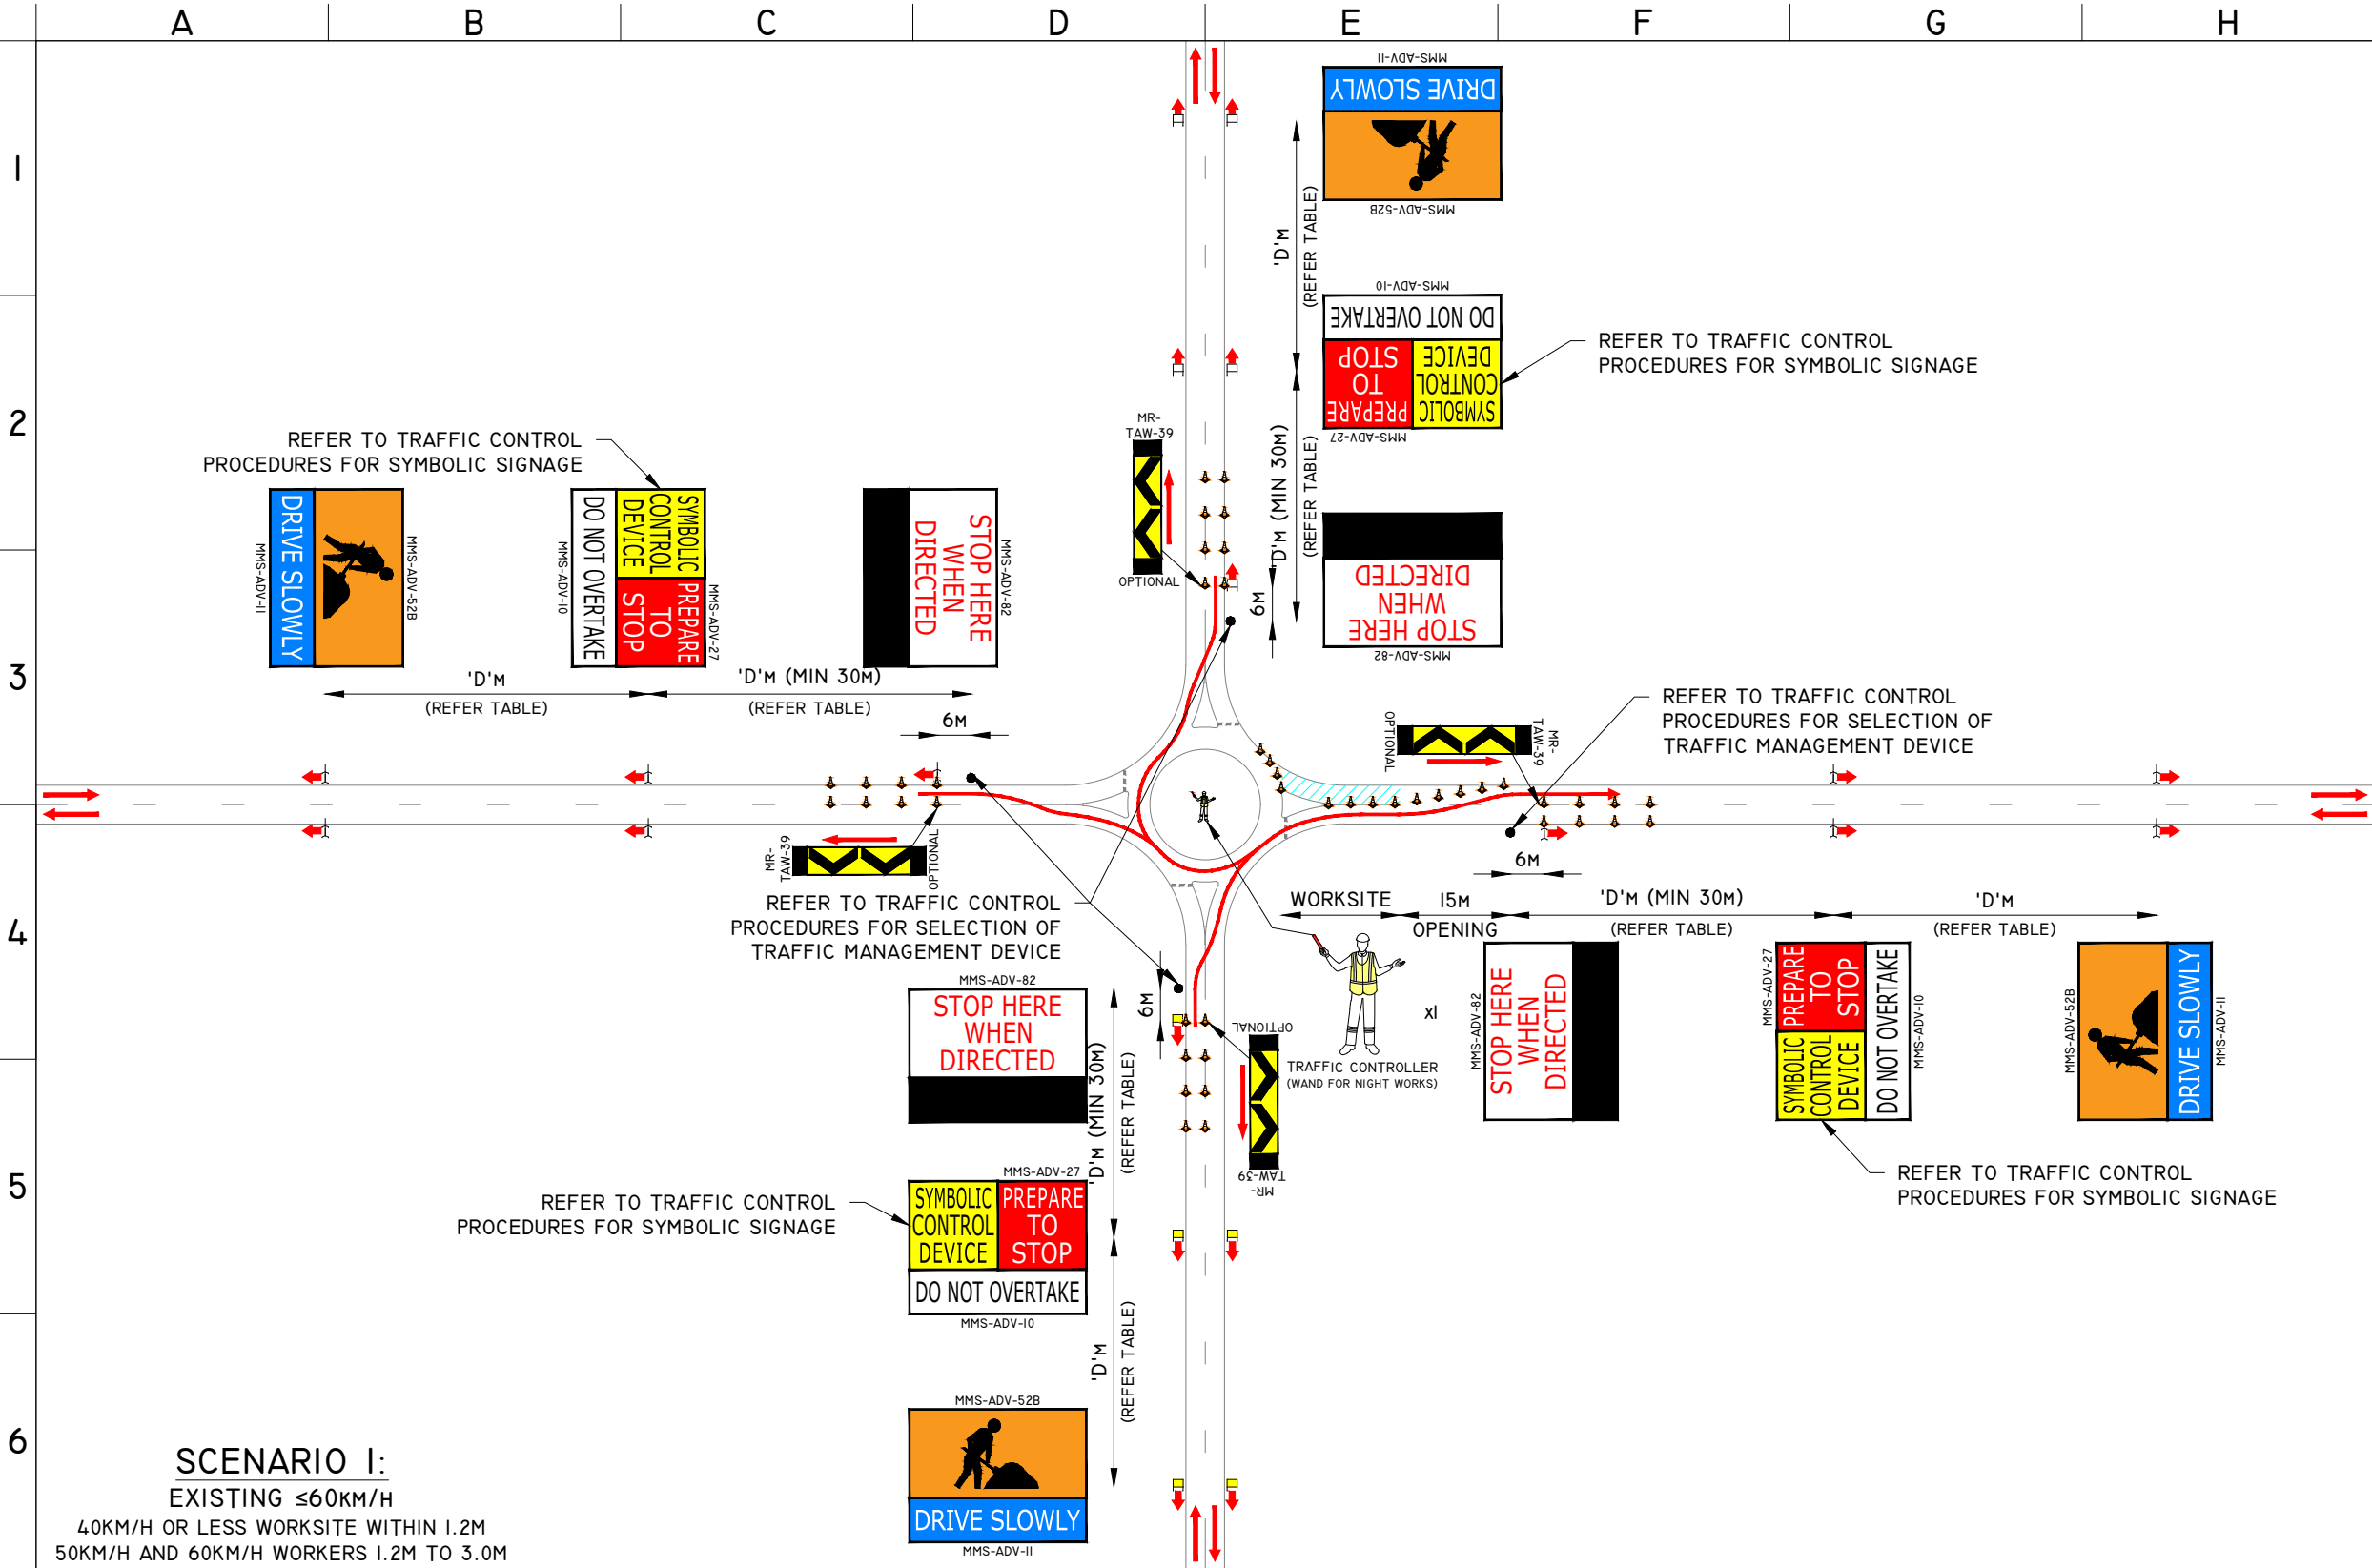

SCENARIO 1:
EXISTING ≤60KM/H
40KM/H OR LESS WORKSITE WITHIN 1.2M
50KM/H AND 60KM/H WORKERS 1.2M TO 3.0M

TRAFFIC CONTROL PROCEDURES

REFER TO TMP SECTION 4.1.7 PORTABLE TRAFFIC CONTROL DEVICES FOR MORE DETAILS

MANUAL TRAFFIC CONTROL

ACCREDITED TRAFFIC CONTROLLER

PORTABLE TRAFFIC CONTROL DEVICE (PTCD)

PORTABOOM

TEMPORARY TRAFFIC SIGNAL

MANUAL TRAFFIC CONTROL IS NOT PERMITTED ON THE MAIN ROADS NETWORK WITH THE EXCEPTIONS LISTED UNDER SECTION 4.1.7 (PORTABLE TRAFFIC CONTROL DEVICES) OF THE TMP AND IN THE MAIN ROADS CODE OF PRACTICE.

ON ALL OTHER ROADS, PTCds MUST BE USED UNDER THE FOLLOWING CONDITIONS:

- A PERMANENT SPEED LIMIT OF 90M/H OR MORE AND OVER 2,000VPD; OR
- A PERMANENT SPEED LIMIT OF 80KM/H OR MORE AND OVER 10,000VPD.

PTCDs SHOULD BE CONSIDERED ON ALL WORKS AND ONLY BE SUPPLEMENTED WITH MANUAL TRAFFIC CONTROL UNDER AN AWTM/WTM RISK ASSESSMENT.

TABLES

MAXIMUM LENGTH OF SHUTTLE FLOW MAIN ROADS WA CoP SECTION 6.8.6 - TABLE 15	
VOLUMES (BOTH DIRECTION) (VPH)	LENGTH (BETWEEN TCs) (M)
RESIDENTIAL STREET	60
701 - 800	70
601 - 700	100
501 - 600	150
401 - 500	250
351 - 400	400
301- 350	600
251 - 300	800
201 - 250	1200
151 - 200	1600
≤150	2200

SIGN SPACING AGTTM PART 3 - TABLE 2.2	
SPEED LIMIT (KM/H)	DISTANCE ('D') (M)
55 OR LESS	15
56 TO 65	45
GREATER THAN 65	EQUAL TO SPEED OF TRAFFIC IN KM/H

NOTES

- TOLERANCES**
POSITION OF SIGNS:
MINIMUM 10% LESS THAN THE DISTANCE OR LENGTHS GIVEN.
MAXIMUM 25% MORE THAN THE DISTANCES OR LENGTHS GIVEN.
SPACING OF DELINEATING DEVICES:
MAXIMUM 10% MORE THAN THE SPACING GIVEN.
NO MINIMUM.
AGTTM PART 6 SECTION 6.8.
- DOCUMENTATION**
ON-SITE VARIATIONS MUST BE APPROVED BY THE TRAFFIC MANAGEMENT SUPERVISOR, THAN AN ON-SITE VARIATION MADE AND CHANGES RECORDED IN THE DAILY DAIRY. FOR MORE INFORMATION REFER TO SECTION 9.3 OF THE TMP.
- GENERAL NOTES**
1. A RISK ASSESSMENT MUST BE CARRIED OUT TO DETERMINE THE REQUIREMENTS OF AFTERCARE.
 2. ALL SIGN LOCATIONS ARE TO BE CHECKED ON SITE PRIOR TO SETOUT AND POSITIONS ADJUSTED AS PER THE 'TOLERANCES'.
 3. ALL CONTRADICTORY SIGNS TO BE COVERED BY SUITABLY OPAQUE MATERIAL.
 4. FOR BOX EDGED SIGN ALTERNATIVES, CONSULT AWTM PRIOR TO IMPLEMENTATION.
- PEDESTRIAN MANAGEMENT**
1. 'PEDESTRIAN WATCH YOUR STEP' SIGN TO BE INSTALLED ON EACH APPROACH WHERE WORKS MAY ENCROACH ONTO OR ADJACENT TO EXISTING FOOTPATH FACILITIES.
 2. TM PERSONNEL TO MONITOR AND ESCORT PEDESTRIANS THROUGH THE WORK AREA AS REQUIRED.
 3. PEDESTRIANS MAY BE HELD ON EITHER END OF THE WORKSITE UNTIL IT IS SAFE TO PASS AS REQUIRED.
- RECOMMENDED CONE SPACING**
AGTTM PART 3 - TABLE 5.3
ALL PURPOSES:
(≤ 50KM/H): 4M
(60 - 70KM/H): 12M
PROTECTING FRESHLY PAINTED LINES:
(≤ 70KM/H): 24M
CENTRELINE ON APPROACH TO TC POSITION: 4M
TAPER AT TRAFFIC CONTROL STATION: 4M
- RECOMMENDED LANE WIDTHS**
MAIN ROADS WA CoP SECTION 6.7 - TABLE 9
SHUTTLE FLOW WITH CONTROL: 3.2M

LEGEND

- EXISTING ROAD
- PROPOSED CONES
- WORKSITE

mainroads
WESTERN AUSTRALIA

**METROPOLITAN REGIONS
TRAFFIC MANAGEMENT BRANCH**

WATERLOO CRESCENT
TELEPHONE (08) 138 138

EAST PERTH 6004

DATE OF DRAWING 2025 JULY	SCALE -
LOCAL GOVERNMENT AUTHORITY -	POSTED SPEED ≤60KM/H
ROAD AUTHORITY MAIN ROADS WA	WORKSITE SPEED AS POSTED
CHECKED BY TYLER HARTLEY	SIGNATURE
ACCREDITATION RTM-0066	SIGNATURE
DESIGNED BY MICHAEL REED	
ACCREDITATION AWTM-23-11536-02	
GENERIC TRAFFIC GUIDANCE SCHEME REVERSIBLE FLOW SETUPS THROUGH ROUNDABOUT AS POSTED SPEED ZONE	
DRAWING NO 0922-01531-RF-004	REVISION 6