


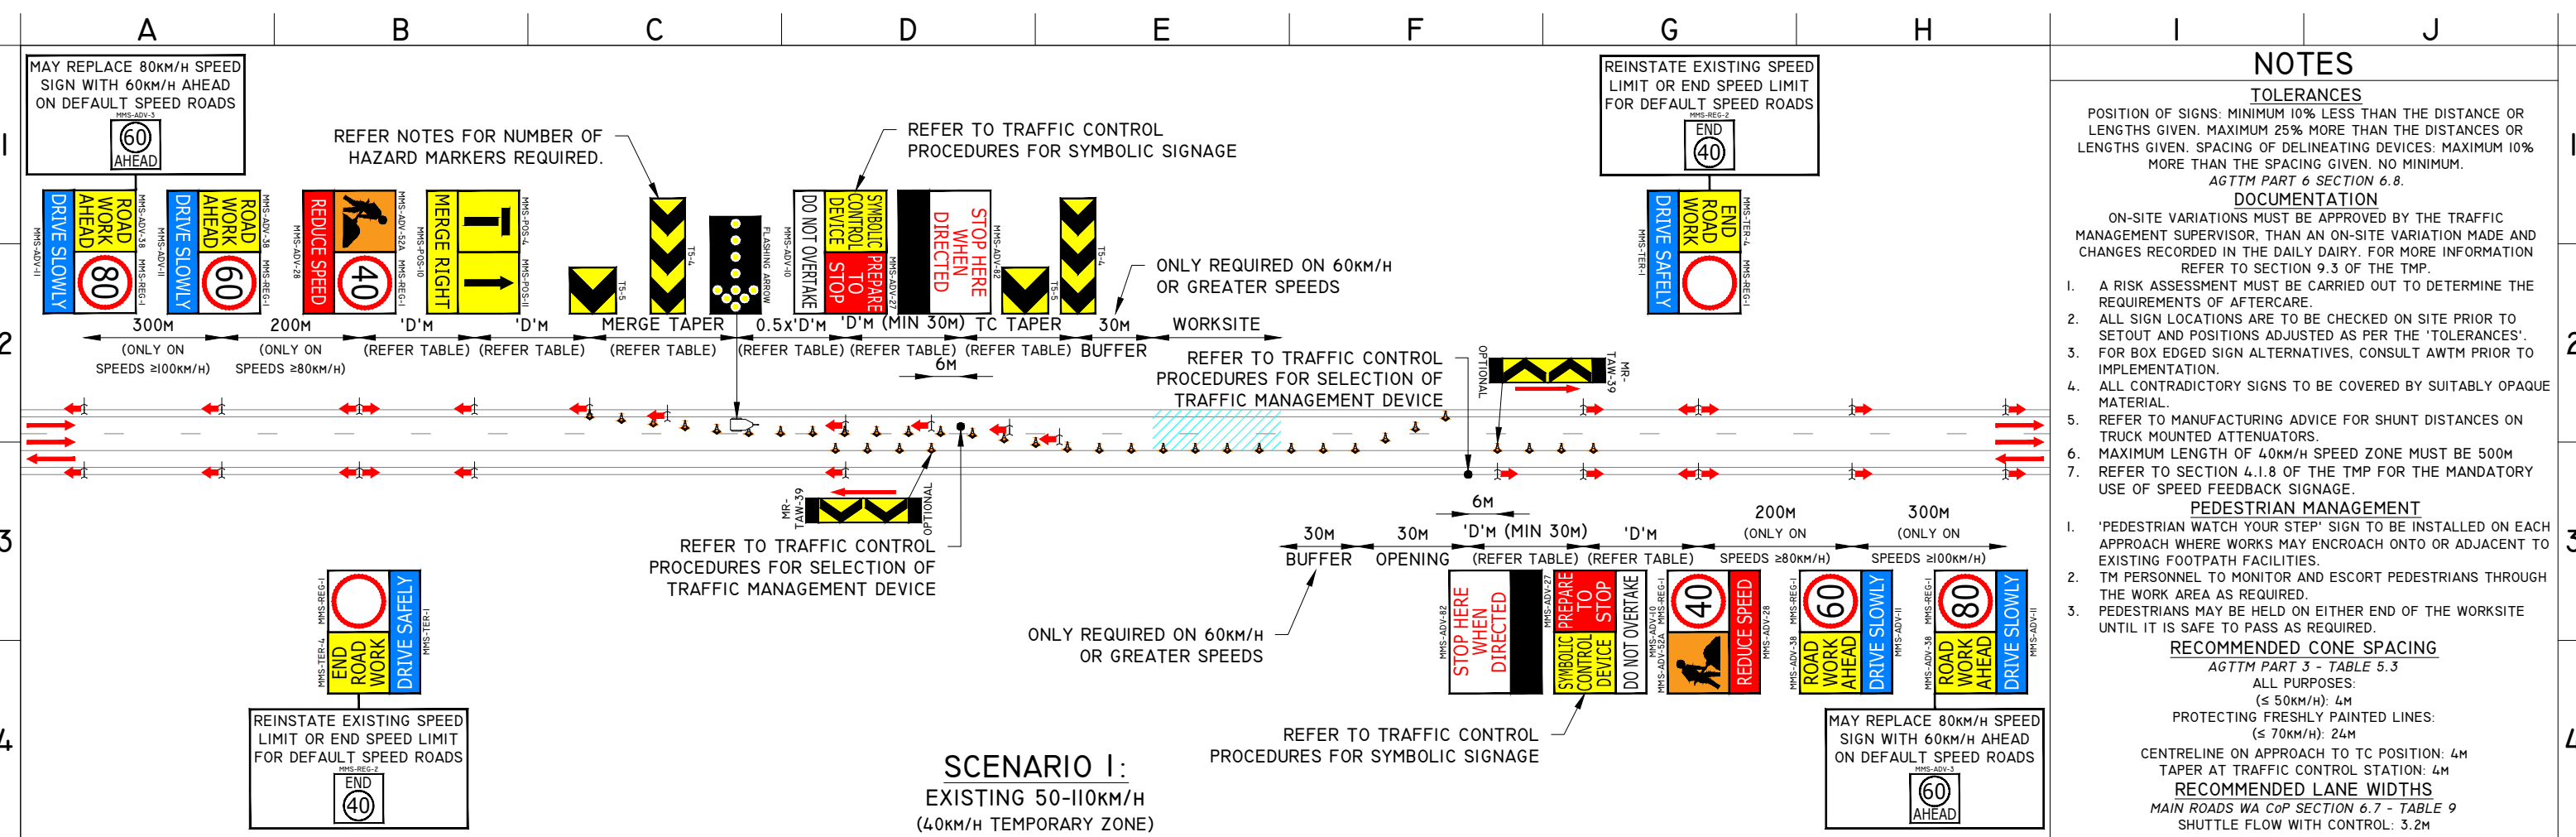

TRAFFIC CONTROL PROCEDURES

REFER TO TMP SECTION 4.1.7 PORTABLE TRAFFIC CONTROL DEVICES FOR MORE DETAILS

MANUAL TRAFFIC CONTROL

ACCREDITED TRAFFIC CONTROLLER (MMS-ADV-47, MMS-ADV-27, MMS-ADV-82)

PORTABLE TRAFFIC CONTROL DEVICE (PTCD) (MMS-ADV-79, MMS-ADV-27, MMS-ADV-82)

TEMPORARY TRAFFIC SIGNAL (MMS-ADV-48, MMS-ADV-27, R6-6)

END OF QUEUE PROTECTION

DEVICE MAY BE A TRAFFIC CONTROLLER, PORTABOOM OR TEMPORARY SIGNAL

MUST BE IMPLEMENTED ON ALL ROADS WITH A POSTED SPEED OF 80km/h OR GREATER. REFER TO TGS-TMC-RF-022, 023 AND 044 FOR MORE INFORMATION.

MANUAL TRAFFIC CONTROL IS NOT PERMITTED ON THE MAIN ROADS NETWORK WITH THE EXCEPTIONS LISTED UNDER SECTION 4.1.7 (PORTABLE TRAFFIC CONTROL DEVICES) OF THE TMP AND IN THE MAIN ROADS CODE OF PRACTICE.

ON ALL OTHER ROADS, PTCDS MUST BE USED UNDER THE FOLLOWING CONDITIONS:

- A PERMANENT SPEED LIMIT OF 90m/h OR MORE AND OVER 2,000vpd; OR
- A PERMANENT SPEED LIMIT OF 70km/h OR MORE AND OVER 10,000vpd.

PTCDs SHOULD BE CONSIDERED ON ALL WORKS AND ONLY BE SUPPLEMENTED WITH MANUAL TRAFFIC CONTROL UNDER AN AWTM/WTM RISK ASSESSMENT.

SHADOW VEHICLE INSET

SHADOW VEHICLE MAY BE DISPENSED WITH UNDER A RISK ASSESSMENT BY AN RTM AS PART OF THE TM ADVICE. IN THE ABSENCE OF THE SHADOW VEHICLE A LOOKOUT PERSON IS REQUIRED. REFER TO SECTION 4.5 OF THE TMP FOR MORE DETAILS.

SHADOW VEHICLE (20-40M BUFFER)

FLASHING ARROWBOARD ON TMA

VARIABLE MESSAGE BOARD DISPLAY 1, DISPLAY 2

TEMPORARY SPEED ZONE

REFER TO SECTION 4.5.1 OF THE TMP FOR TMA REQUIREMENTS

TABLES

SIGN SPACING		TAPER LENGTHS		
AGTMM PART 3 - TABLE 2.2		AGTMM PART 3 - TABLE 5.7		
SPEED LIMIT (KM/H)	DISTANCE ('D') (M)	SPEED LIMIT (KM/H)	TRAFFIC CONTROL TAPER (M)	MERGE TAPER (M)
55 OR LESS	15	45 OR LESS	15	15
56 TO 65	45	46 TO 55	15	30
GREATER THAN 65	EQUAL TO SPEED OF TRAFFIC IN KM/H	56 TO 65	30	60
MAXIMUM LENGTH OF SHUTTLE FLOW MAIN ROADS WA CoP SECTION 6.8.6 - TABLE 15		66 TO 75*	N/A	115
		76 TO 85*		130
		86 TO 95*		145
		96 TO 105*		160
		GREATER THAN 105*		180
VOLUMES (BOTH DIRECTION) (VPH)		*TAPER LENGTHS ARE BASED ON A: 3.5M WIDTH OF THE LANE TO BE CLOSED - LATERAL SHIFT TAPER LENGTH EQUAL TO 1.0M/s - MERGE TAPER LENGTH EQUAL TO 0.6M/s		
RESIDENTIAL STREET	60	TEMPORARY HAZARD MARKERS		
701 - 800	70	AGTMM PART 3 - 5.4.2 PAGE 65		
601 - 700	100	A CONTINUOUS LINE OF T5-4 HAZARD MARKERS MUST BE MADE USING THE FOLLOWING RECOMMENDED NUMBERS.		
501 - 600	150	NUMBER OF SHIFT MARKERS		
401 - 500	250	LENGTH OF TAPER		
351 - 400	400	2		
301- 350	600	4		
251 - 300	800	6		
201 - 250	1200	8		
151 - 200	1600	EVERY 20M		
≤ 150	2200	WITHIN A CLOSED LANE		