


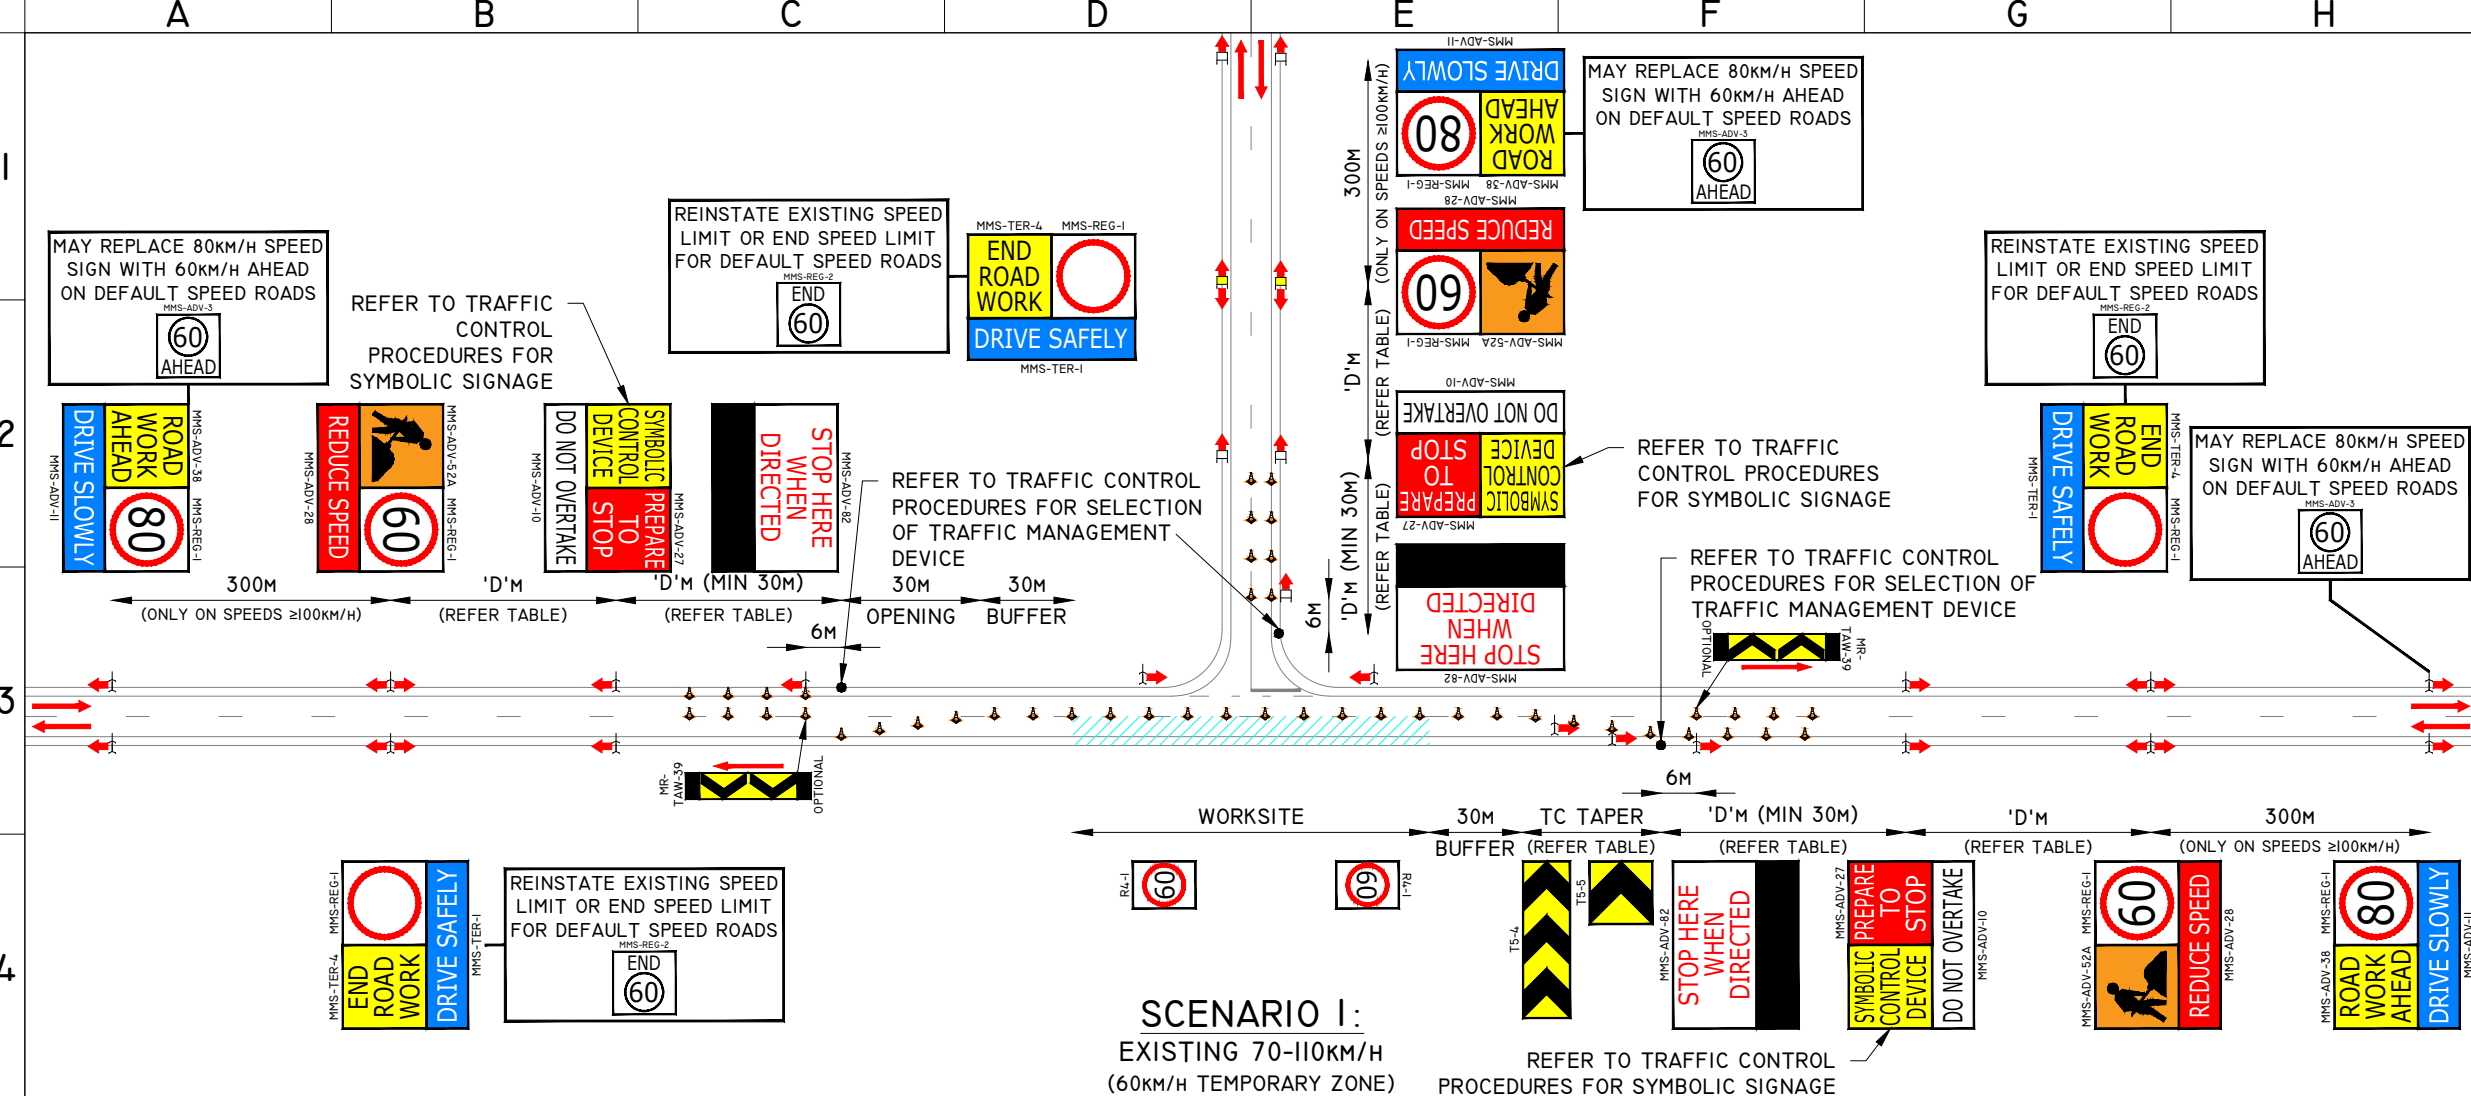

**NOTES**

**TOLERANCES**  
POSITION OF SIGNS:  
MINIMUM 10% LESS THAN THE DISTANCE OR LENGTHS GIVEN.  
MAXIMUM 25% MORE THAN THE DISTANCES OR LENGTHS GIVEN.  
SPACING OF DELINEATING DEVICES:  
MAXIMUM 10% MORE THAN THE SPACING GIVEN.  
NO MINIMUM.  
AGTTM PART 6 SECTION 6.8.

**DOCUMENTATION**  
ON-SITE VARIATIONS MUST BE APPROVED BY THE TRAFFIC MANAGEMENT SUPERVISOR, THAN AN ON-SITE VARIATION MADE AND CHANGES RECORDED IN THE DAILY DAIRY. FOR MORE INFORMATION REFER TO SECTION 9.3 OF THE TMP.

**GENERAL NOTES**

- A RISK ASSESSMENT MUST BE CARRIED OUT TO DETERMINE THE REQUIREMENTS OF AFTERCARE.
- ALL SIGN LOCATIONS ARE TO BE CHECKED ON SITE PRIOR TO SETOUT AND POSITIONS ADJUSTED AS PER THE 'TOLERANCES'.
- ALL CONTRADICTIONARY SIGNS TO BE COVERED BY SUITABLY OPAQUE MATERIAL.
- FOR BOX EDGED SIGN ALTERNATIVES, CONSULT AWTM PRIOR TO IMPLEMENTATION.
- REFER TO SECTION 4.1.8 OF THE TMP FOR THE MANDATORY USE OF SPEED FEEDBACK SIGNAGE

**PEDESTRIAN MANAGEMENT**

- 'PEDESTRIAN WATCH YOUR STEP' SIGN TO BE INSTALLED ON EACH APPROACH WHERE WORKS MAY ENCROACH ONTO OR ADJACENT TO EXISTING FOOTPATH FACILITIES.
- TM PERSONNEL TO MONITOR AND ESCORT PEDESTRIANS THROUGH THE WORK AREA AS REQUIRED.
- PEDESTRIANS MAY BE HELD ON EITHER END OF THE WORKSITE UNTIL IT IS SAFE TO PASS AS REQUIRED.

**RECOMMENDED CONE SPACING**  
AGTTM PART 3 - TABLE 5.3  
ALL PURPOSES:  
(60 - 70km/h): 12M  
PROTECTING FRESHLY PAINTED LINES:  
(≤ 70km/h): 24M  
CENTRELINE ON APPROACH TO TC POSITION: 4M  
TAPER AT TRAFFIC CONTROL STATION: 4M

**RECOMMENDED LANE WIDTHS**  
MAIN ROADS WA CoP SECTION 6.7 - TABLE 9  
SHUTTLE FLOW WITH CONTROL: 3.2M

**TRAFFIC CONTROL PROCEDURES**  
REFER TO TMP SECTION 4.1.7 PORTABLE TRAFFIC CONTROL DEVICES FOR MORE DETAILS

**MANUAL TRAFFIC CONTROL**

5 ACCREDITED TRAFFIC CONTROLLER

6 PORTABLE TRAFFIC CONTROL DEVICE (PTCD)

7 PORTABOOM

8 TEMPORARY TRAFFIC SIGNAL

**END OF QUEUE PROTECTION**

DEVICE MAY BE A TRAFFIC CONTROLLER, PORTABOOM OR TEMPORARY SIGNAL

MUST BE IMPLEMENTED ON ALL ROADS WITH A POSTED SPEED OF 80km/h OR GREATER. REFER TO TGS-TMC-RF-022, 023 AND 044 FOR MORE INFORMATION.

MANUAL TRAFFIC CONTROL IS NOT PERMITTED ON THE MAIN ROADS NETWORK WITH THE EXCEPTIONS LISTED UNDER SECTION 4.1.7 (PORTABLE TRAFFIC CONTROL DEVICES) OF THE TMP AND IN THE MAIN ROADS CODE OF PRACTICE.

ON ALL OTHER ROADS, PTCDS MUST BE USED UNDER THE FOLLOWING CONDITIONS:

- A PERMANENT SPEED LIMIT OF 90m/h OR MORE AND OVER 2,000VPD; OR
- A PERMANENT SPEED LIMIT OF 70km/h OR MORE AND OVER 10,000VPD.

PTCDs SHOULD BE CONSIDERED ON ALL WORKS AND ONLY BE SUPPLEMENTED WITH MANUAL TRAFFIC CONTROL UNDER AN AWTM/WTM RISK ASSESSMENT.

**SHADOW VEHICLE INSET**  
SHADOW VEHICLE MAY BE DISPENSED WITH UNDER A RISK ASSESSMENT BY AN RTM AS PART OF THE TM ADVISE. IN THE ABSENCE OF THE SHADOW VEHICLE A LOOKOUT PERSON IS REQUIRED. REFER TO SECTION 4.5 OF THE TMP FOR MORE DETAILS.

**SHADOW VEHICLE**

FLASHING ARROW

20-40M BUFFER

**FLASHING ARROWBOARD ON TMA**

VARIABLE MESSAGE BOARD DISPLAY 1

VARIABLE MESSAGE BOARD DISPLAY 2

TEMPORARY SPEED ZONE

REFER TO SECTION 4.5.1 OF THE TMP FOR TMA REQUIREMENTS

| TABLES                                               |                                      |
|------------------------------------------------------|--------------------------------------|
| TAPER LENGTHS                                        |                                      |
| AGTTM PART 3 - TABLE 5.7                             |                                      |
| SPEED LIMIT<br>(KM/H)                                | TRAFFIC CONTROL TAPER<br>(M)         |
| 45 OR LESS                                           | 15                                   |
| 46 TO 55                                             | 15                                   |
| 56 TO 65                                             | 30                                   |
| 66 TO 75*                                            | N/A                                  |
| 76 TO 85*                                            |                                      |
| 86 TO 95*                                            |                                      |
| 96 TO 105*                                           |                                      |
| GREATER THAN 105*                                    |                                      |
| *TAPER LENGTHS ARE BASED ON A:                       |                                      |
| • 3.5M WIDTH OF THE LANE TO BE CLOSED                |                                      |
| • LATERAL SHIFT TAPER LENGTH EQUAL TO 1.0M/s         |                                      |
| • MEDIAN SPEED FOR EACH RANGE (I.E 76 - 85 = 80KM/H) |                                      |
| SIGN SPACING                                         |                                      |
| AGTTM PART 3 - TABLE 2.2                             |                                      |
| SPEED LIMIT<br>(KM/H)                                | DISTANCE ('D')<br>(M)                |
| 55 OR LESS                                           | 15                                   |
| 56 TO 65                                             | 45                                   |
| GREATER THAN 65                                      | EQUAL TO SPEED OF<br>TRAFFIC IN KM/H |
| MAXIMUM LENGTH OF SHUTTLE FLOW                       |                                      |
| MAIN ROADS WA CoP SECTION 6.8.6 - TABLE 15           |                                      |
| VOLUMES (BOTH DIRECTION)<br>(VPH)                    | LENGTH (BETWEEN TCs)<br>(M)          |
| RESIDENTIAL STREET                                   | 60                                   |
| 701 - 800                                            | 70                                   |
| 601 - 700                                            | 100                                  |
| 501 - 600                                            | 150                                  |
| 401 - 500                                            | 250                                  |
| 351 - 400                                            | 400                                  |
| 301- 350                                             | 600                                  |
| 251 - 300                                            | 800                                  |
| 201 - 250                                            | 1200                                 |
| 151 - 200                                            | 1600                                 |
| ≤150                                                 | 2200                                 |
| G                                                    | H                                    |

**LEGEND**

- EXISTING ROAD
- PROPOSED CONES
- WORKSITE

**mainroads WESTERN AUSTRALIA**

**METROPOLITAN REGIONS TRAFFIC MANAGEMENT BRANCH**  
WATERLOO CRESCENT  
TELEPHONE (08) 138 138  
EAST PERTH 6004

|                            |                   |   |               |
|----------------------------|-------------------|---|---------------|
| DATE OF DRAWING            | 2025 JULY         | SCALE   | -             |
| LOCAL GOVERNMENT AUTHORITY | -                 | POSTED SPEED   | 70-110KM/H    |
| ROAD AUTHORITY             | MAIN ROADS WA     | WORKSITE SPEED                                                                                                  | 60KM/H        |
| CHECKED BY                 | TYLER HARTLEY     | SIGNATURE   | Tyler Hartley |
| ACCREDITATION              | RTM-0066          | SIGNATURE   | Michael Reed  |
| DESIGNED BY                | MICHAEL REED      | SIGNATURE   | Michael Reed  |
| ACCREDITATION              | AWTM-23-11536-02  | GENERIC TRAFFIC GUIDANCE SCHEME<br>REVERSIBLE FLOW SETUPS<br>SINGLE LANE ROAD<br>WORKSITE BETWEEN 1.2M AND 3.0M |               |
| DRAWING NO                 | 0922-01531-RF-011 | REVISION   | 6             |