
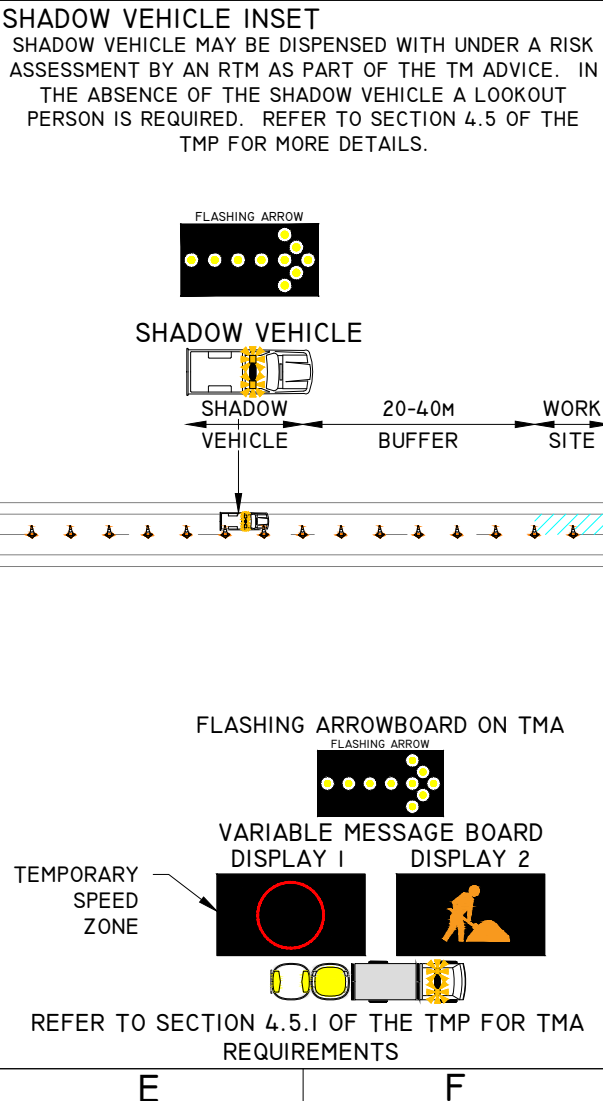
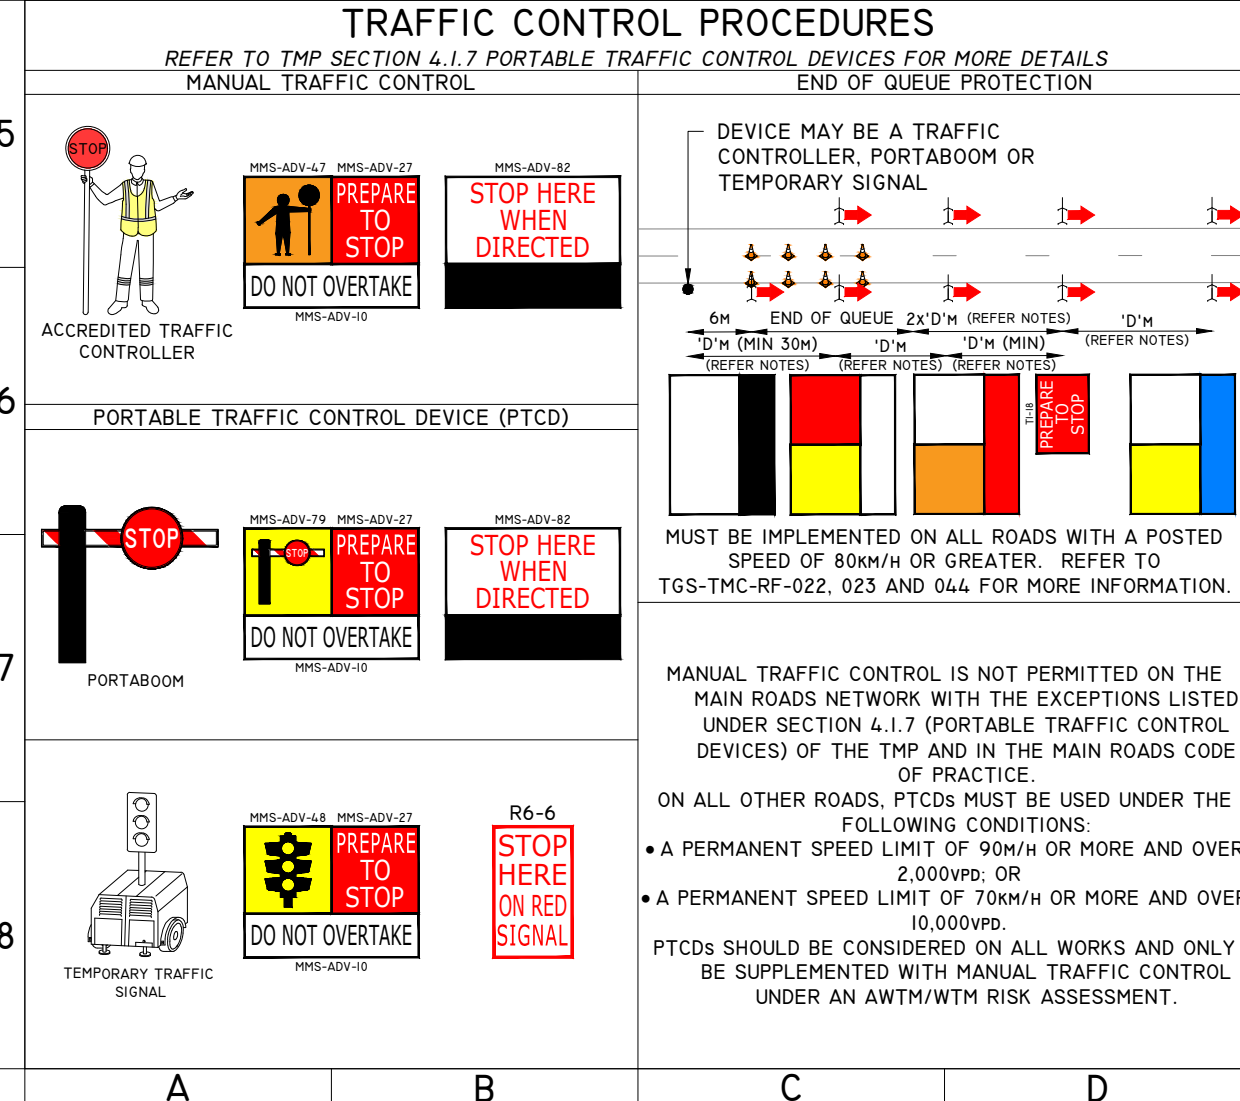


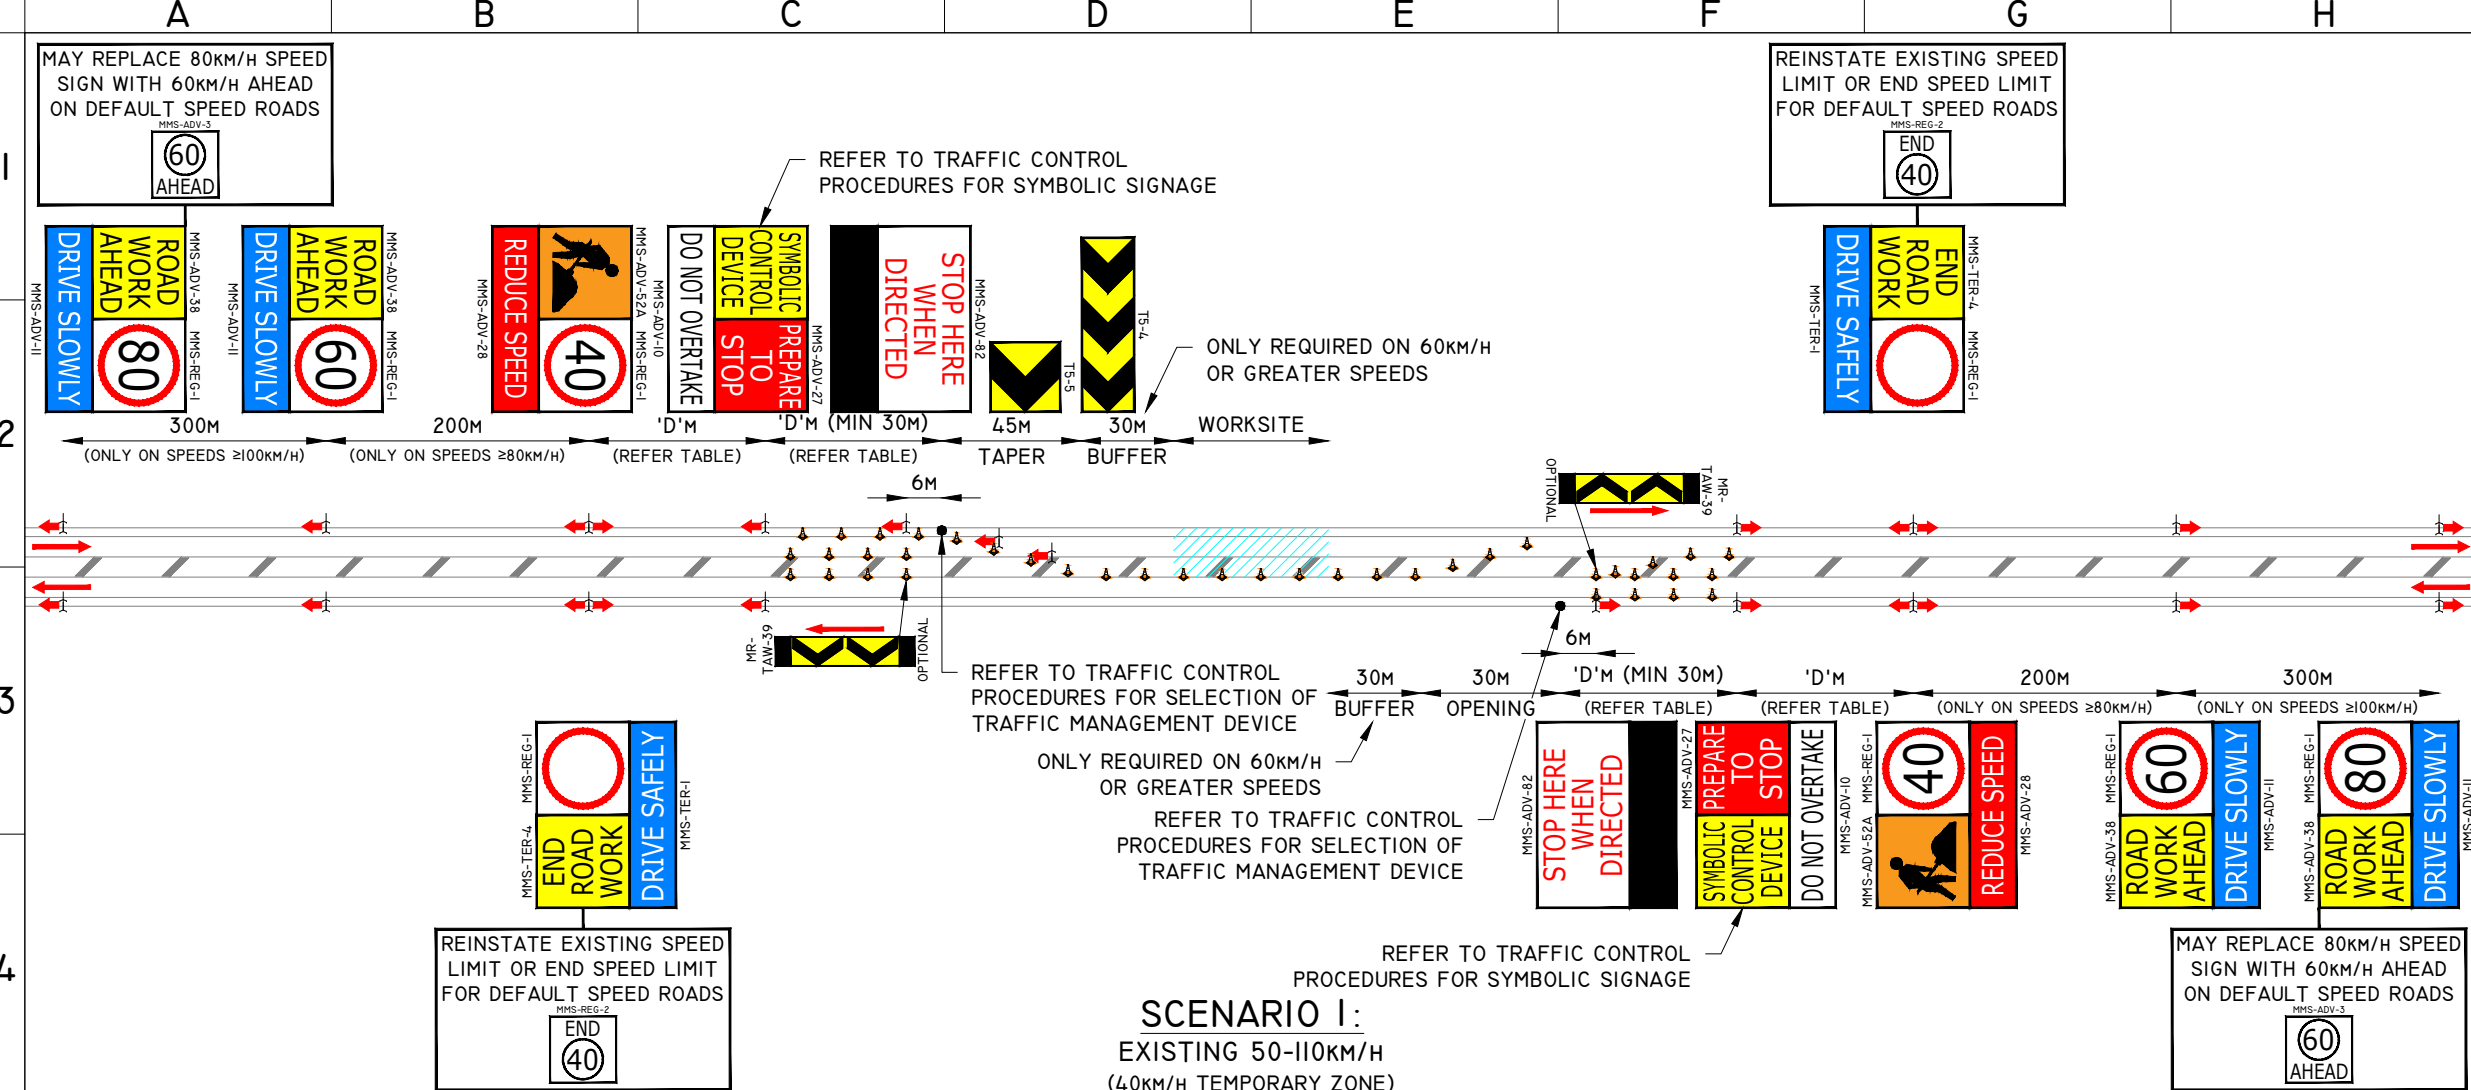

**TABLES**

**TAPER LENGTHS**

AGTTM PART 3 - TABLE 5.7

| SPEED LIMIT (KM/H) | TRAFFIC CONTROL TAPER (M) |
|--------------------|---------------------------|
| 45 OR LESS         | 15                        |
| 46 TO 55           | 15                        |
| 56 TO 65           | 30                        |
| 66 TO 75*          |                           |
| 76 TO 85*          |                           |
| 86 TO 95*          |                           |
| 96 TO 105*         |                           |
| GREATER THAN 105*  |                           |

\*TAPER LENGTHS ARE BASED ON A:  
• 3.5m WIDTH OF THE LANE TO BE CLOSED  
• LATERAL SHIFT TAPER LENGTH EQUAL TO 1.0m/s  
• MEDIAN SPEED FOR EACH RANGE (I.E 76 - 85 = 80km/h)

**SIGN SPACING**

AGTTM PART 3 - TABLE 2.2

| SPEED LIMIT (KM/H) | DISTANCE ('D')                    |
|--------------------|-----------------------------------|
| 55 OR LESS         | 15                                |
| 56 TO 65           | 45                                |
| GREATER THAN 65    | EQUAL TO SPEED OF TRAFFIC IN KM/H |

**MAXIMUM LENGTH OF SHUTTLE FLOW**

MAIN ROADS WA CoP SECTION 6.8.6 - TABLE 15

| VOLUMES (BOTH DIRECTION) (VPH) | LENGTH (BETWEEN TCS) (M) |
|--------------------------------|--------------------------|
| RESIDENTIAL STREET             | 60                       |
| 701 - 800                      | 70                       |
| 601 - 700                      | 100                      |
| 501 - 600                      | 150                      |
| 401 - 500                      | 250                      |
| 351 - 400                      | 400                      |
| 301 - 350                      | 600                      |
| 251 - 300                      | 800                      |
| 201 - 250                      | 1200                     |
| 151 - 200                      | 1600                     |
| ≤ 150                          | 2200                     |

**NOTES**

**TOLERANCES**

POSITION OF SIGNS:  
MINIMUM 10% LESS THAN THE DISTANCE OR LENGTHS GIVEN.  
MAXIMUM 25% MORE THAN THE DISTANCES OR LENGTHS GIVEN.  
SPACING OF DELINEATING DEVICES:  
MAXIMUM 10% MORE THAN THE SPACING GIVEN.  
NO MINIMUM.

AGTTM PART 6 SECTION 6.8.

**DOCUMENTATION**

ON-SITE VARIATIONS MUST BE APPROVED BY THE TRAFFIC MANAGEMENT SUPERVISOR, THAN AN ON-SITE VARIATION MADE AND CHANGES RECORDED IN THE DAILY DAIRY. FOR MORE INFORMATION REFER TO SECTION 9.3 OF THE TMP.

**GENERAL NOTES**

- A RISK ASSESSMENT MUST BE CARRIED OUT TO DETERMINE THE REQUIREMENTS OF AFTERCARE.
- ALL SIGN LOCATIONS ARE TO BE CHECKED ON SITE PRIOR TO SETOUT AND POSITIONS ADJUSTED AS PER THE 'TOLERANCES'.
- ALL CONTRADICTORY SIGNS TO BE COVERED BY SUITABLY OPAQUE MATERIAL.
- FOR BOX EDGED SIGN ALTERNATIVES, CONSULT AWTM PRIOR TO IMPLEMENTATION.
- MAXIMUM LENGTH OF 40km/h SPEED ZONE MUST BE 500M.
- REFER TO SECTION 4.1.8 OF THE TMP FOR THE MANDATORY USE OF SPEED FEEDBACK SIGNAGE.

**PEDESTRIAN MANAGEMENT**

- 'PEDESTRIAN WATCH YOUR STEP' SIGN TO BE INSTALLED ON EACH APPROACH WHERE WORKS MAY ENCRACH ONTO OR ADJACENT TO EXISTING FOOTPATH FACILITIES.
- TM PERSONNEL TO MONITOR AND ESCORT PEDESTRIANS THROUGH THE WORK AREA AS REQUIRED.
- PEDESTRIANS MAY BE HELD ON EITHER END OF THE WORKSITE UNTIL IT IS SAFE TO PASS AS REQUIRED.

**RECOMMENDED CONE SPACING**

AGTTM PART 3 - TABLE 5.3

ALL PURPOSES:  
≤ 50km/h: 4m  
PROTECTING FRESHLY PAINTED LINES:  
≤ 70km/h: 24m

CENTRELINE ON APPROACH TO TC POSITION: 4m  
TAPER AT TRAFFIC CONTROL STATION: 4m

**RECOMMENDED LANE WIDTHS**

MAIN ROADS WA CoP SECTION 6.7 - TABLE 9  
SHUTTLE FLOW WITH CONTROL: 3.2m

**LEGEND**

- EXISTING ROAD
- PROPOSED CONES
- WORKSITE

**mainroads WESTERN AUSTRALIA**

**METROPOLITAN REGIONS TRAFFIC MANAGEMENT BRANCH**

WATERLOO CRESCENT  
TELEPHONE (08) 138 138  
EAST PERTH 6004

**DATE OF DRAWING** 2025 JULY  
**SCALE** -

**LOCAL GOVERNMENT AUTHORITY** -  
**POSTED SPEED** 50-110km/h

**ROAD AUTHORITY** MAIN ROADS WA  
**WORKSITE SPEED** 40km/h

**CHECKED BY** TYLER HARTLEY  
**SIGNATURE** Tyler Hartley

**ACCREDITATION** RTM-0066  
**SIGNATURE** Michael Reed

**DESIGNED BY** MICHAEL REED  
**ACCREDITATION** AWTM-23-11536-02  
**SIGNATURE** Michael Reed

**GENERIC TRAFFIC GUIDANCE SCHEME REVERSIBLE FLOW SETUPS SINGLE LANE ROAD WORKSITE WITHIN 1.2M**

**DRAWING NO** 0922-01531-RF-017  
**REVISION** 6