


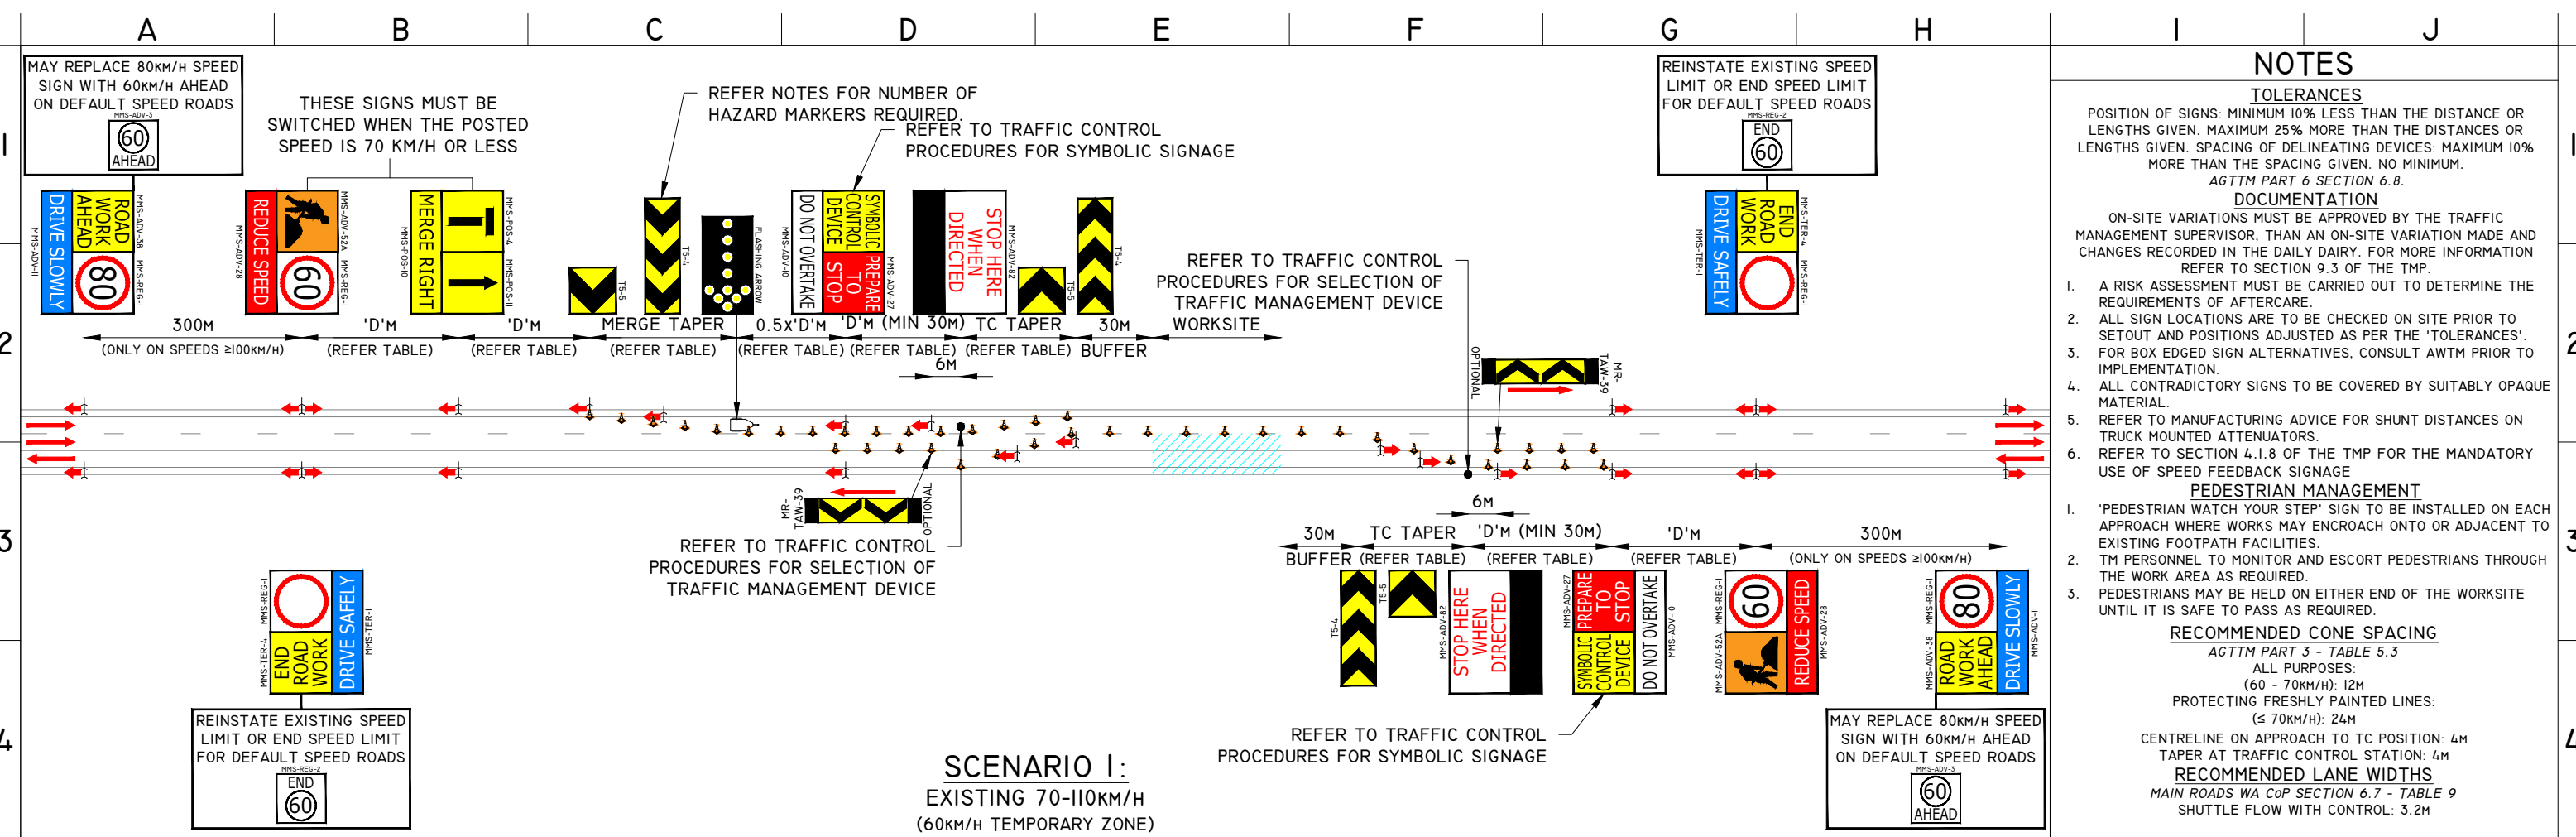

TRAFFIC CONTROL PROCEDURES
REFER TO TMP SECTION 4.1.7 PORTABLE TRAFFIC CONTROL DEVICES FOR MORE DETAILS

MANUAL TRAFFIC CONTROL
ACCREDITED TRAFFIC CONTROLLER: MMS-ADV-47, MMS-ADV-27, MMS-ADV-82, MMS-ADV-10. Signs: DO NOT OVERTAKE, STOP HERE WHEN DIRECTED.

PORTABLE TRAFFIC CONTROL DEVICE (PTCD)
PORTABOOM: MMS-ADV-79, MMS-ADV-27, MMS-ADV-82, MMS-ADV-10. Signs: DO NOT OVERTAKE, STOP HERE WHEN DIRECTED.


TEMPORARY TRAFFIC SIGNAL
TEMPORARY TRAFFIC SIGNAL: MMS-ADV-48, MMS-ADV-27, R6-6. Signs: DO NOT OVERTAKE, STOP HERE ON RED SIGNAL.

END OF QUEUE PROTECTION
DEVICE MAY BE A TRAFFIC CONTROLLER, PORTABOOM OR TEMPORARY SIGNAL. Signs: 6M, END OF QUEUE, 2x'D'M, 'D'M (MIN 30M), 'D'M (REFER NOTES).

SHADOW VEHICLE INSET
SHADOW VEHICLE MAY BE DISPENSED WITH UNDER A RISK ASSESSMENT BY AN RTM AS PART OF THE TM ADVICE. IN THE ABSENCE OF THE SHADOW VEHICLE A LOOKOUT PERSON IS REQUIRED. REFER TO SECTION 4.5 OF THE TMP FOR MORE DETAILS. Signs: FLASHING ARROW, SHADOW VEHICLE, 20-40M, BUFFER, WORK SITE.

FLASHING ARROWBOARD ON TMA
FLASHING ARROW, VARIABLE MESSAGE BOARD DISPLAY 1, DISPLAY 2. Signs: TEMPORARY SPEED ZONE.

REFER TO SECTION 4.5.1 OF THE TMP FOR TMA REQUIREMENTS

 A		B		C		D		E		F		G		H		I		J	
  METROPOLITAN REGIONS TRAFFIC MANAGEMENT BRANCH WATERLOO CRESCENT TELEPHONE (08) 158 158 EAST PERTH 6004		DATE OF DRAWING 2025 JULY		DESIGNED BY MICHAEL REED		ACCREDITATION AWTM-23-11536-02		SIGNATURE 		LEGEND				GENERIC TRAFFIC GUIDANCE SCHEME REVERSIBLE FLOW SETUPS OVERTAKING LANE WORKSITE BETWEEN 1.2M AND 3.0M					
		POSTED SPEED 70-110KM/H		CHECKED BY TYLER HARTLEY		ACCREDITATION RTM-0066		SIGNATURE 											
		WORKSITE SPEED 60KM/H		SCALE -		ROAD AUTHORITY MAIN ROADS WA		LOCAL GOVERNMENT AUTHORITY -		EXISTING ROAD  PROPOSED CONES  WORKSITE				DRAWING NO 0922-01531-RF-030		REVISION 6			