


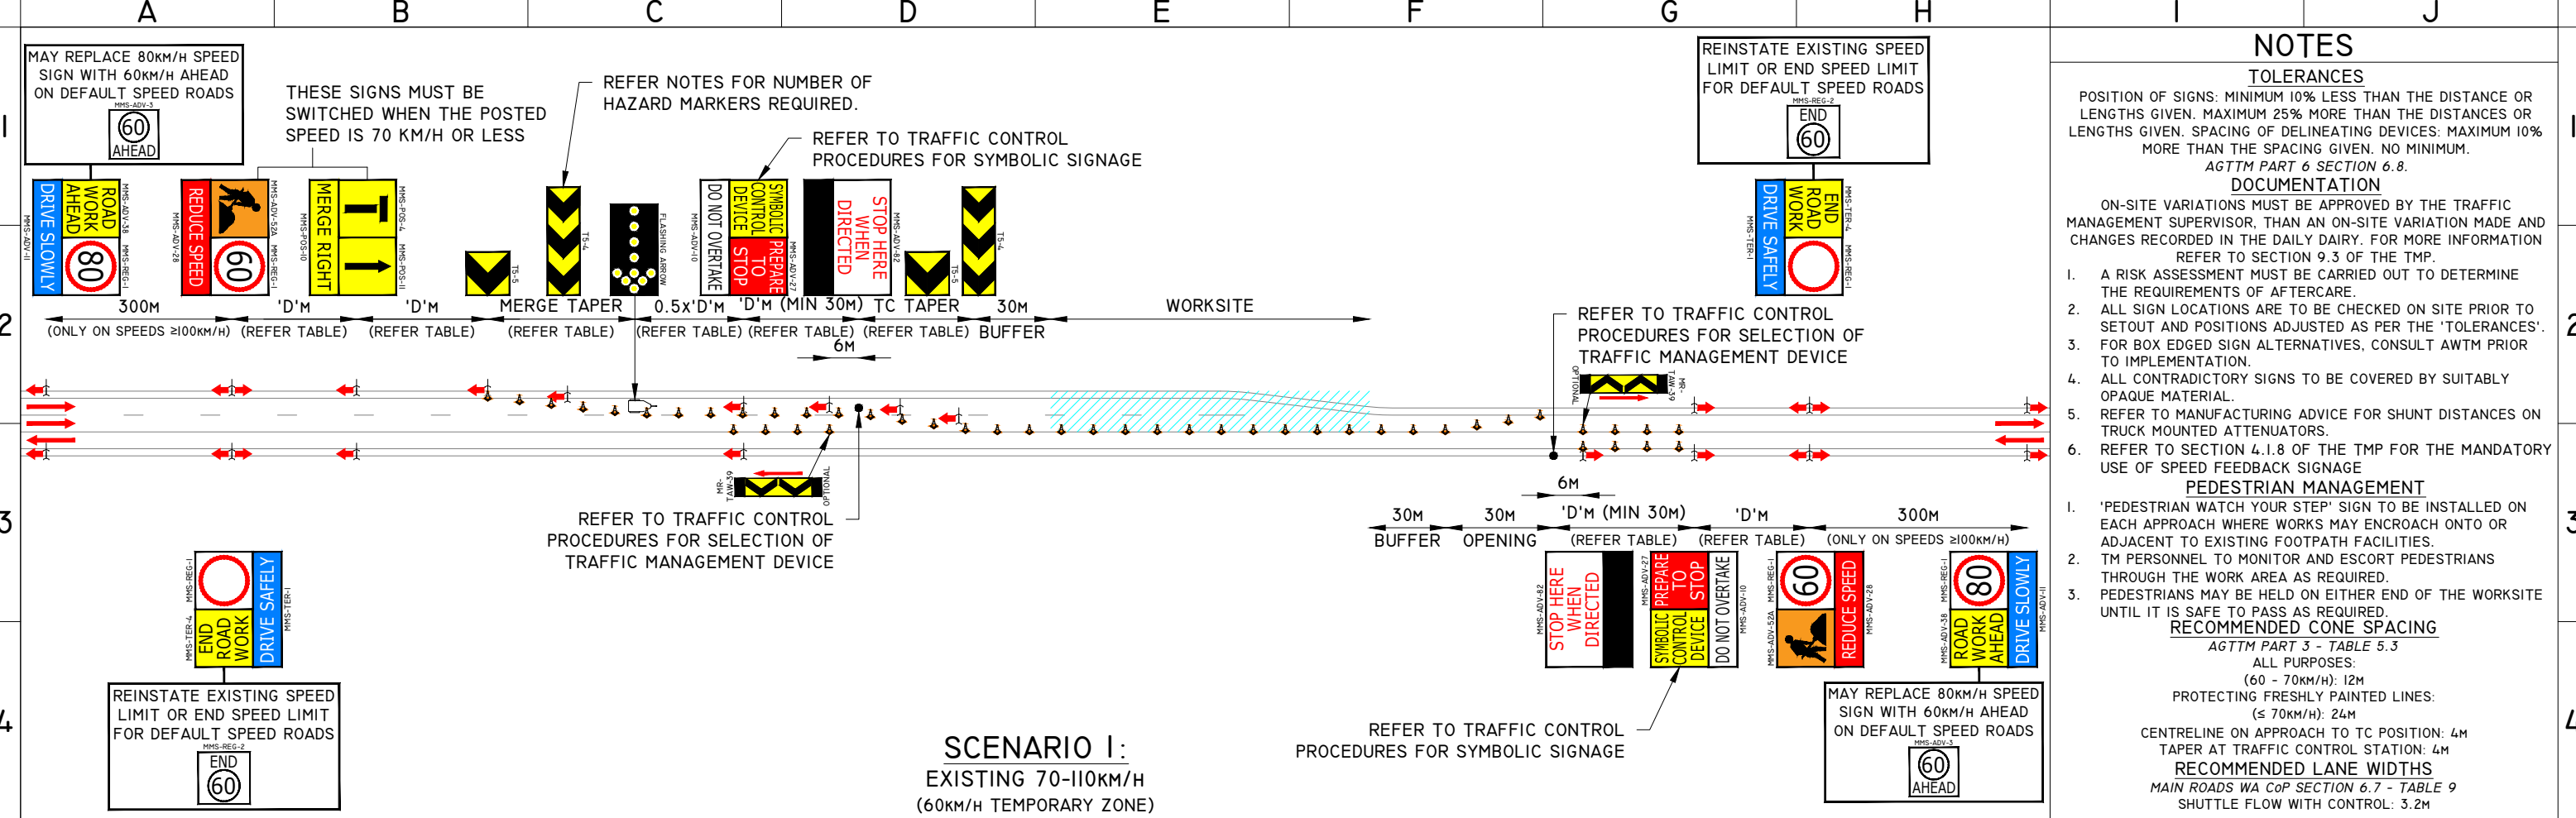

TRAFFIC CONTROL PROCEDURES

REFER TO TMP SECTION 4.1.7 PORTABLE TRAFFIC CONTROL DEVICES FOR MORE DETAILS

MANUAL TRAFFIC CONTROL

ACCREDITED TRAFFIC CONTROLLER

PORTABLE TRAFFIC CONTROL DEVICE (PTCD)

PORTABOOM

TEMPORARY TRAFFIC SIGNAL

SHADOW VEHICLE INSET

SHADOW VEHICLE MAY BE DISPENSED WITH UNDER A RISK ASSESSMENT BY AN RTM AS PART OF THE TM ADVICE. IN THE ABSENCE OF THE SHADOW VEHICLE A LOOKOUT PERSON IS REQUIRED. REFER TO SECTION 4.5 OF THE TMP FOR MORE DETAILS.

SHADOW VEHICLE

FLASHING ARROWBOARD ON TMA

TEMPORARY SPEED ZONE

REFER TO SECTION 4.5.1 OF THE TMP FOR TMA REQUIREMENTS

TABLES

SIGN SPACING	
AGTTM PART 3 - TABLE 2.2	
SPEED LIMIT (KM/H)	DISTANCE ('D')
55 OR LESS	15
56 TO 65	45
GREATER THAN 65	EQUAL TO SPEED OF TRAFFIC IN KM/H

MAXIMUM LENGTH OF SHUTTLE FLOW	
MAIN ROADS WA CoP SECTION 6.8.6 - TABLE 15	
VOLUMES (BOTH DIRECTION) (VPH)	LENGTH (BETWEEN TCS) (M)
RESIDENTIAL STREET	60
701 - 800	70
601 - 700	100
501 - 600	150
401 - 500	250
351 - 400	400
301 - 350	600
251 - 300	800
201 - 250	1200
151 - 200	1600
≤ 150	2200

TAPER LENGTHS		
AGTTM PART 3 - TABLE 5.7		
SPEED LIMIT (KM/H)	TRAFFIC CONTROL TAPER (M)	MERGE TAPER (M)
45 OR LESS	15	15
46 TO 55	15	30
56 TO 65	30	60
66 TO 75*	N/A	115
76 TO 85*		130
86 TO 95*		145
96 TO 105*		160
GREATER THAN 105*		180

*TAPER LENGTHS ARE BASED ON A:
• 3.5M WIDTH OF THE LANE TO BE CLOSED
• LATERAL SHIFT TAPER LENGTH EQUAL TO 1.0M/s
• MERGE TAPER LENGTH EQUAL TO 0.6M/s
• MEDIAN SPEED FOR EACH RANGE (I.E 76 - 85 = 80KM/H)

TEMPORARY HAZARD MARKERS

AGTTM PART 3 - 5.4.2 PAGE 65

A CONTINUOUS LINE OF T5-4 HAZARD MARKERS MUST BE MADE USING THE FOLLOWING RECOMMENDED NUMBERS.	NUMBER OF SHIFT MARKERS	LENGTH OF TAPER
	2	≤60M
	4	≤115M
	6	≤130M
	8	≤145M
	EVERY 20M	WITHIN A CLOSED LANE