


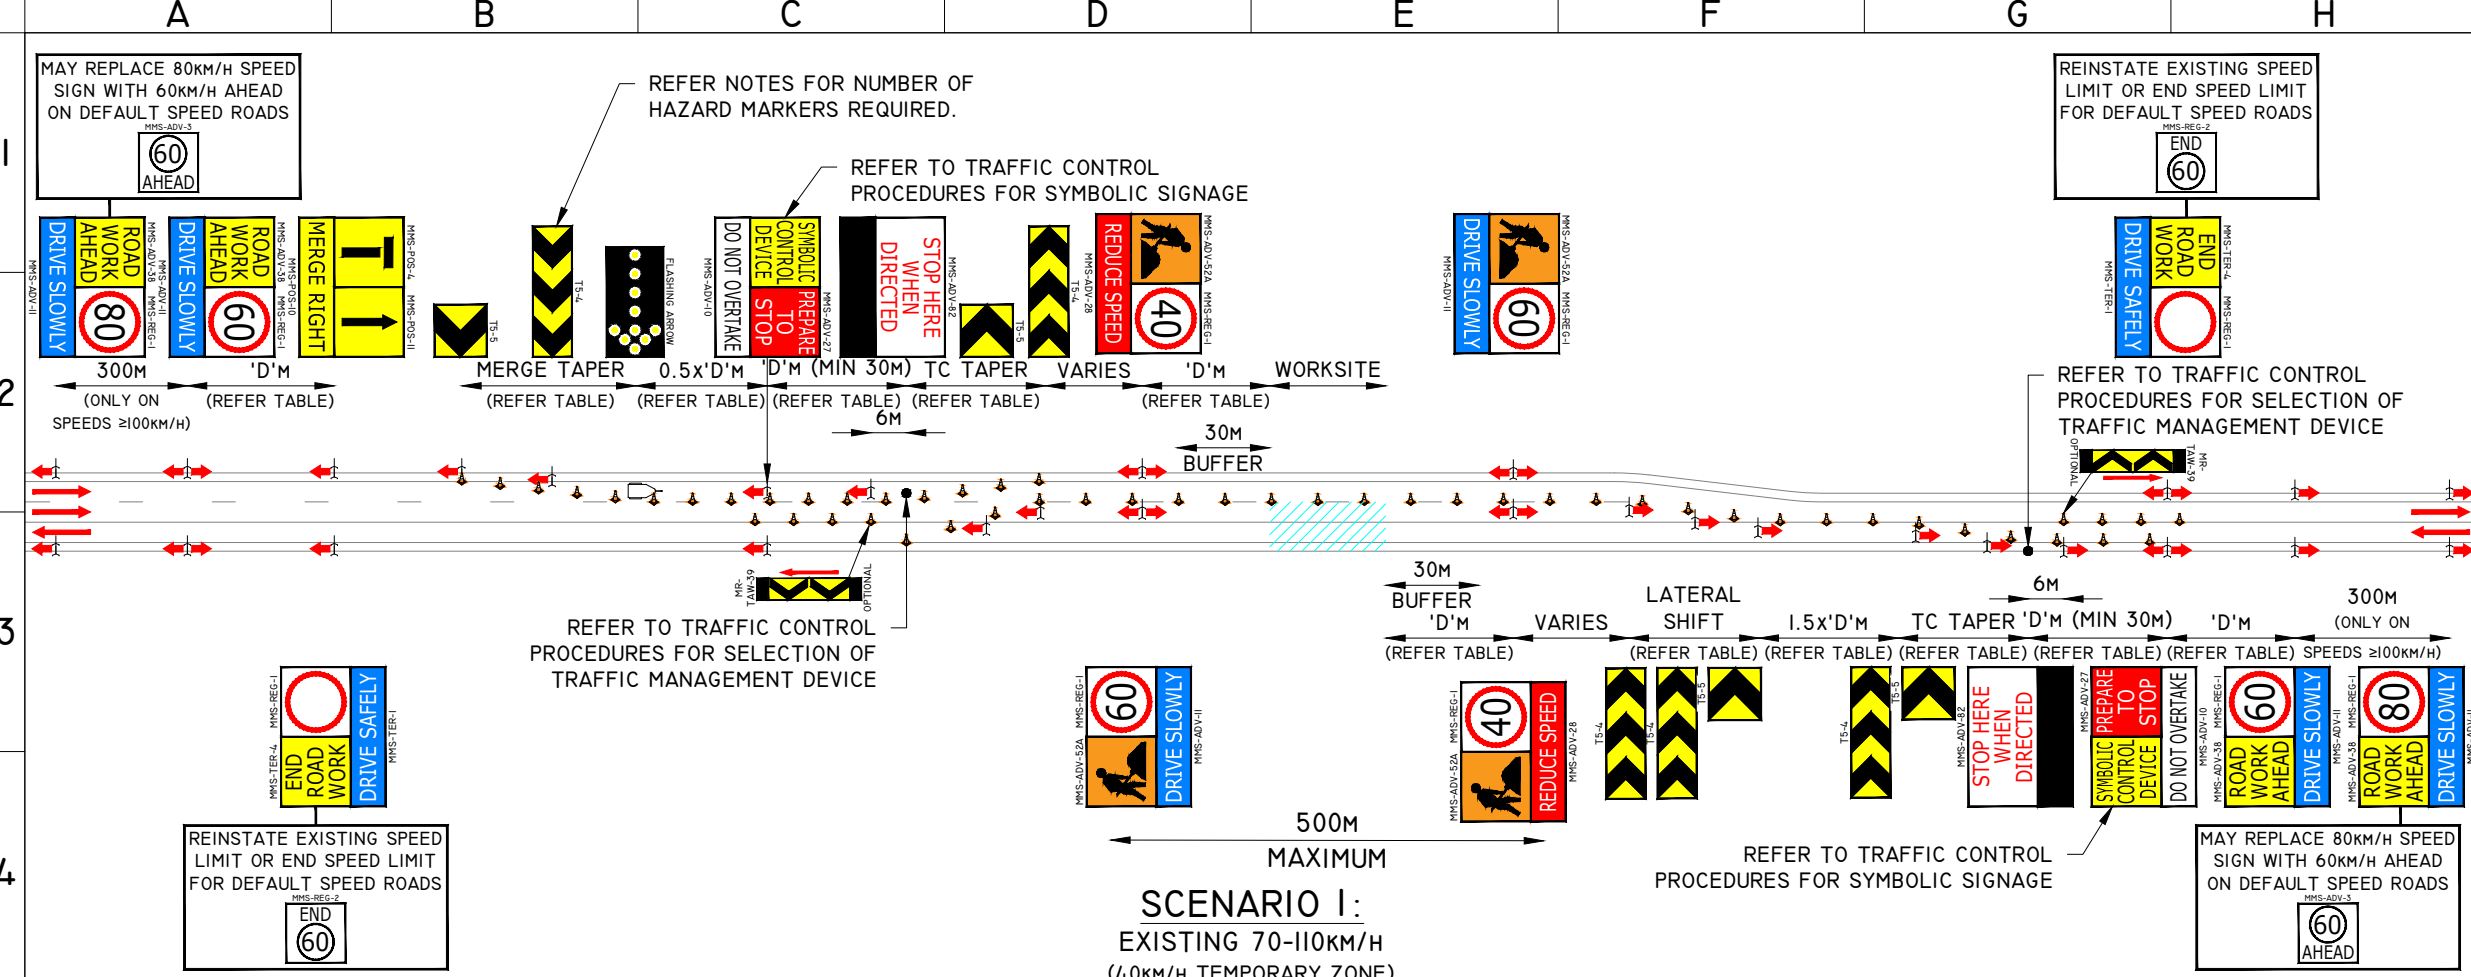

NOTES

TOLERANCES

DOCUMENTATION

PEDESTRIAN MANAGEMENT

RECOMMENDED CONE SPACING

TRAFFIC CONTROL PROCEDURES

REFER TO TMP SECTION 4.1.7 PORTABLE TRAFFIC CONTROL DEVICES FOR MORE DETAILS

MANUAL TRAFFIC CONTROL

ACCREDITED TRAFFIC CONTROLLER

PORTABLE TRAFFIC CONTROL DEVICE (PTCD)

PORTABOOM

TEMPORARY TRAFFIC SIGNAL

SHADOW VEHICLE INSET

SHADOW VEHICLE

FLASHING ARROWBOARD ON TMA

TEMPORARY SPEED ZONE

REFER TO SECTION 4.5.1 OF THE TMP FOR TMA REQUIREMENTS

TABLES

SIGN SPACING

MAXIMUM LENGTH OF SHUTTLE FLOW

RECOMMENDED LANE WIDTHS

TAPER LENGTHS

TEMPORARY HAZARD MARKERS