



SCENARIO 1:

- NOT TO BE USED ON FREEWAYS OR HIGH SPEED / VOLUME HIGHWAYS

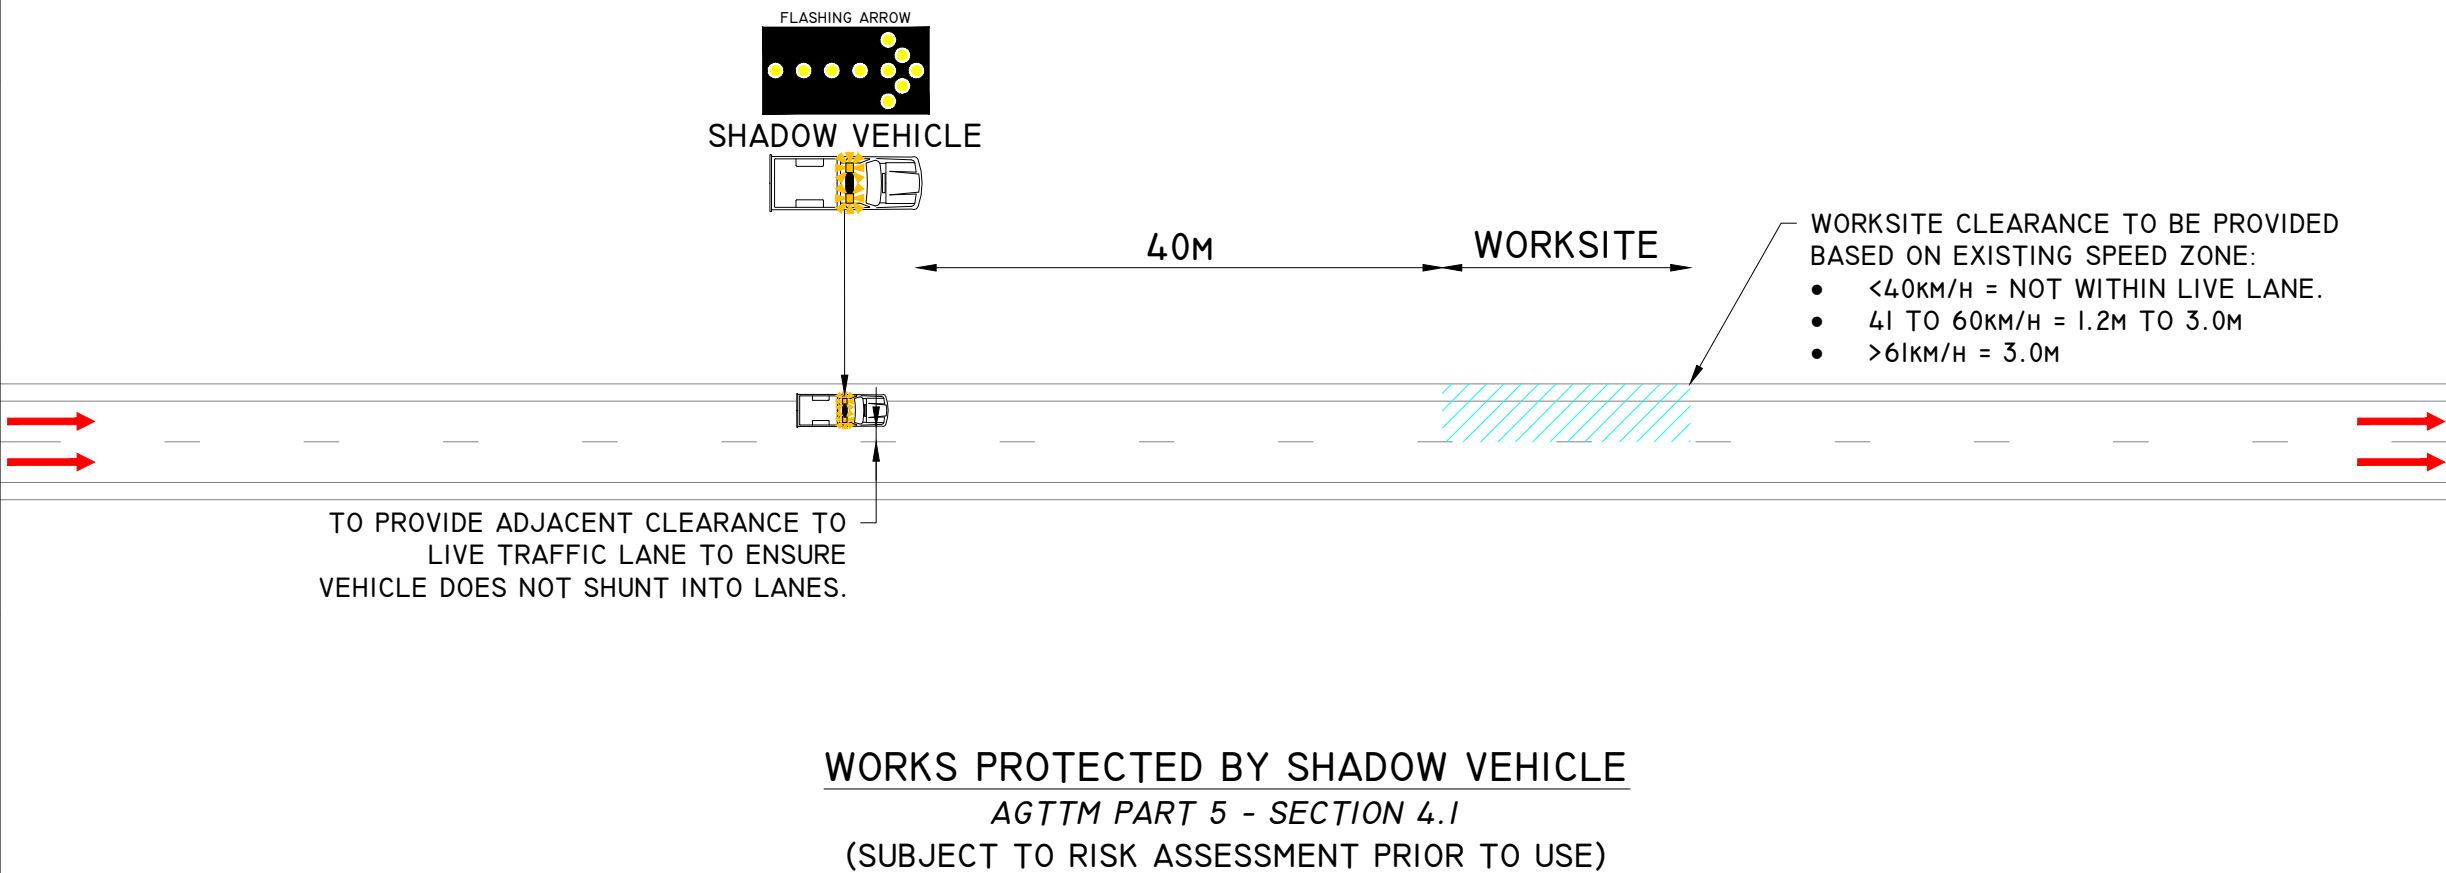

SCENARIO 2:

- NOT TO BE USED ON FREEWAYS OR HIGH SPEED / VOLUME HIGHWAYS

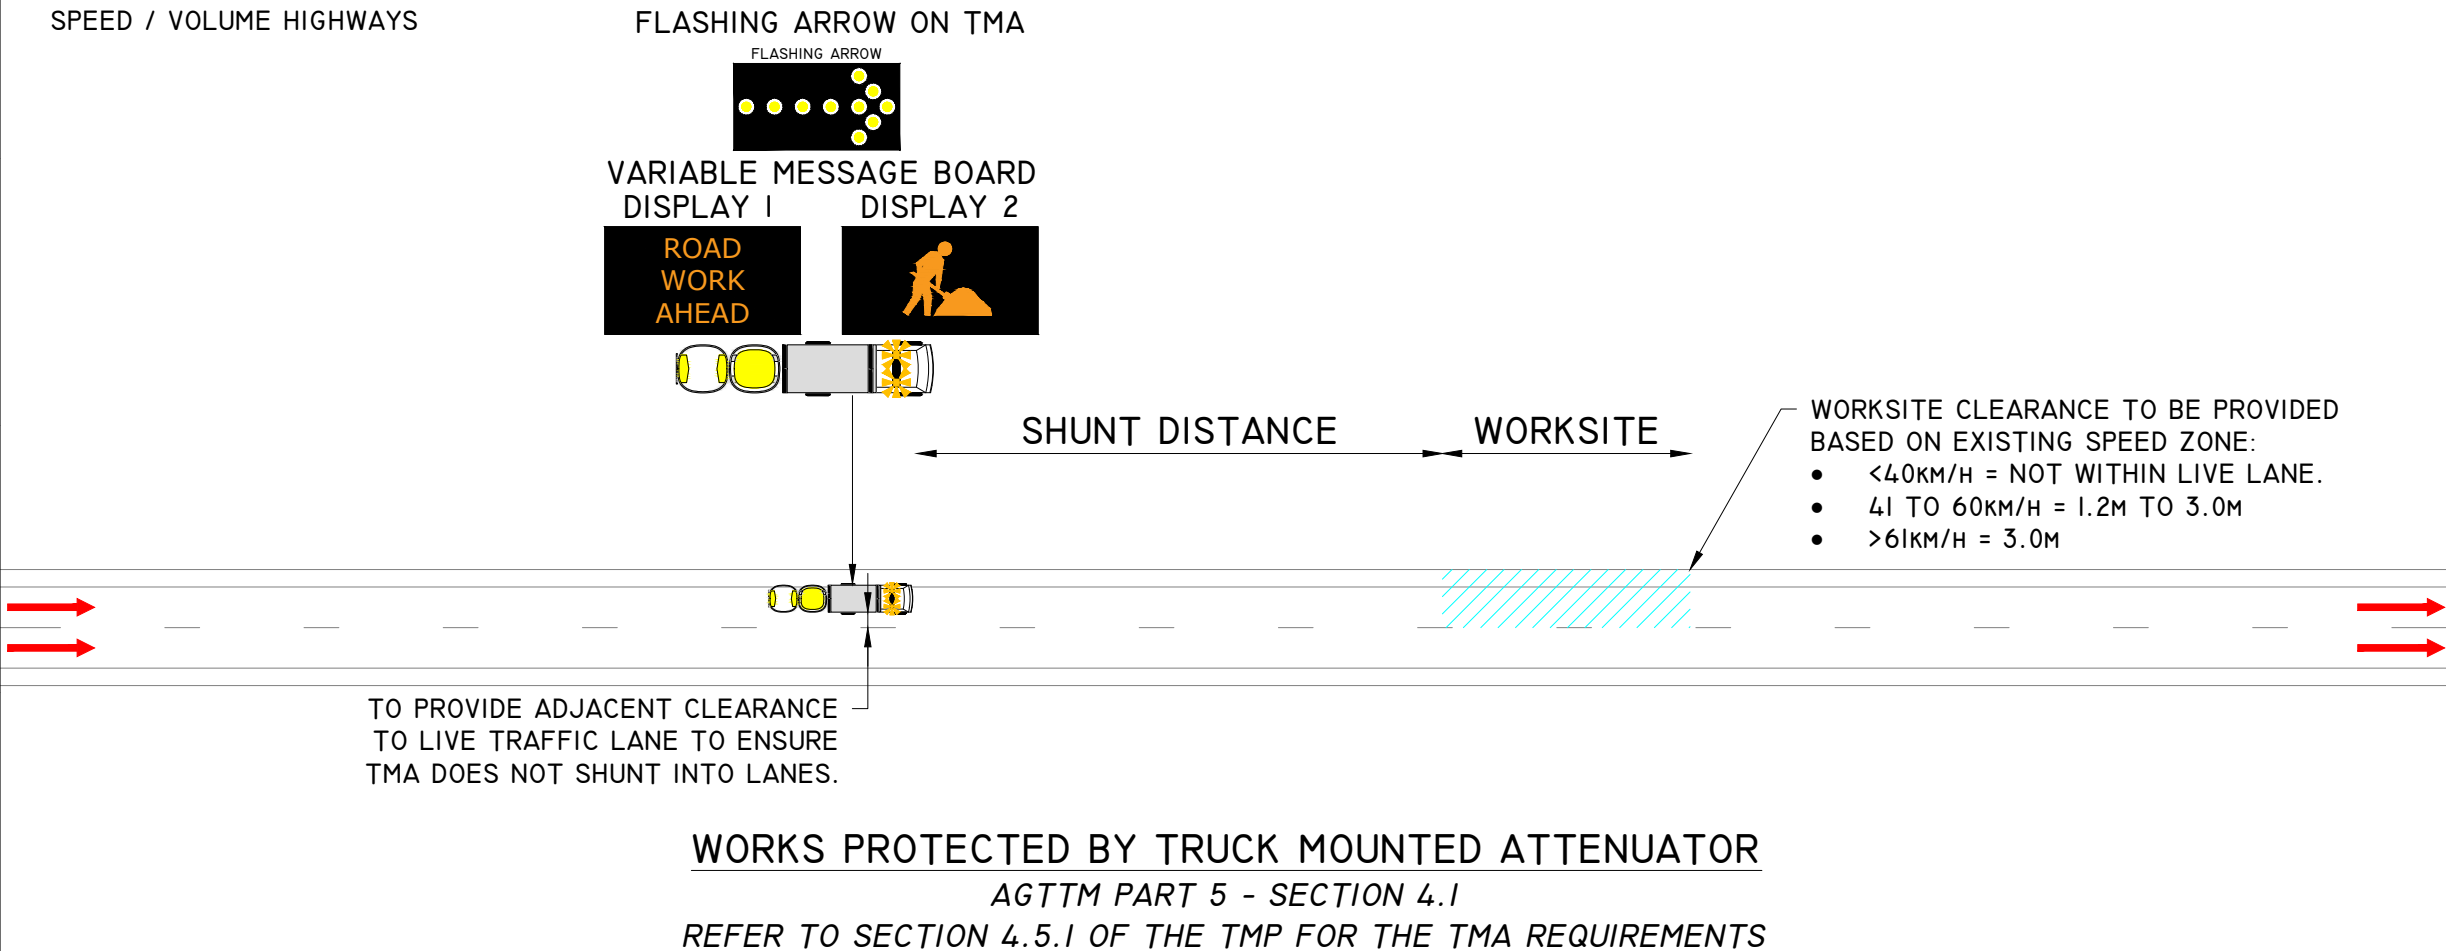

SCENARIO 1:

WORKS PROTECTED BY SHADOW VEHICLE

- A RISK ASSESSMENT MUST BE COMPLETED TO REPLACE ATTENUATOR WITH A SHADOW VEHICLE. SHADOW VEHICLE MUST BE FITTED WITH AN ILLUMINATED FLASHING ARROW.
- NO WORKERS OR PLANT ARE PERMITTED WITHIN THE 20-40M EXCLUSION ZONE BETWEEN SHADOW VEHICLE AND WORKSITE. ENOUGH ROOM IS TO BE ALLOW FOR VEHICLE ROLL FORWARD DURING IMPACT.
- AN ADJACENT CLEARANCE AREA SHOULD BE CONSIDERED BETWEEN SHADOW VEHICLE AND CLOSEST TRAFFIC LANE TO ENSURE IT DOES NOT SHUNT INTO THE LANE. AN ON-SITE RISK ASSESSMENT WILL DETERMINE THE REQUIREMENT AND DISTANCE OF THE ADJACENT CLEARANCE AREA, BASED ON OBSERVATIONS OF VEHICLE PATHS AS THEY PASS THE VEHICLE.
- NOT TO BE USED ON FREEWAYS OR HIGH SPEED / VOLUME ROADS WITHIN THE METROPOLITAN REGION.

SCENARIO 2:

WORKS PROTECTED BY TMA

- REFER TO MRWA CODE OF PRACTICE - REQUIREMENTS FOR THE USE OF TRUCK MOUNTED ATTENUATORS IN WA FOR PROCEDURES ON TRUCK MOUNTED ATTENUATORS.
- REFER TO MANUFACTURING ADVICE FOR SHUNT DISTANCES ON TRUCK MOUNTED ATTENUATORS.
- NO WORKERS OR PLANT ARE PERMITTED WITHIN THE SHUNT DISTANCE ZONE BETWEEN TMA AND WORKSITE.
- TMA MUST BE USED WHERE WORKERS ARE WITHIN 3M OF A LANE FOR LONGER THAN 20 MINUTES OR WITHIN A FREQUENTLY CHANGING WORK AREA ON HIGH SPEED / VOLUME ROADS IN THE METROPOLITAN REGION.
- TMAS SHOULD BE CONSIDERED FOR ALL OTHER SCENARIOS AND ONLY SUBSTITUTED WHERE NECESSARY.

NOTES

- LANE CLOSURES ARE NOT TO BLOCK ON OR OFF RAMP.
- IF A TEMPORARY SPEED ZONE IS REQUIRED FOR WORKER SAFETY, REFER TO TGS-TMC-STLI-002.
- WHERE FITTED, ILLUMINATED FLASHING ARROW SIGNS MUST BE USED TO DIRECT TRAFFIC TO ONE SIDE OF THE VEHICLES WHERE SAFE TO DO SO. IF NOT SAFE, ONLY THE WARNING MODE OF THE ARROWS MUST BE USED.
- ALL VEHICLES MUST BE EQUIPPED WITH A VEHICLE MOUNTED WARNING DEVICE. THE VEHICLE MOUNTED WARNING DEVICE MUST NOT BE OBSCURED AT ANY TIME.
- FOR USE ON MULTI-LANE ROADS WHERE AT LEAST ONE LANE IN THE DIRECTION OF THE WORKS REMAINS OPEN OR WHERE THE SPECIALIST VEHICLE IS CLEAR OF THE TRAFFIC LANES AND WORKS IS ON THE SHOULDER.
- WORKS MUST NOT TAKE LONGER THAN 1 HOUR IN ANY 1 LOCATION.
- REFER TO AGTTM PART 5: SECTION 4.1 WORK PROTECTED BY SPECIALIST VEHICLES FOR MORE DETAILS.

DOCUMENTATION

DAILY RECORDS OF THE SITE LAYOUT INCLUDING DEVICES, SIGHT DISTANCE, RISK ASSESSMENTS, SIGNS OR TGS, MUST BE KEPT IN A DIARY OR IN WORK SHEETS (DAILY DAIRY). ANY SIGNIFICANT DEPARTURES FROM, OR ADDITIONS TO, THE SIGNS AND DEVICES INCLUDED IN THIS DIAGRAM SHOULD BE NOTED AND APPROVED.

LEGEND

- EXISTING ROAD
- WORK ZONE



METROPOLITAN REGIONS
TRAFFIC MANAGEMENT BRANCH
WATERLOO CRESCENT
TELEPHONE (08) 138 138
EAST PERTH 6004

DATE OF DRAWING 2025 JULY	SCALE -
LOCAL GOVERNMENT AUTHORITY -	POSTED SPEED -
ROAD AUTHORITY MRWA	WORKSITE SPEED -
CHECKED BY TYLER HARTLEY	SIGNATURE
ACCREDITATION RTM-0066	
DESIGNED BY MICHAEL REED	SIGNATURE
ACCREDITATION AWTM-23-11536-02	
GENERIC TRAFFIC GUIDANCE SCHEME SHORT TERM LOW IMPACT WORK PROTECTED BY SPECIALIST VEHICLE	
DRAWING NO 0922-01531-STLI-001	REVISION 6