



SCENARIO 1:

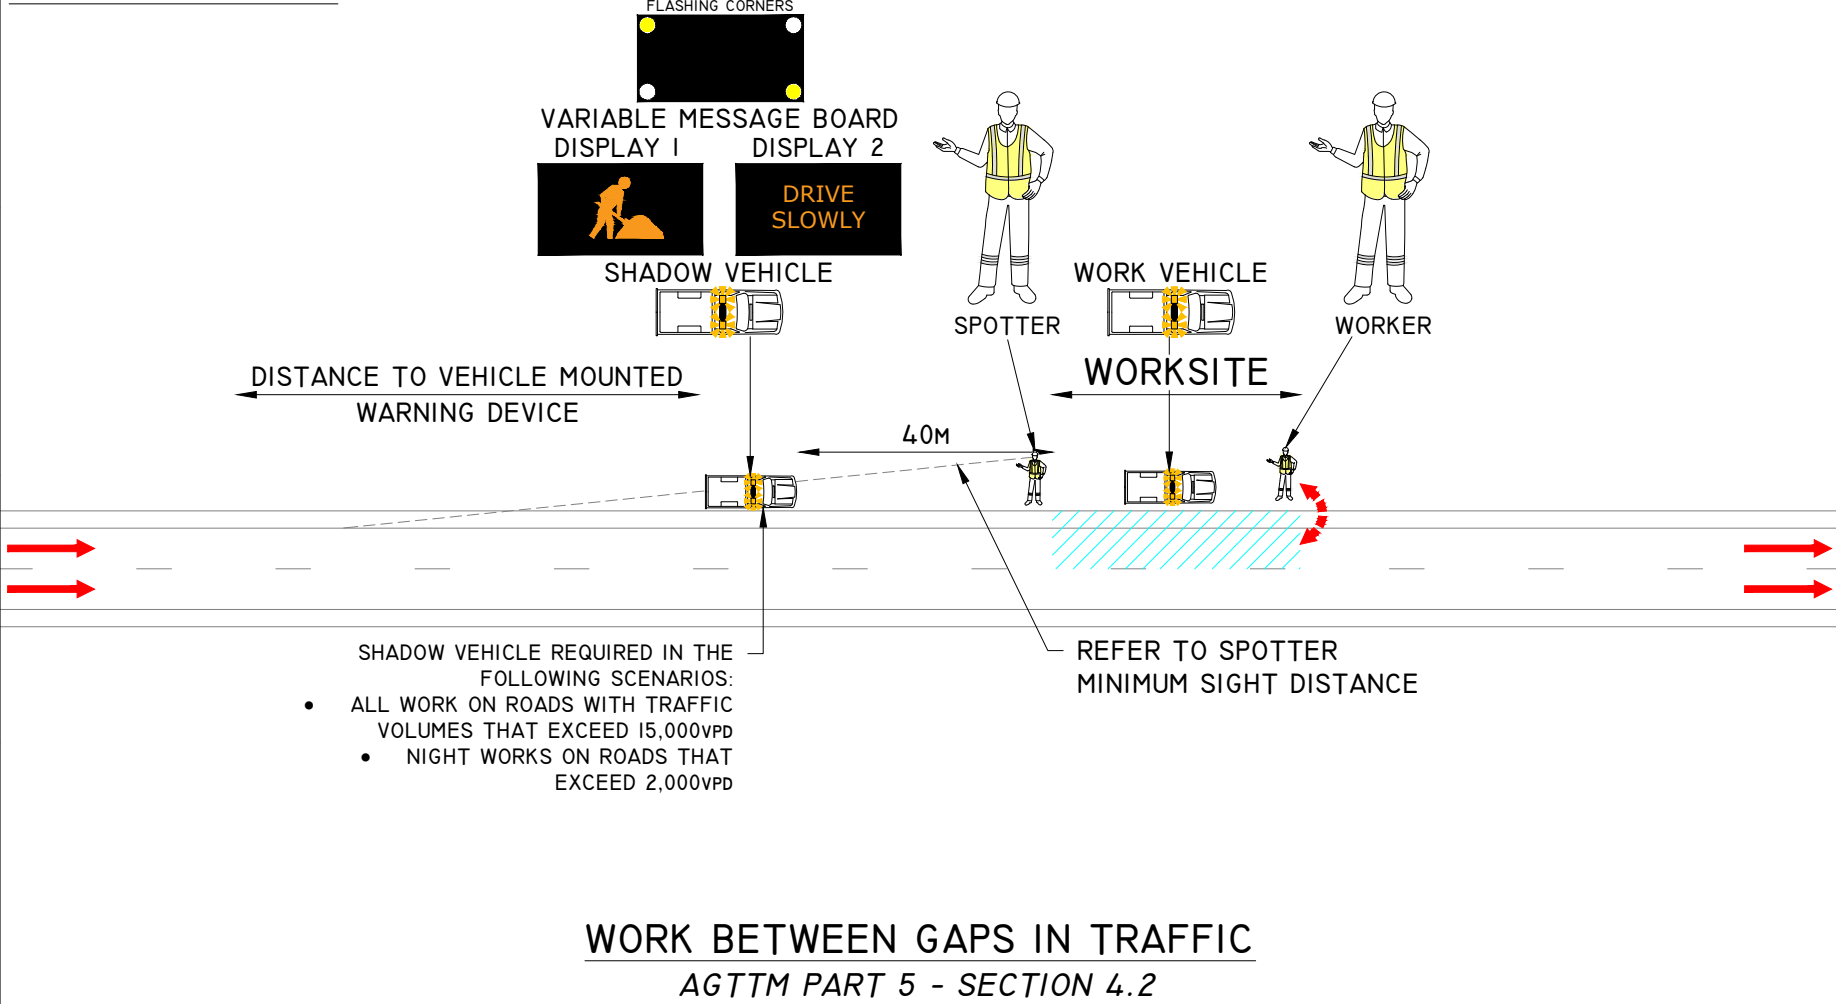

SCENARIO 2:

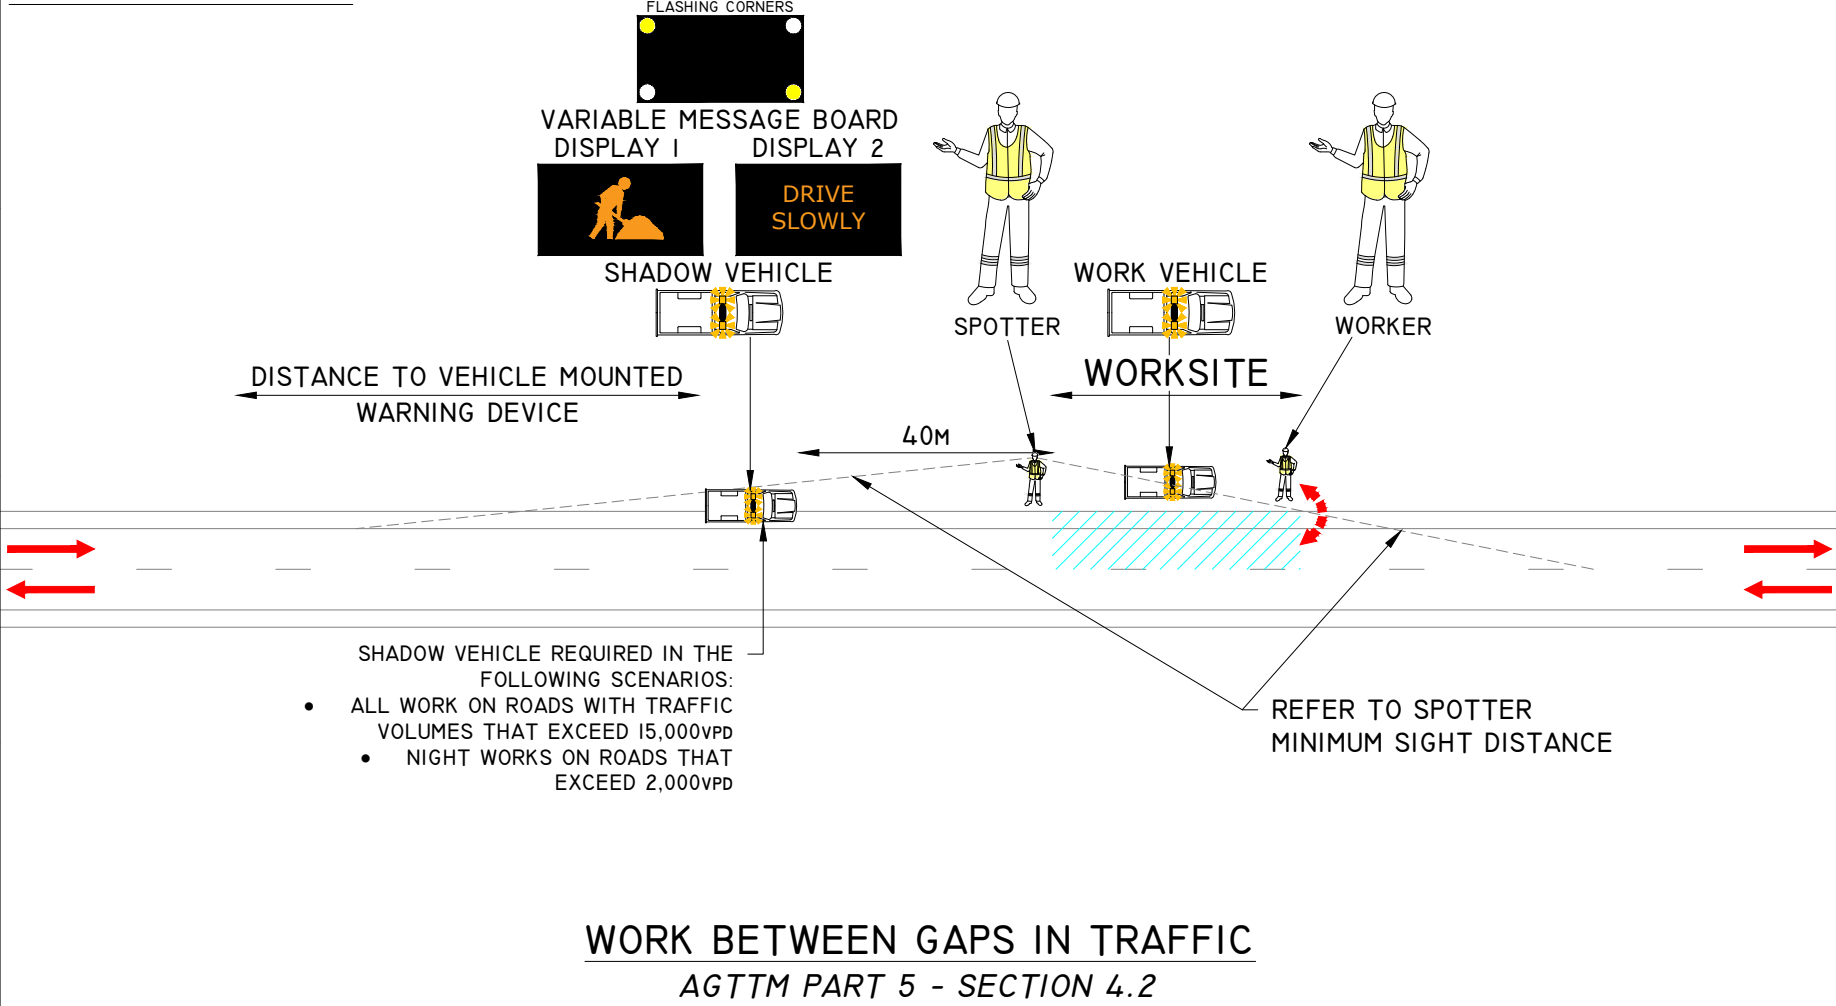

SCENARIO 1:
MULTI-LANE ROAD
SCENARIO 2:
TWO-WAY CARRIAGEWAY
NOTES

1. VEHICLE MUST BE EQUIPPED WITH A VEHICLE MOUNTED WARNING DEVICE.
2. THE VEHICLE MOUNTED WARNING DEVICE SHALL BE MOUNTED AS HIGH AS PRACTICABLE AND NOT BE OBSCURED, E.G BY OVERHANGING VEGETATION OR A RAISED TRUCK BODY.
3. ON HIGH SPEED / VOLUME ROADS, SHADOW VEHICLE MUST BE REPLACED WITH A TMA. A TMA MAY BE USED IN ALL OTHER CIRCUMSTANCE SUBJECT TO A RISK ASSESSMENT.
4. THE FOLLOWING MUST BE ADHERED FOR WORKS IN GAPS IN TRAFFIC:
 - 4.1. THE WORK AREA IS WITHIN A TRAFFIC LANE.
 - 4.2. THE WORKS CAN BE UNDERTAKEN SAFELY WITH ROAD WORKERS ENTERING AND EXITING THE ROAD IN GAPS IN TRAFFIC.
 - 4.3. TRAFFIC IS NOT IMPEDED IN ANY WAY.
 - 4.4. THE ROAD SURFACE CAN REMAIN TRAFFICABLE WITHOUT HAZARD TO TRAFFIC.
 - 4.5. A SPOTTER IS PROVIDED TO WARN WORKERS ON FOOT TO VACATE THE ROADWAY BEFORE THE ARRIVAL OF TRAFFIC WHERE THE SIGHT DISTANCE CANNOT BE MET IN THE MINIMUM SIGHT DISTANCE TO VEHICLE MOUNTED WARNING DEVICE TABLE.*
 - 4.6. A VEHICLE MOUNTED WARNING DEVICE IS DISPLAYED ON THE WORK VEHICLE AND NOT OBSCURED WHEN THE VEHICLE CAN BE PARKED ADJACENT TO THE WORKER LOCATION.
 - 4.7. WORK VEHICLES AND EQUIPMENT ARE PARKED CLEAR OF MOVING TRAFFIC LANE.
- *SPOTTER NOT REQUIRED WHERE THE TASK TAKES 10 SECONDS OR LESS TO COMPLETE AND THE SIGHT DISTANCE OF APPROACHING TRAFFIC TO THE VEHICLE MOUNTED WARNING DEVICE IS A MINIMUM DISTANCE AS SHOWN IN THE MINIMUM SIGHT DISTANCE TO VEHICLE MOUNTED WARNING DEVICE TABLE. THE WORKER MUST BE AWARE OF THE APPROACHING TRAFFIC IF NO SPOTTER IS USED.
5. WORKER ENTERING TRAFFIC IS TO WALK AT A NORMAL PACE AND CONTROLLED MANNER.
6. PRIOR TO COMMENCEMENT OF WORKS, A RISK ASSESSMENT MUST BE UNDERTAKEN TO ENSURE THE WORKS CAN BE COMPLETED SAFELY. REFER TO THE TMP FOR RISK CONSIDERATIONS PRIOR TO SETUP.
7. THE WORKS VEHICLE LOCATION MUST CONSIDER THE IMPACT ON VULNERABLE ROAD USERS AND CYCLISTS. THE WORKER MUST HAVE A CLEAR PATH TO EXIT THE ROAD WHICH IS NOT BLOCKED BY THE WORKS VEHICLE. THE WORK VEHICLE MUST BE LOCATED WITHIN 40M OF THE PROPOSED WORKS.
8. FOR ROADS THAT EXCEED 100VPH PER LANE, THIS SCENARIO CAN ONLY BE USED WHERE SIGNIFICANT GAPS IN TRAFFIC ARE BEING CREATED BY UPSTREAM TRAFFIC CONTROL DEVICES SUCH AS INTERSECTION TRAFFIC SIGNALS.
9. EQUIPMENT OR MATERIALS BROUGHT TO THE SITE MUST BE UNLOADED FROM THE NON-TRAFFIC SIDE OF A STATIONARY WORK VEHICLE, OR THE REAR OF A STATIONARY WORK VEHICLE WITH A SPOTTER OR SHADOW VEHICLE IN PLACE.
10. THE SPOTTER MUST BE WITHIN REASONABLE DISTANCE TO THE WORK LOCATION AT ALL TIMES (WITHIN 40M), TO VIEW AND PROVIDE ADVICE TO THE WORKERS.

DOCUMENTATION

DAILY RECORDS OF THE SITE LAYOUT INCLUDING DEVICES, SIGHT DISTANCE, RISK ASSESSMENTS, SIGNS OR TGS, MUST BE KEPT IN A DIARY OR IN WORK SHEETS (DAILY DAIRY). ANY SIGNIFICANT DEPARTURES FROM, OR ADDITIONS TO, THE SIGNS AND DEVICES INCLUDED IN THIS DIAGRAM SHOULD BE NOTED AND APPROVED.

TABLES

MINIMUM SIGHT DISTANCE TO VEHICLE MOUNTED WARNING DEVICE - NO SPOTTER
AGTTM PART 5 - TABLE 4.2

SPEED LIMIT (km/h)	DISTANCE (m)
≤45	225
46-55	275
56-65	335
66-75	390
76-85	445
86-95	500
96-110	555
>110	SPOTTER REQUIRED

WORK TASK ≤ 10 SECONDS. WORKER TO FACE ONCOMING TRAFFIC.

SPOTTER MINIMUM SIGHT DISTANCE
AGTTM PART 5 - TABLE 4.3

SPEED LIMIT (km/h)	DISTANCE (m)
≤45	80
46-55	100
56-65	120
66-75	140
76-85	160
86-95	180
96-105	200
>106	220

DISTANCES ARE FOR WORKER ON FOOT TO VACATE ROADWAY AT A MAX TRAVEL DISTANCE OF 3.5M

LEGEND

- EXISTING ROAD
- WORK ZONE



METROPOLITAN REGIONS
TRAFFIC MANAGEMENT BRANCH
WATERLOO CRESCENT
TELEPHONE (08) 138 138
EAST PERTH 6004

DATE OF DRAWING 2025 JULY	SCALE -
LOCAL GOVERNMENT AUTHORITY -	POSTED SPEED -
ROAD AUTHORITY MRWA	WORKSITE SPEED -
CHECKED BY TYLER HARTLEY	SIGNATURE <i>Tyler Hartley</i>
ACCREDITATION RTM-0066	
DESIGNED BY MICHAEL REED	SIGNATURE <i>Michael Reed</i>
ACCREDITATION AWTM-23-11536-02	

GENERIC TRAFFIC GUIDANCE SCHEME
SHORT TERM LOW IMPACT
WORK BETWEEN GAPS IN TRAFFIC
IN LIVE TRAFFIC LANE

DRAWING NO 0922-01531-STLI-003	REVISION 6
-----------------------------------	---------------