



SCENARIO 1:

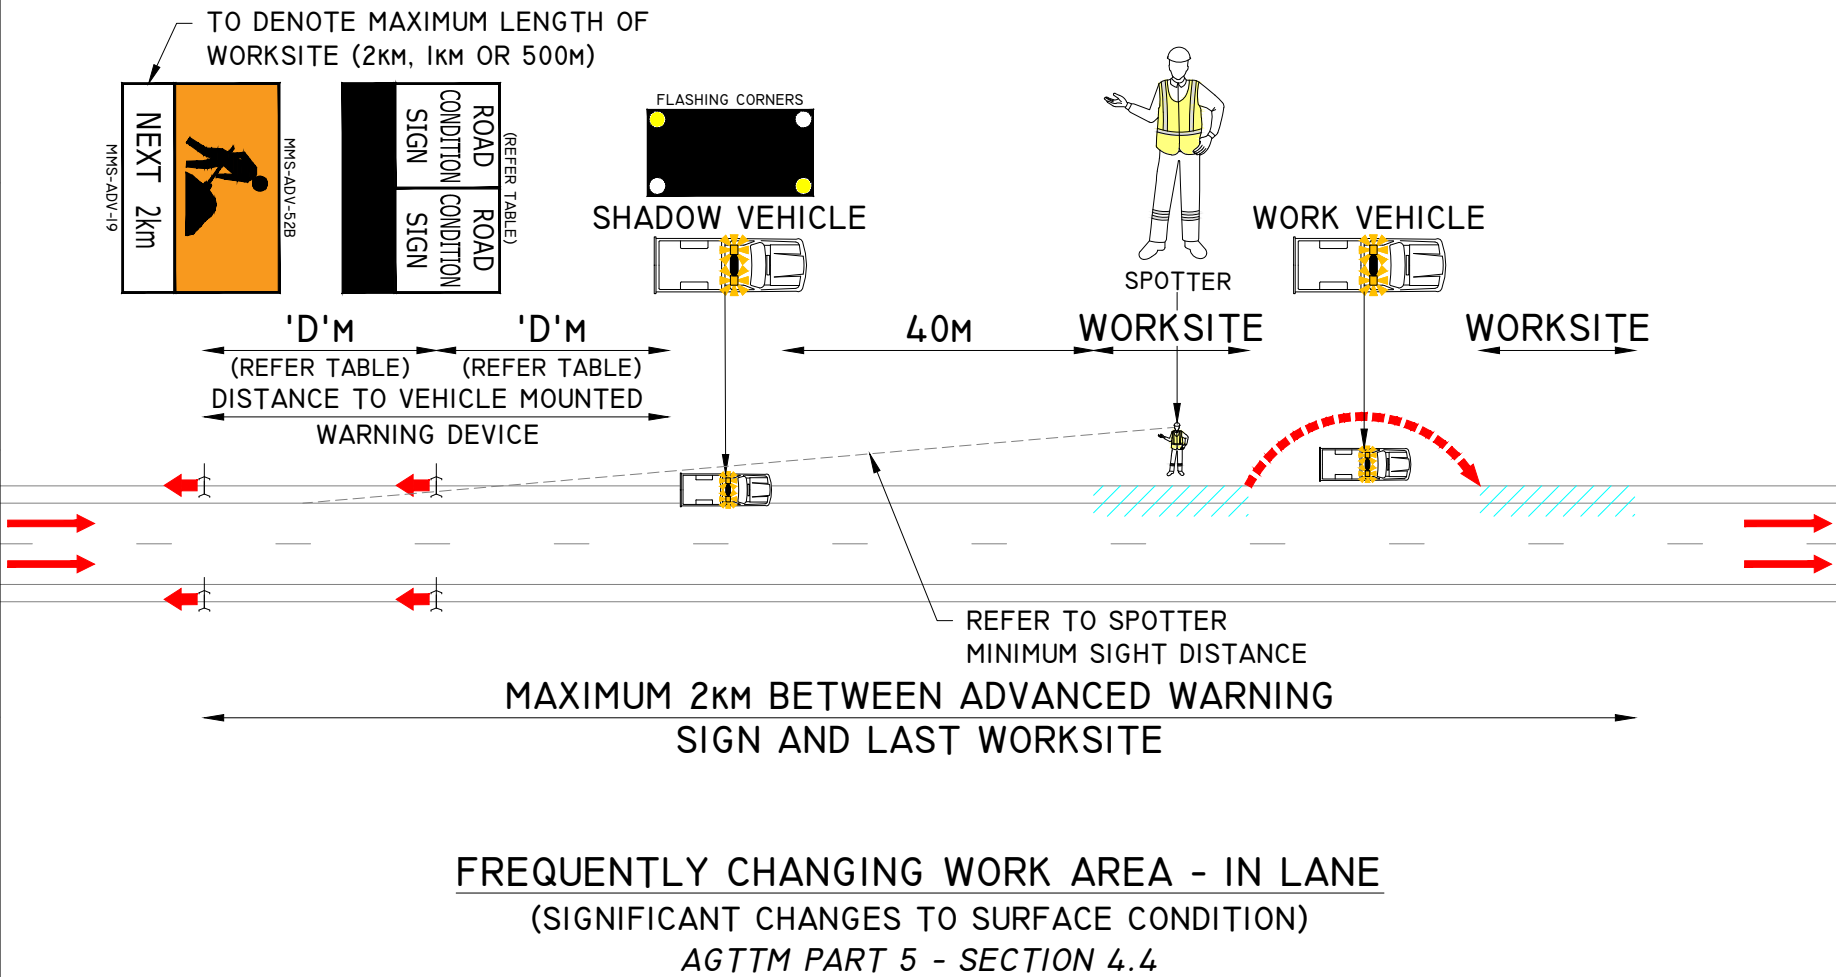

SCENARIO 2:

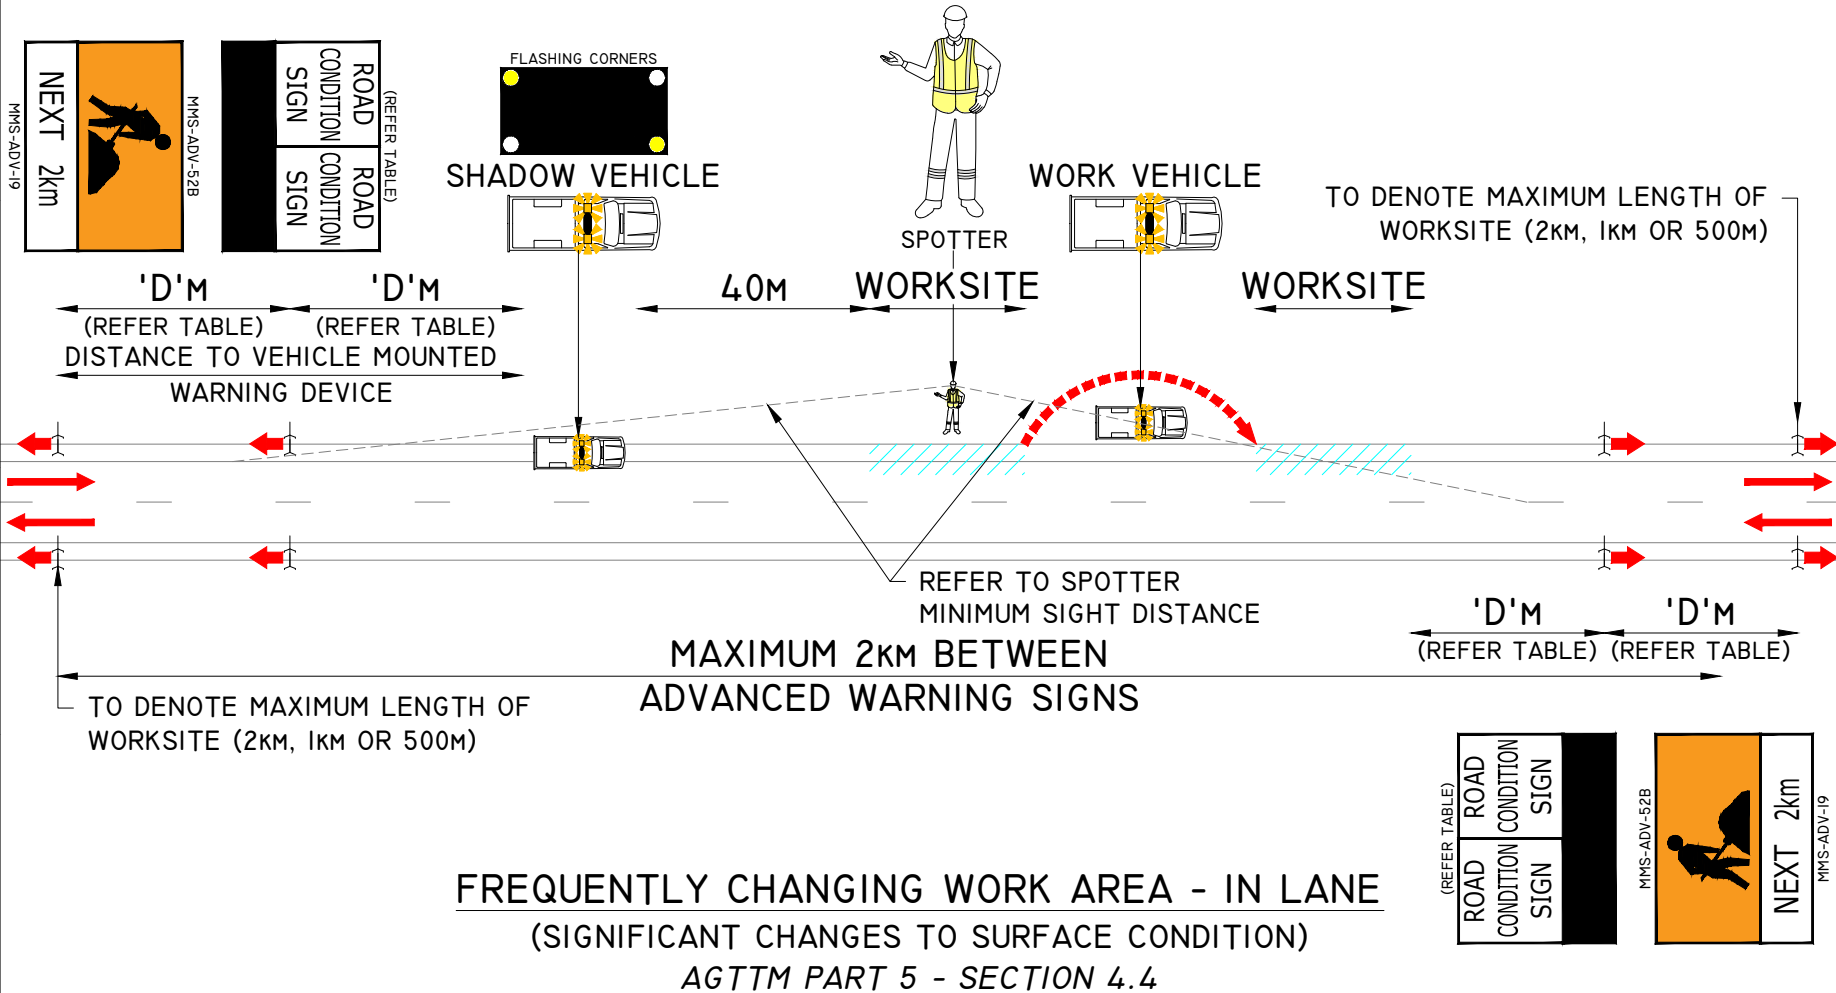

SCENARIO 1:

MULTI-LANE ROAD (WORKERS ON FOOT)

SCENARIO 2:

TWO-WAY CARRIAGEWAY (WORKERS ON FOOT)

NOTES

- ON HIGH SPEED / VOLUME ROADS, SHADOW VEHICLE MUST BE REPLACED WITH A TMA. A TMA MAY BE USED IN ALL OTHER CIRCUMSTANCE SUBJECT TO A RISK ASSESSMENT.
- VEHICLES MUST BE EQUIPPED WITH A VEHICLE MOUNTED WARNING DEVICE.
- THE VEHICLE MOUNTED WARNING DEVICE SHALL BE MOUNTED AS HIGH AS PRACTICABLE AND NOT BE OBSCURED, E.G BY OVERHANGING VEGETATION OR A RAISED TRUCK BODY.
- AS THE WORKS PROGRESS ALONG THE ROAD, THE SHADOW VEHICLE, WORK VEHICLE AND SPOTTER MOVES WITH THE WORKERS.
- THE FOLLOWING MUST BE ADHERED FOR FREQUENTLY CHANGING WORK AREA:
 - WORKS MOVE FREQUENTLY BETWEEN SUCCESSIVE LOCATIONS.
 - A SPOTTER IS AVAILABLE TO WARN WORKERS ON FOOT TO VACATE THE ROADWAY BEFORE THE ARRIVAL OF APPROACHING TRAFFIC.
 - A SHADOW VEHICLE IS AVAILABLE (TMA FOR HIGH SPEED / VOLUME ROADS).
 - THERE IS A MINIMUM SIGHT DISTANCE FROM APPROACHING ROAD USERS TO THE SHADOW AND THE WORK VEHICLE MOUNTED WARNING DEVICE OF:
 - 150M IF THE SPEED IS 60KM/H OR LESS.
 - 250M IF THE SPEED IS MORE THAN 60KM/H.
 - WORKS DO NOT REDUCE THE OVERALL WIDTH TO LESS THAN THE REQUIREMENTS FOR SAFE PASSAGE OF TWO WAY TRAFFIC FLOW, OR ONE WAY TRAFFIC IF THE VOLUME IS LESS THAN 50VPD.
 - WORKS DO NO REDUCE ANY TRAFFIC LANE WIDTH ADJACENT TO A BARRIER LINE TO LESS THAN THAT NEEDED TO ALLOW VEHICLES TO PROCEED WITHOUT CROSSING THE LINE.
 - THE MAXIMUM WORK PERIOD AT ANY ONE LOCATION IS AS PER THE BELOW:

IN TRAFFIC OR WITHIN 1.2M OF TRAFFIC:

 - 5 MIN WHERE TRAFFIC VOLUME IS ABOVE 40VPD.
 - 1 HOUR WHERE TRAFFIC VOLUMES IS 40VPD OR LESS.

BETWEEN 1.2M AND 3M OF TRAFFIC:


 - 20 MIN WHERE TRAFFIC VOLUMES IS ABOVE 40VPD.
 - 1 HOUR WHERE TRAFFIC VOLUMES IS 40VPD OR LESS.
- FOR SCENARIOS WHERE THERE ARE NO WORKERS ON FOOT, REFER TO TGC-TMC-STLI-006 OR 008. FOR SCENARIOS WHERE THERE ARE NO SIGNIFICANT CHANGES TO THE SURFACE CONDITION OCCUR REFER TO TGS-TMC-STLI-005.
- PRIOR TO EQUIPMENT OR MATERIALS BEING BROUGHT INTO THE WORK AREA, A DRIVE THROUGH CHECK OF THE WORKSITE TRAFFIC MANAGEMENT SETUP SHOULD BE MADE IN ALL DIRECTIONS, INCLUDING SIDE ROADS.
- PRIOR TO COMMENCEMENT OF WORKS, A RISK ASSESSMENT MUST BE UNDERTAKEN TO ENSURE THE WORKS CAN BE COMPLETED SAFELY. REFER TO THE TMP FOR RISK CONSIDERATIONS PRIOR TO SETUP.
- THE WORKS AND SHADOW VEHICLE LOCATION MUST CONSIDER THE IMPACT ON VULNERABLE ROAD USERS AND CYCLISTS. THE WORK VEHICLE MUST BE LOCATED WITHIN 40M OF THE PROPOSED WORKS. EQUIPMENT OR MATERIALS BROUGHT TO THE SITE MUST BE UNLOADED FROM THE NON-TRAFFIC SIDE OF A STATIONARY WORK VEHICLE, OR THE REAR OF A STATIONARY WORK VEHICLE WITH A SPOTTER OR SHADOW VEHICLE IN PLACE.
- THE SPOTTER MUST BE WITHIN REASONABLE DISTANCE TO THE WORK LOCATION AT ALL TIMES (WITHIN 40M), TO VIEW AND PROVIDE ADVICE TO THE WORKERS. SPOTTER TO ENSURE THAT SHADOW OR WORK VEHICLE DOES NOT IMPACT ON REQUIRED SIGHT DISTANCE.

DOCUMENTATION

DAILY RECORDS OF THE SITE LAYOUT INCLUDING DEVICES, SIGHT DISTANCE, RISK ASSESSMENTS, SIGNS OR TGS, MUST BE KEPT IN A DIARY OR IN WORK SHEETS (DAILY DAIRY). ANY SIGNIFICANT DEPARTURES FROM, OR ADDITIONS TO, THE SIGNS AND DEVICES INCLUDED IN THIS DIAGRAM SHOULD BE NOTED AND APPROVED.

ROAD CONDITION SIGNS

PLACEMENT ON EITHER SIDE OF FRAME

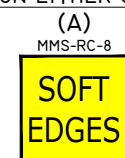

RIGHT SIDE OF FRAME ONLY		LEFT SIDE OF FRAME ONLY	
(B) MMS-RC-1	(C) MMS-RC-6	(D) MMS-RC-2	(E) MMS-RC-5

TABLES

SIGN SPACING

AGTTM PART 3 - TABLE 2.2

SPEED LIMIT (KM/H)	DISTANCE ('D') (M)
55 OR LESS	15
56 TO 65	45
GREATER THAN 65	EQUAL TO SPEED OF TRAFFIC IN KM/H

MINIMUM SIGHT DISTANCE TO VEHICLE MOUNTED WARNING DEVICE - NO SPOTTER

AGTTM PART 5 - TABLE 4.2

SPEED LIMIT (KM/H)	DISTANCE (M)
≤45	225
46-55	275
56-65	335
66-75	390
76-85	445
86-95	500
96-110	555
>110	SPOTTER REQUIRED

WORK TASK ≤ 10 SECONDS. WORKER TO FACE ONCOMING TRAFFIC.

SPOTTER MINIMUM SIGHT DISTANCE

AGTTM PART 5 - TABLE 4.8

SPEED LIMIT (KM/H)	DISTANCE (M)
≤45	80
46-55	100
56-65	120
66-75	140
76-85	160
86-95	180
96-105	200
>106	220

DISTANCES ARE FOR WORKER ON FOOT TO VACATE ROADWAY AT A MAX TRAVEL DISTANCE OF 3.5M

LEGEND

- EXISTING ROAD
- WORK ZONE



METROPOLITAN REGIONS
TRAFFIC MANAGEMENT BRANCH

WATERLOO CRESCENT
TELEPHONE (08) 138 138

EAST PERTH 6004

DATE OF DRAWING 2025 JULY	SCALE -
LOCAL GOVERNMENT AUTHORITY -	POSTED SPEED -
ROAD AUTHORITY MRWA	WORKSITE SPEED -
CHECKED BY TYLER HARTLEY	SIGNATURE
ACCREDITATION RTM-0066	SIGNATURE
DESIGNED BY MICHAEL REED	
ACCREDITATION AWTM-23-11536-02	
GENERIC TRAFFIC GUIDANCE SCHEME SHORT TERM LOW IMPACT FREQUENTLY CHANGING WORK AREA IN LIVE TRAFFIC LANE	
DRAWING NO 0922-01531-STLI-007	REVISION 6