



SCENARIO 1:

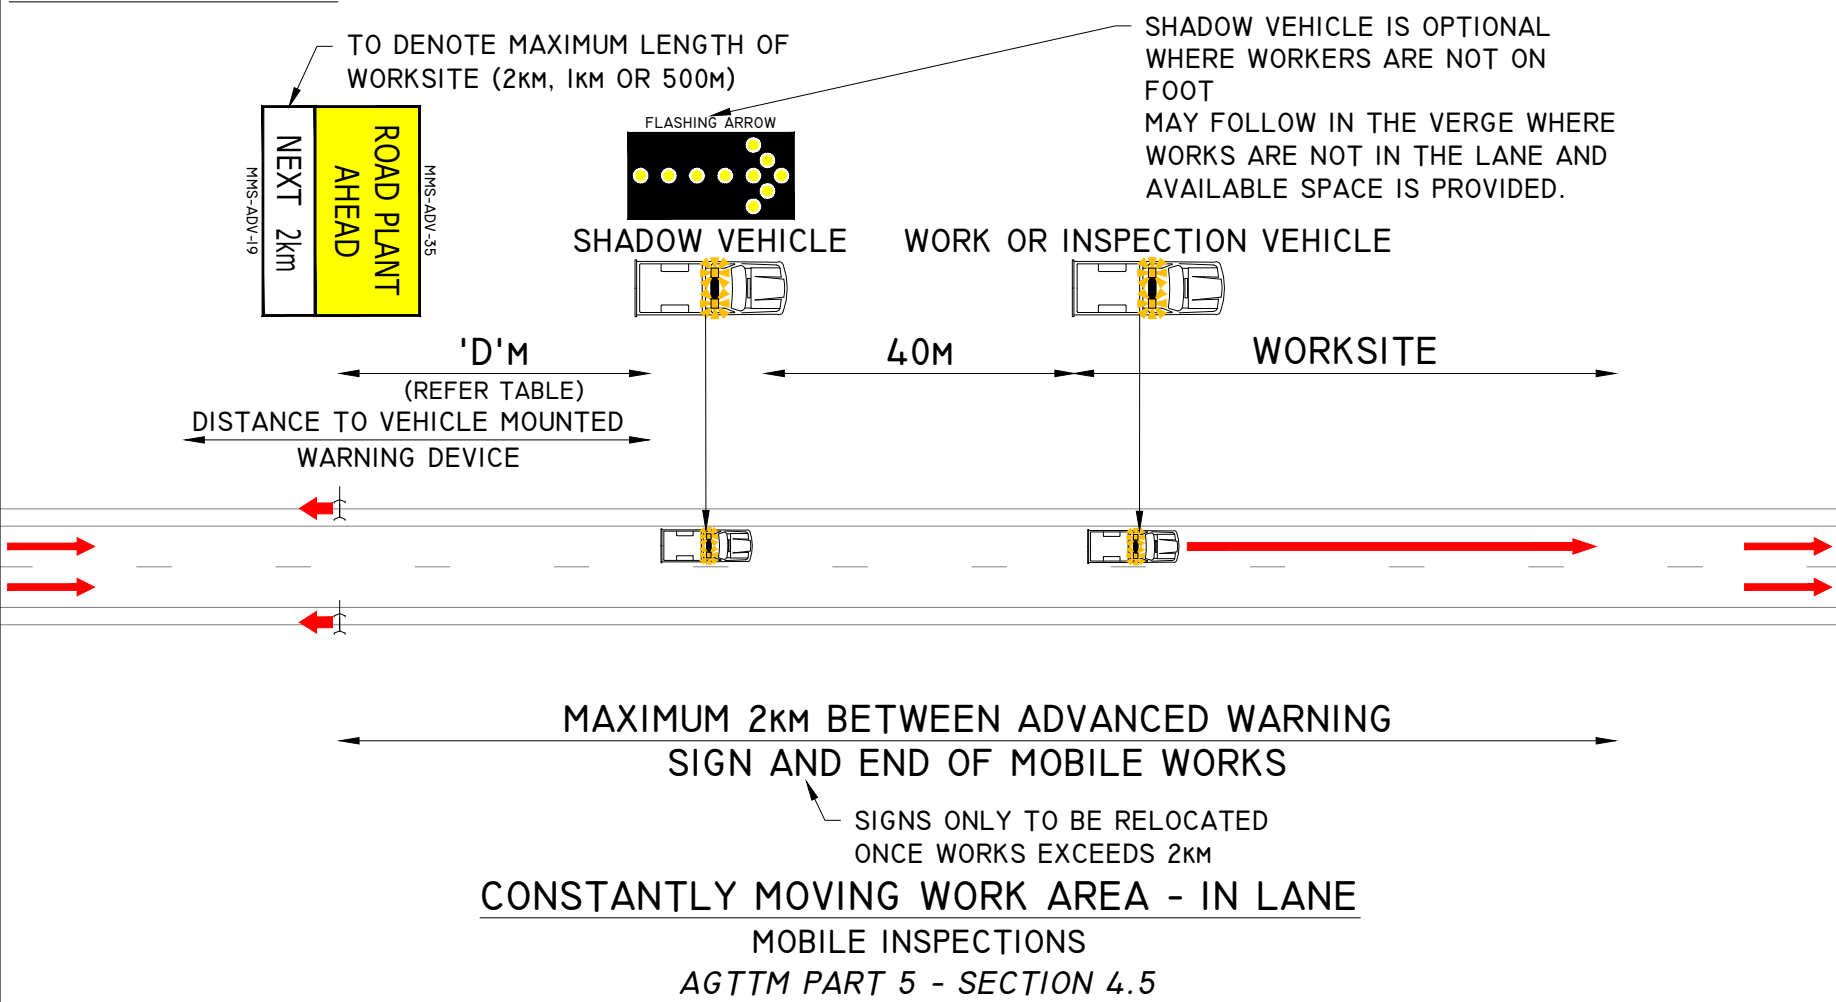

SCENARIO 2:

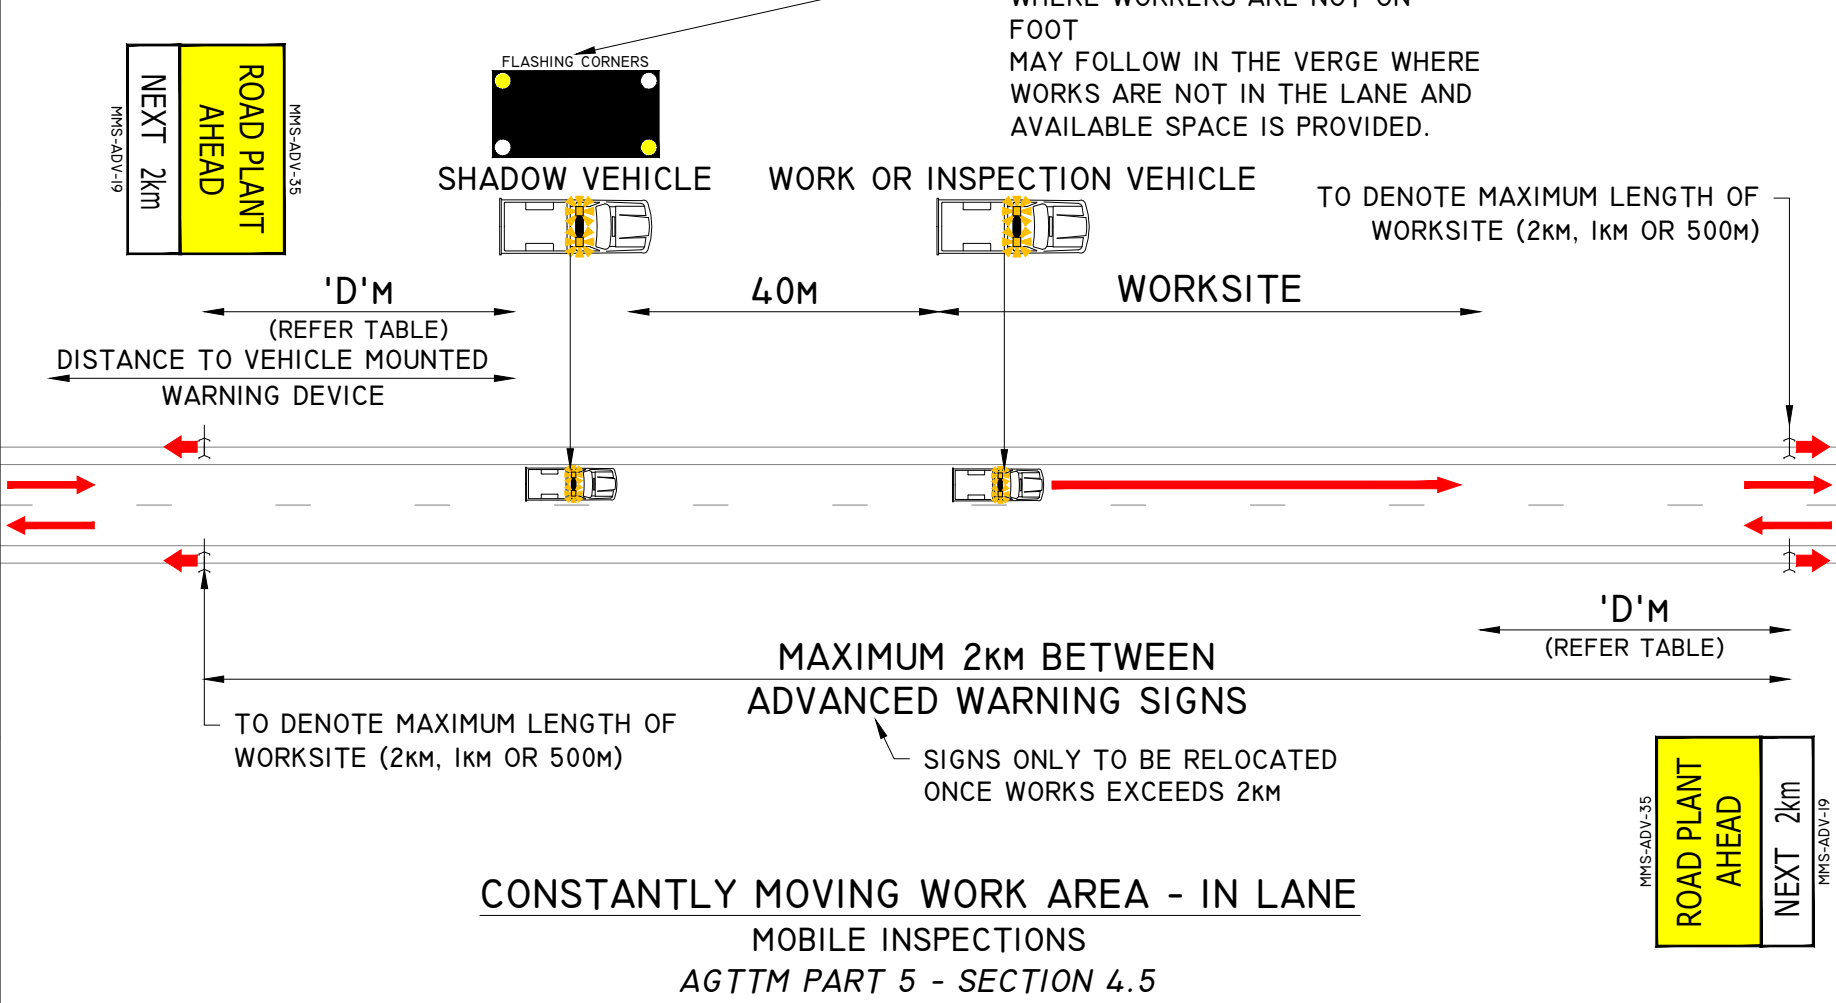

SCENARIO 1:
MULTI-LANE ROAD
SCENARIO 2:
TWO-WAY CARRIAGEWAY
NOTES

- ON HIGH SPEED / VOLUME ROADS, SHADOW VEHICLE MUST BE REPLACED WITH A TMA. A TMA MAY BE USED IN ALL OTHER CIRCUMSTANCE SUBJECT TO A RISK ASSESSMENT.
- VEHICLES MUST BE EQUIPPED WITH A VEHICLE MOUNTED WARNING DEVICE.
- THE VEHICLE MOUNTED WARNING DEVICE SHALL BE MOUNTED AS HIGH AS PRACTICABLE AND NOT BE OBSCURED, E.G BY OVERHANGING VEGETATION OR A RAISED TRUCK BODY.
- AS THE WORKS PROGRESS ALONG THE ROAD, THE SHADOW VEHICLE MOVES WITH THE WORK VEHICLE.
- THE FOLLOWING MUST BE ADHERED FOR CONSTANTLY MOVING WORK AREA:
 - THE INSPECTION VEHICLE IS EITHER FULLY OR PARTIALLY WITHIN A TRAFFIC LANE.
 - THE WORKS AREA MUST BE CONTINUALLY MOVING.
 - THE MOBILE ROAD INSPECTION IS CARRIED OUT PROVIDING THE VEHICLE MAINTAINS SPEED:
 - LESS THAN 20km/h BELOW THE SPEED LIMIT OR
 - ON A ROAD WITH LESS THAN 200vpa IS AT LEAST 25km/h
- FOR GRADING SCENARIOS REFER TO TGS-TMC-STLI-010 OR 011.
- PRIOR TO COMMENCEMENT OF WORKS, A RISK ASSESSMENT MUST BE UNDERTAKEN TO ENSURE THE WORKS CAN BE COMPLETED SAFELY. REFER TO THE TMP FOR RISK CONSIDERATIONS PRIOR TO SETUP.
- THE WORKS AND SHADOW VEHICLE LOCATION MUST CONSIDER THE IMPACT ON VULNERABLE ROAD USERS AND CYCLISTS.
- ADVANCED WARNING SIGNS MAY BE OMITTED FOR A SECTION WHEN:
 - THE SIGHT DISTANCE FOR THE ENTIRE SECTION EXCEEDS 150M WHEN THE SPEED IS 60km/h OR LESS AND A VEHICLE MOUNTED WARNING DEVICE IS DISPLAYED.
 - THE SIGHT DISTANCE FOR THE ENTIRE SECTION EXCEED 250M WHEN THE SPEED IS MORE THAN 60km/h AND A VEHICLE MOUNTED WARNING DEVICE IS DISPLAYED.
- A SPOTTER MUST BE USED FOR THE INSTALLATION OF SIGNAGE. REFER TO THE SPOTTER MINIMUM SIGHT DISTANCE TABLES.

DOCUMENTATION

DAILY RECORDS OF THE SITE LAYOUT INCLUDING DEVICES, SIGHT DISTANCE, RISK ASSESSMENTS, SIGNS OR TGS, MUST BE KEPT IN A DIARY OR IN WORK SHEETS (DAILY DAIRY). ANY SIGNIFICANT DEPARTURES FROM, OR ADDITIONS TO, THE SIGNS AND DEVICES INCLUDED IN THIS DIAGRAM SHOULD BE NOTED AND APPROVED.

TABLES

SIGN SPACING

AGTTM PART 3 - TABLE 2.2

SPEED LIMIT (KM/H)	DISTANCE ('D') (M)
55 OR LESS	15
56 TO 65	45
GREATER THAN 65	EQUAL TO SPEED OF TRAFFIC IN KM/H

MINIMUM SIGHT DISTANCE TO VEHICLE MOUNTED WARNING DEVICE - NO SPOTTER
AGTTM PART 5 - TABLE 4.2

SPEED LIMIT (KM/H)	DISTANCE (M)
≤45	225
46-55	275
56-65	335
66-75	390
76-85	445
86-95	500
96-110	555
>110	SPOTTER REQUIRED

WORK TASK ≤ 10 SECONDS. WORKER TO FACE ONCOMING TRAFFIC.

LEGEND

EXISTING ROAD



METROPOLITAN REGIONS
TRAFFIC MANAGEMENT BRANCH
WATERLOO CRESCENT
TELEPHONE (08) 138 138
EAST PERTH 6004

DATE OF DRAWING 2025 JULY	SCALE -
LOCAL GOVERNMENT AUTHORITY -	POSTED SPEED -
ROAD AUTHORITY MRWA	WORKSITE SPEED -
CHECKED BY TYLER HARTLEY	SIGNATURE Tyler Hartley
ACCREDITATION RTM-0066	
DESIGNED BY MICHAEL REED	SIGNATURE Michael Reed
ACCREDITATION AWTM-23-11536-02	

GENERIC TRAFFIC GUIDANCE SCHEME
SHORT TERM LOW IMPACT
CONSTANTLY MOVING WORK AREA
IN LIVE TRAFFIC LANE

DRAWING NO 0922-01531-STLI-009	REVISION 6
-----------------------------------	---------------