
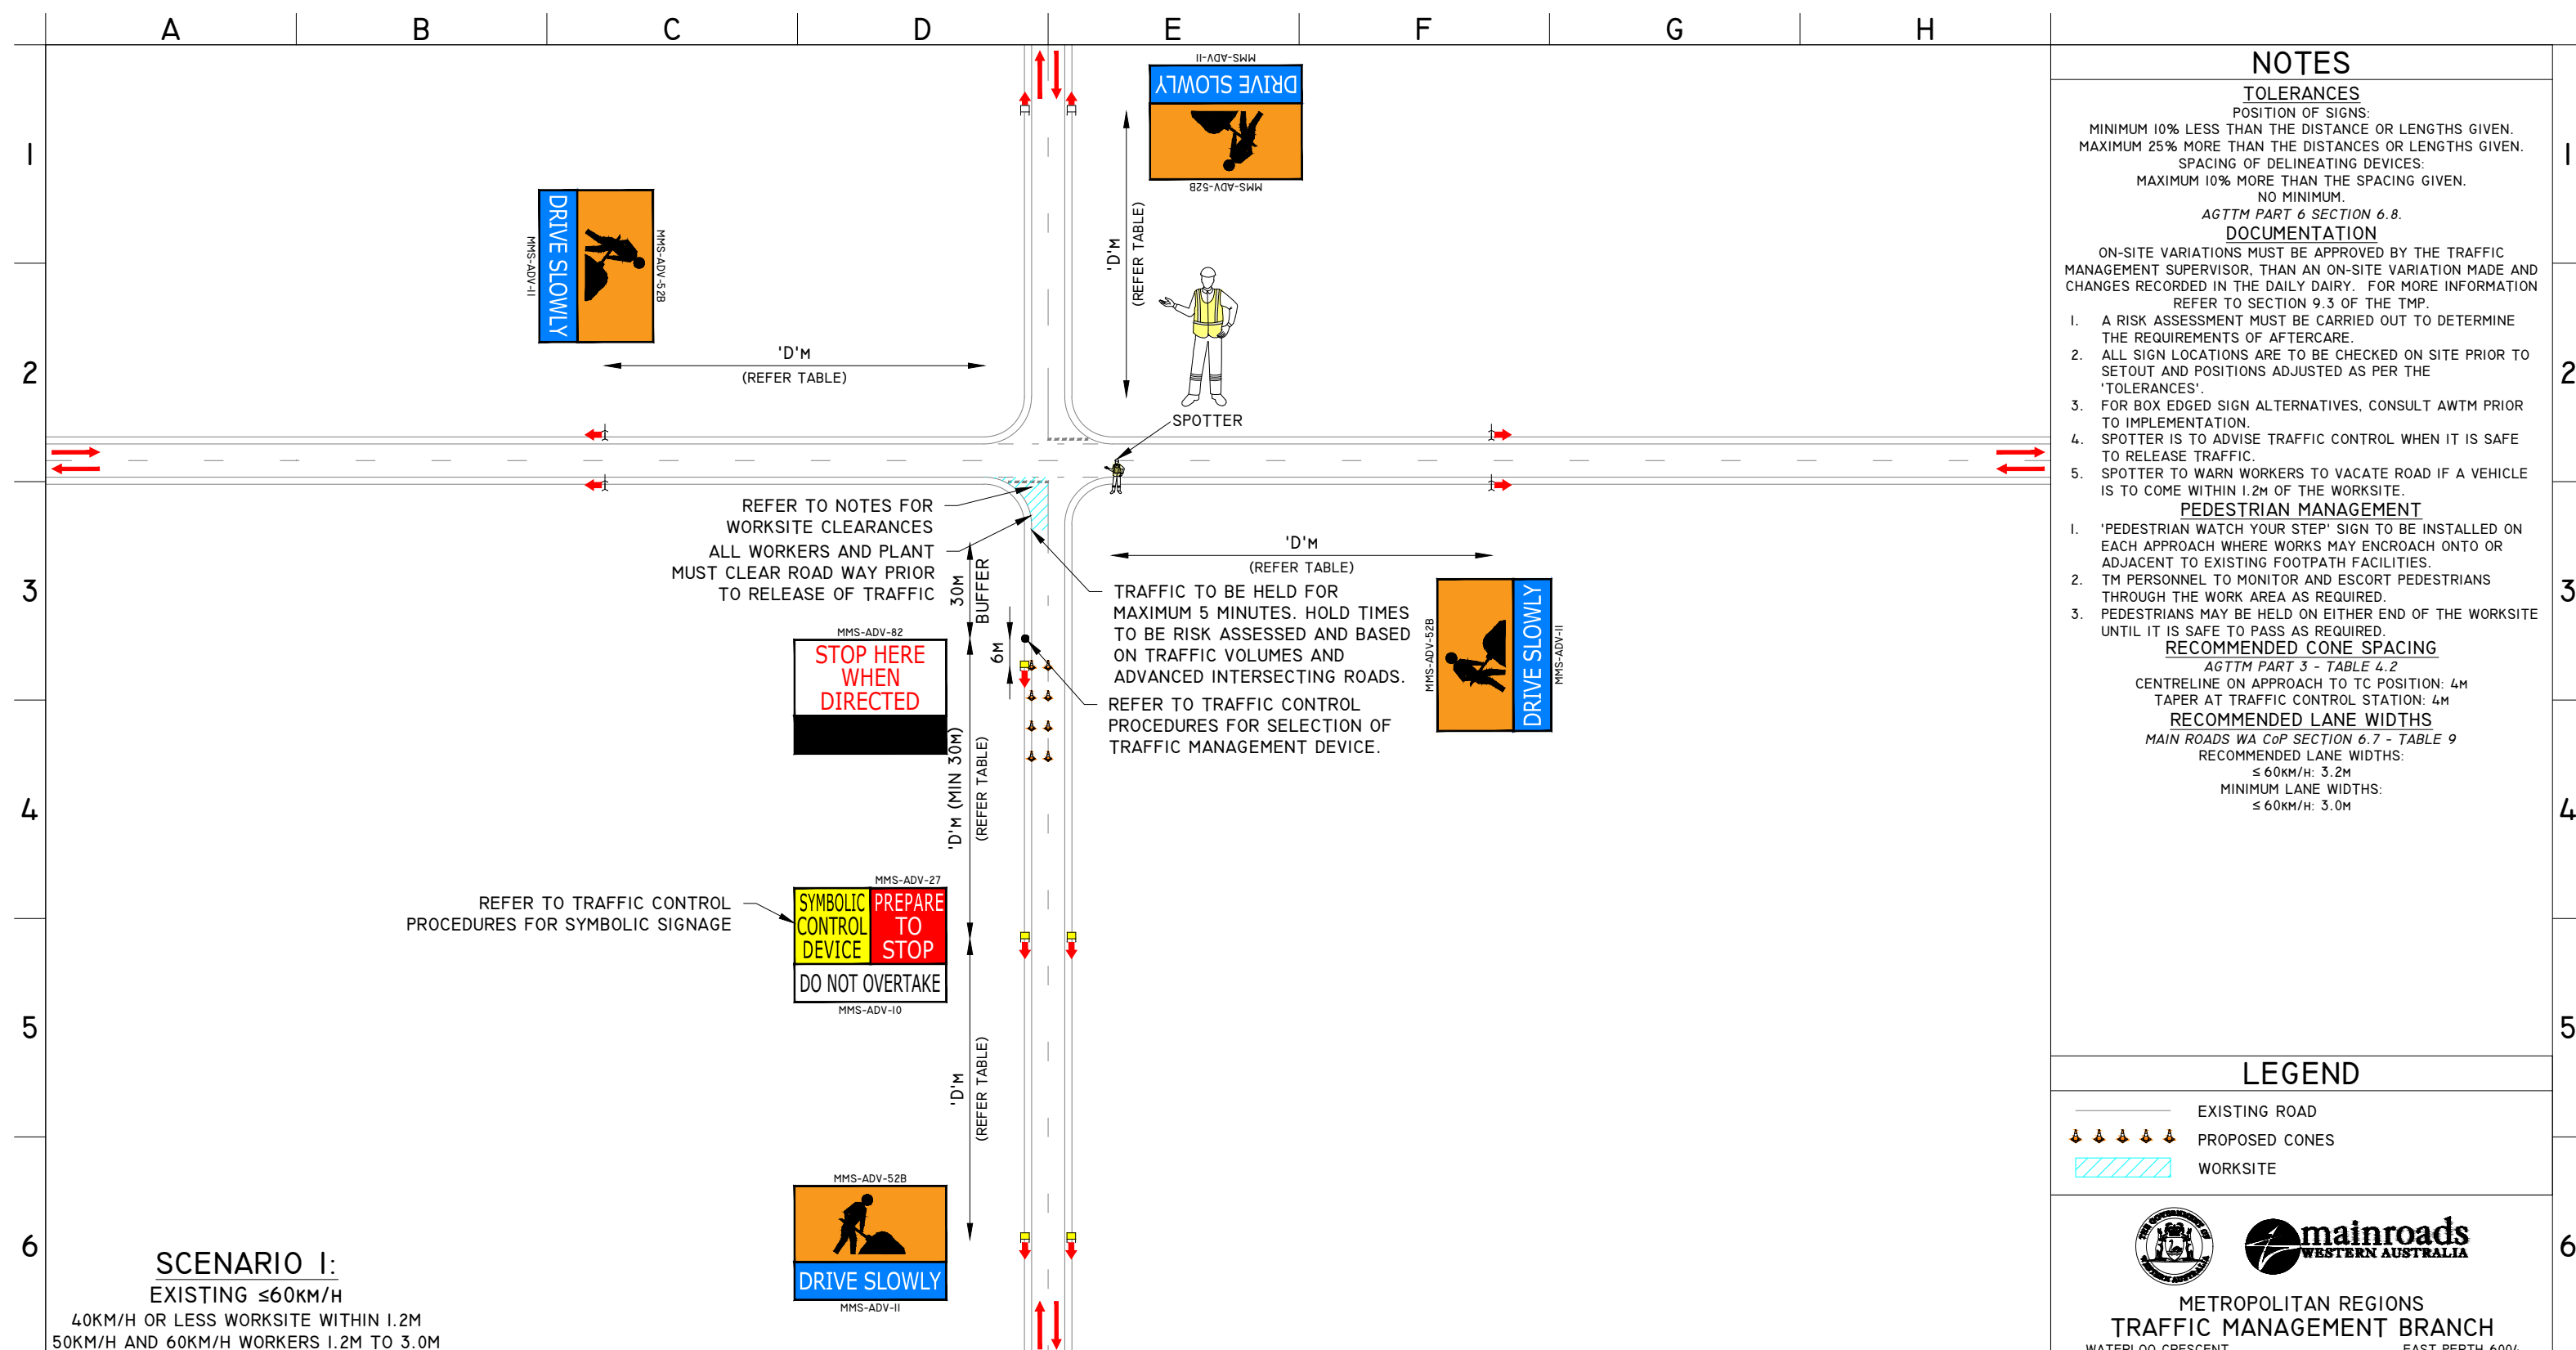
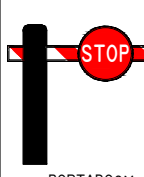


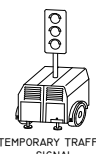

7	TRAFFIC CONTROL PROCEDURES REFER TO TMP SECTION 4.1.7 PORTABLE TRAFFIC CONTROL DEVICES FOR MORE DETAILS		MANUAL TRAFFIC CONTROL IS NOT PERMITTED ON THE MAIN ROADS NETWORK WITH THE EXCEPTIONS LISTED UNDER SECTION 4.1.7 (PORTABLE TRAFFIC CONTROL DEVICES) OF THE TMP AND IN THE MAIN ROADS CODE OF PRACTICE. ON ALL OTHER ROADS, PTCDS MUST BE USED UNDER THE FOLLOWING CONDITIONS: • A PERMANENT SPEED LIMIT OF 90m/h OR MORE AND OVER 2,000vpd; OR • A PERMANENT SPEED LIMIT OF 80km/h OR MORE AND OVER 10,000vpd. PTCDs SHOULD BE CONSIDERED ON ALL WORKS AND ONLY BE SUPPLEMENTED WITH MANUAL TRAFFIC CONTROL UNDER AN AWTM/WTM RISK ASSESSMENT.	E	F	G	H	TABLES SIGN SPACING AGTMM PART 3 - TABLE 2.2	
	 ACCREDITED TRAFFIC CONTROLLER  MMS-ADV-10  PORTABLE TRAFFIC CONTROL DEVICE (PTCD)  PORTABOOM  MMS-ADV-10 MMS-ADV-82  MMS-ADV-10 R6-6  TEMPORARY TRAFFIC SIGNAL							DATE OF DRAWING 2025 JULY LOCAL GOVERNMENT AUTHORITY - ROAD AUTHORITY MAIN ROADS WA CHECKED BY TYLER HARTLEY ACCREDITATION RTM-0066 DESIGNED BY MICHAEL REED ACCREDITATION AWTM-23-II536-02 GENERIC TRAFFIC GUIDANCE SCHEME TRAFFIC HOLD SETUPS SIDE ROAD (LOW VOLUME/SPEED) AS POSTED SPEED ZONE DRAWING NO 0922-01531-TH-003	SCALE - POSTED SPEED ≤60KM/H WORKSITE SPEED AS POSTED SIGNATURE  SIGNATURE  REVISION 6
8	A	B	C	D					