


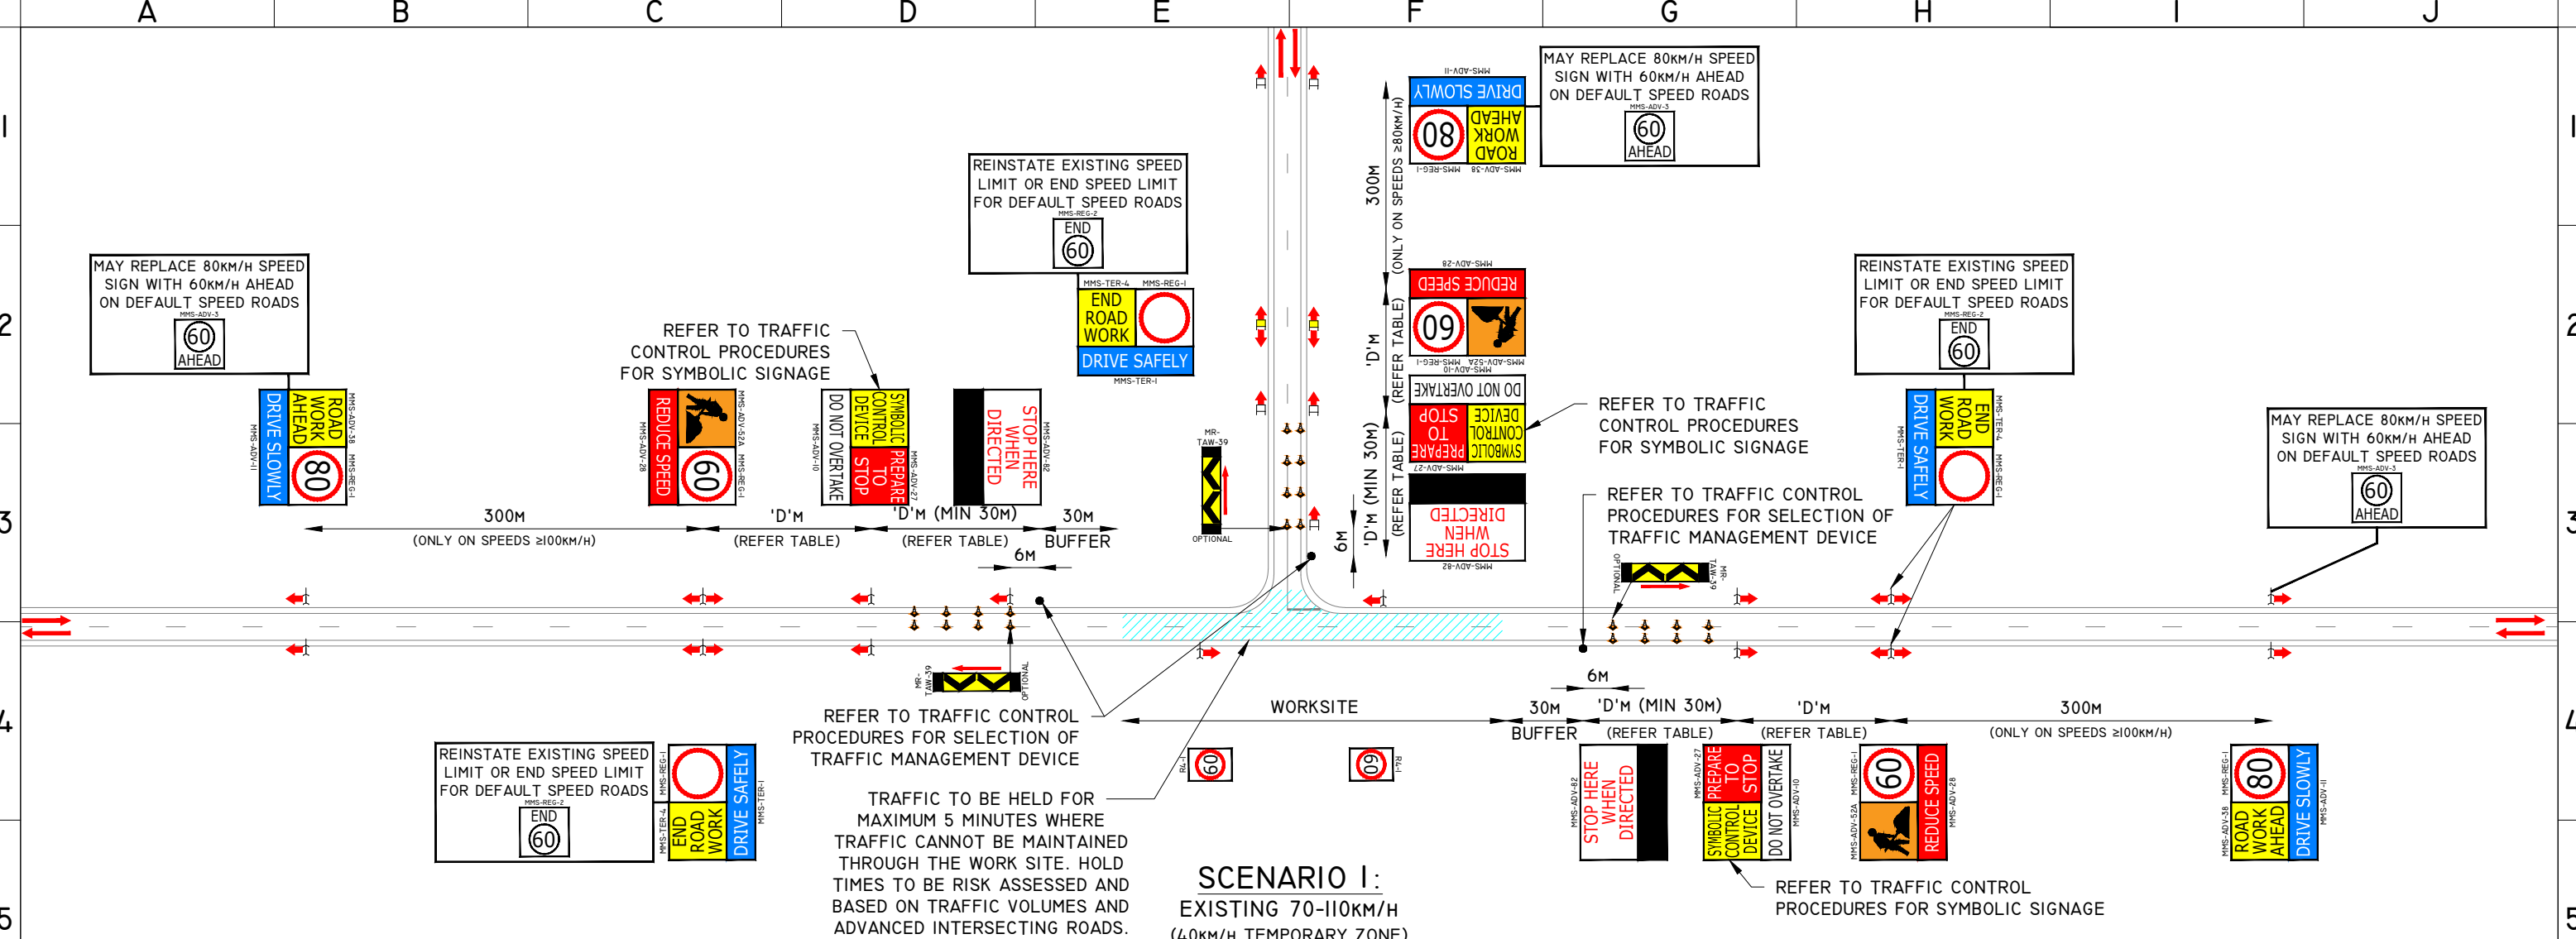

TRAFFIC CONTROL PROCEDURES				NOTES		SIGN SPACING	
REFER TO TMP SECTION 4.1.7 PORTABLE TRAFFIC CONTROL DEVICES FOR MORE DETAILS				TOLERANCES		AGTTM PART 3 - TABLE 2.2	
MANUAL TRAFFIC CONTROL				POSITION OF SIGNS: MINIMUM 10% LESS THAN THE DISTANCE OR LENGTHS GIVEN. MAXIMUM 25% MORE THAN THE DISTANCES OR LENGTHS GIVEN. SPACING OF DELINEATING DEVICES: MAXIMUM 10% MORE THAN THE SPACING GIVEN. NO MINIMUM.		SPEED LIMIT (KM/H)	DISTANCE ('D') (M)
PORTABLE TRAFFIC CONTROL DEVICE (PTCD)				AGTTM PART 6 SECTION 6.8.		55 OR LESS	15
				DOCUMENTATION		56 TO 65	45
				ON-SITE VARIATIONS MUST BE APPROVED BY THE TRAFFIC MANAGEMENT SUPERVISOR, THAN AN ON-SITE VARIATION MADE AND CHANGES RECORDED IN THE DAILY DAIRY. FOR MORE INFORMATION REFER TO SECTION 9.3 OF THE TMP.		GREATER THAN 65	EQUAL TO SPEED OF TRAFFIC IN KM/H
				1. A RISK ASSESSMENT MUST BE CARRIED OUT TO DETERMINE THE REQUIREMENTS OF AFTERCARE.			
				2. ALL SIGN LOCATIONS ARE TO BE CHECKED ON SITE PRIOR TO SETOUT AND POSITIONS ADJUSTED AS PER THE 'TOLERANCES'. FOR BOX EDGED SIGN ALTERNATIVES, CONSULT AWTM PRIOR TO IMPLEMENTATION.			
				3. ALL CONTRADICTORY SIGNS TO BE COVERED BY SUITABLY OPAQUE MATERIAL.			
				5. PEDESTRIAN MANAGEMENT			
				1. 'PEDESTRIAN WATCH YOUR STEP' SIGN TO BE INSTALLED ON EACH APPROACH WHERE WORKS MAY ENCROACH ONTO OR ADJACENT TO EXISTING FOOTPATH FACILITIES.			
				2. TM PERSONNEL TO MONITOR AND ESCORT PEDESTRIANS THROUGH THE WORK AREA AS REQUIRED.			
				3. PEDESTRIANS MAY BE HELD ON EITHER END OF THE WORKSITE UNTIL IT IS SAFE TO PASS AS REQUIRED.			
				RECOMMENDED CONE SPACING			
				CENTRELINE ON APPROACH TO TC POSITION: 4M			
				TAPER AT TRAFFIC CONTROL STATION: 4M			