



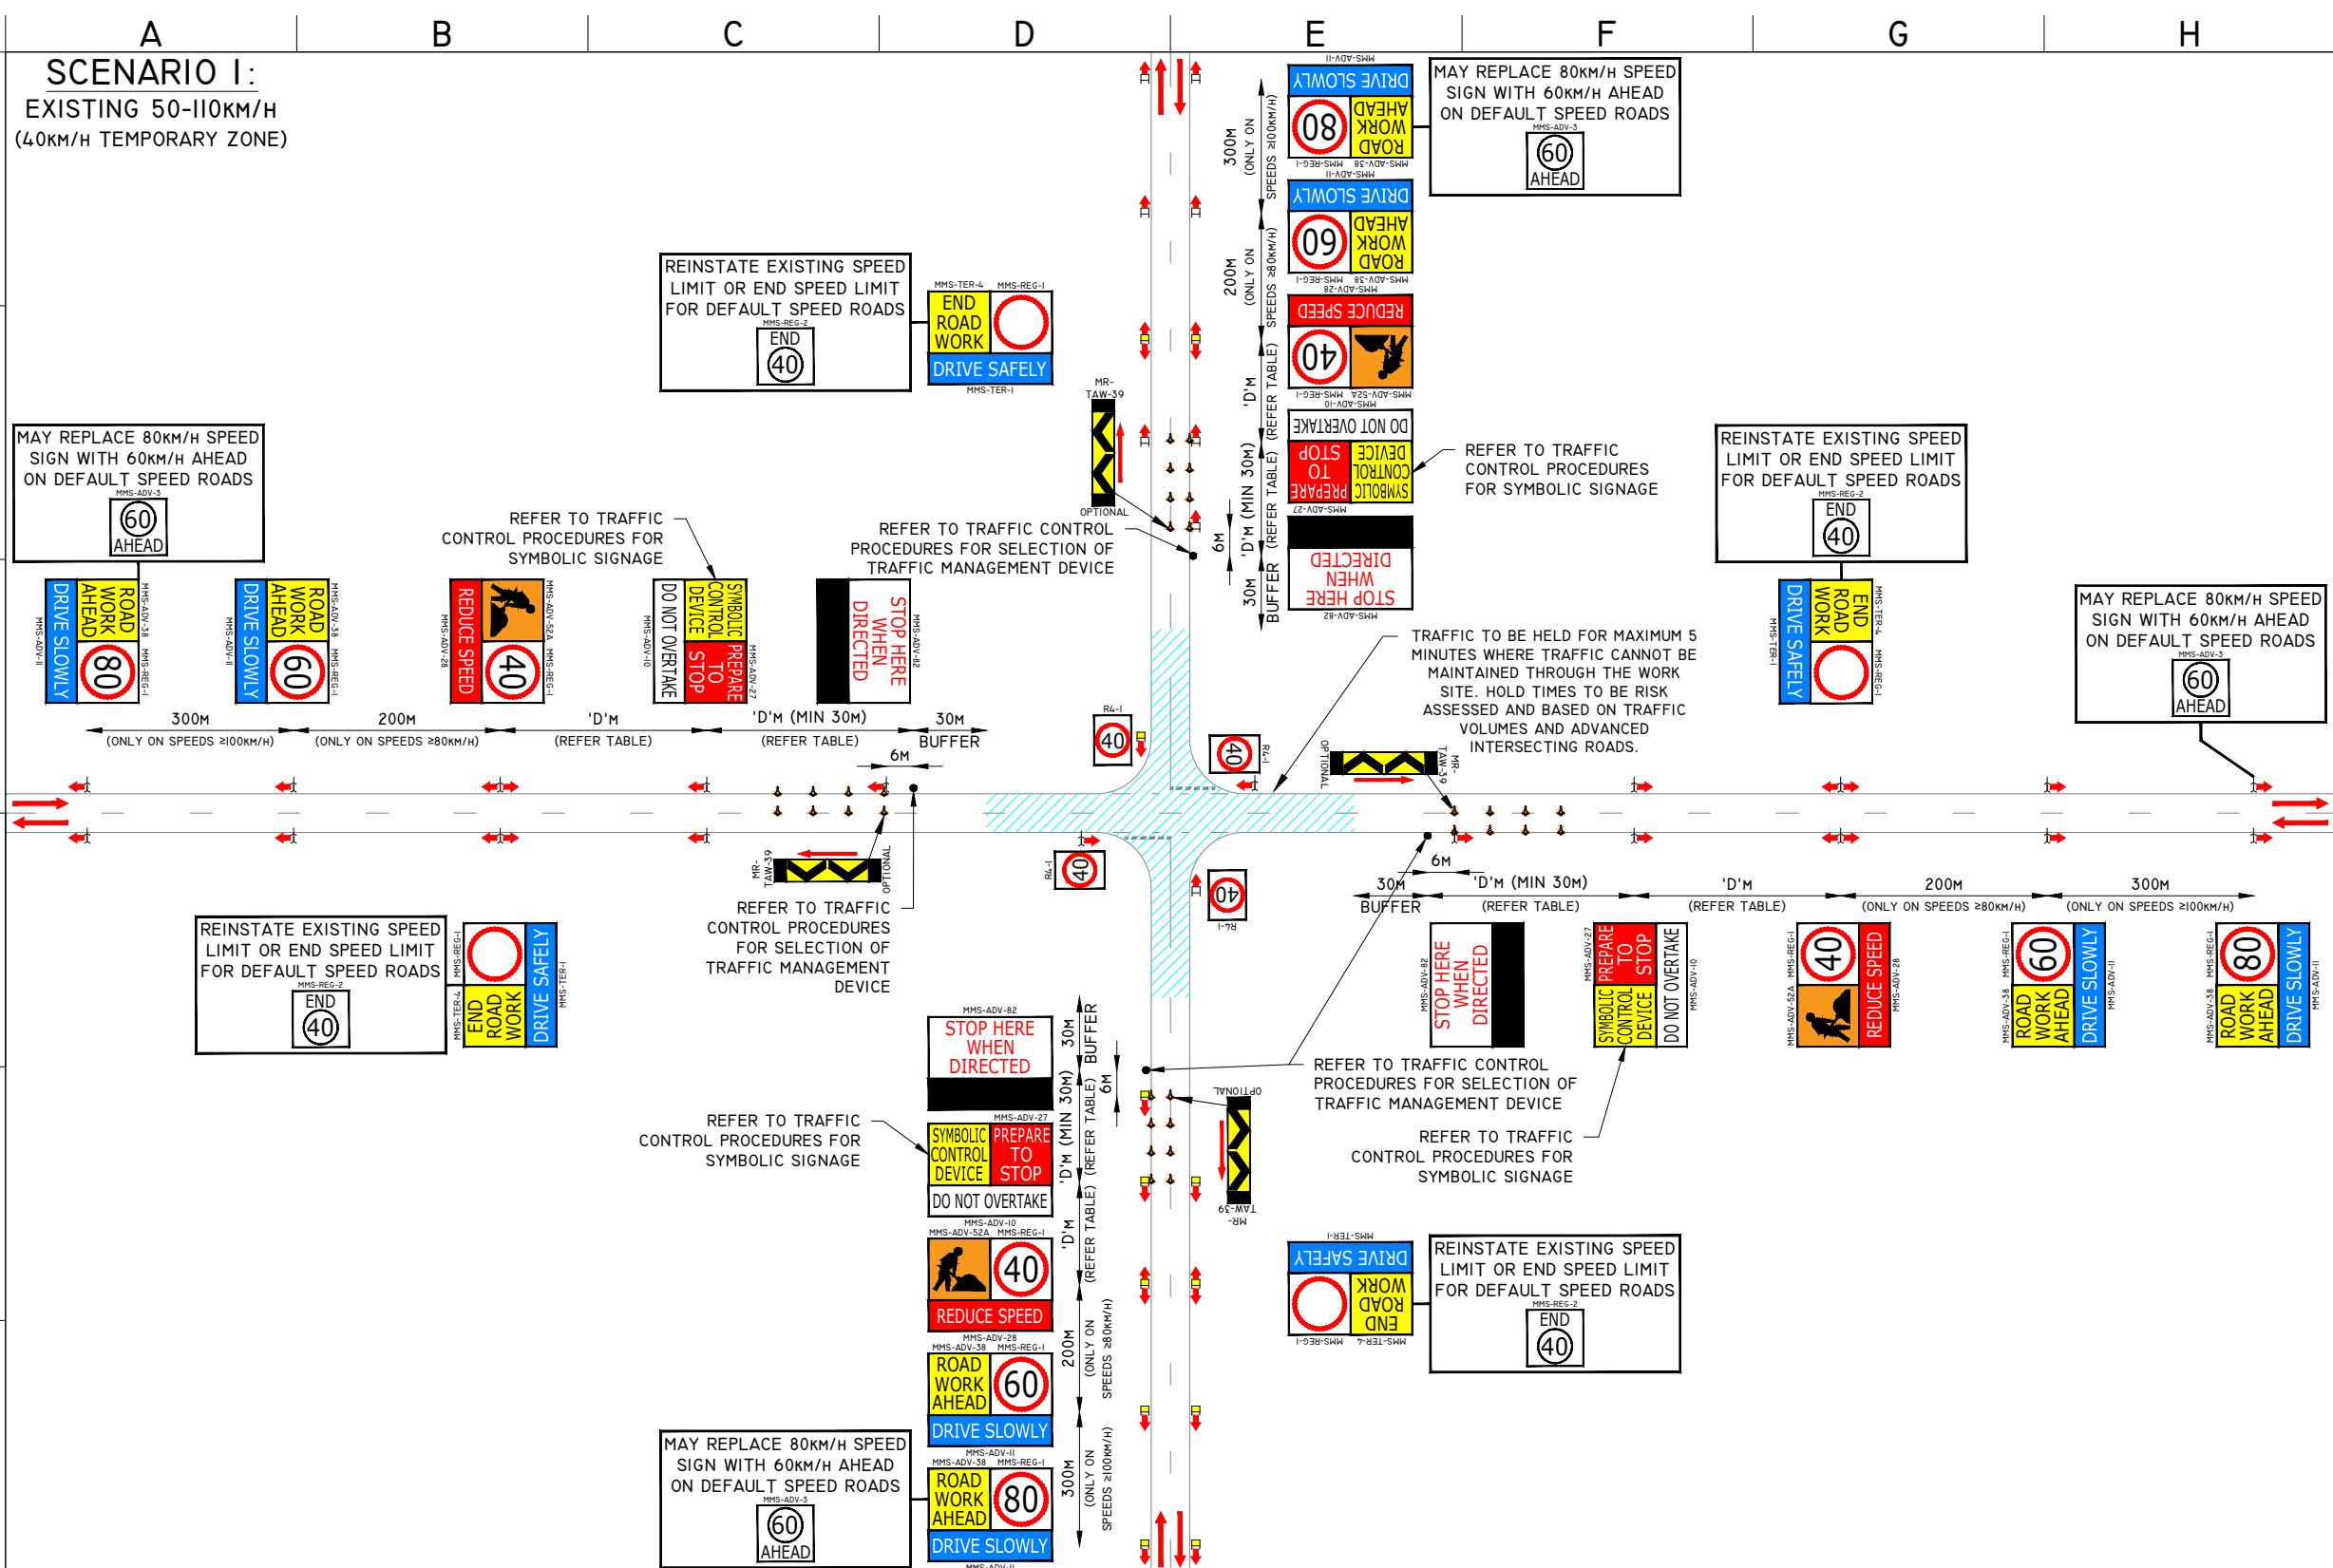

	NOTES TOLERANCES POSITION OF SIGNS: MINIMUM 10% LESS THAN THE DISTANCE OR LENGTHS GIVEN. MAXIMUM 25% MORE THAN THE DISTANCES OR LENGTHS GIVEN. SPACING OF DELINEATING DEVICES: MAXIMUM 10% MORE THAN THE SPACING GIVEN. NO MINIMUM. AGTTM PART 6 SECTION 6.8. DOCUMENTATION ON-SITE VARIATIONS MUST BE APPROVED BY THE TRAFFIC MANAGEMENT SUPERVISOR, THAN AN ON-SITE VARIATION MADE AND CHANGES RECORDED IN THE DAILY DAIRY. FOR MORE INFORMATION REFER TO SECTION 9.3 OF THE TMP. GENERAL NOTES 1. A RISK ASSESSMENT MUST BE CARRIED OUT TO DETERMINE THE REQUIREMENTS OF AFTERCARE. 2. ALL SIGN LOCATIONS ARE TO BE CHECKED ON SITE PRIOR TO SETOUT AND POSITIONS ADJUSTED AS PER THE 'TOLERANCES'. 3. ALL CONTRADICTIONARY SIGNS TO BE COVERED BY SUITABLY OPAQUE MATERIAL. 4. FOR BOX EDGED SIGN ALTERNATIVES, CONSULT AWTM PRIOR TO IMPLEMENTATION. 5. MAXIMUM LENGTH OF 40km/h TEMPORARY SPEED ZONE MUST BE 500M. PEDESTRIAN MANAGEMENT 1. 'PEDESTRIAN WATCH YOUR STEP' SIGN TO BE INSTALLED ON EACH APPROACH WHERE WORKS MAY ENCR OACH ONTO OR ADJACENT TO EXISTING FOOTPATH FACILITIES. 2. TM PERSONNEL TO MONITOR AND ESCORT PEDESTRIANS THROUGH THE WORK AREA AS REQUIRED. 3. PEDESTRIANS MAY BE HELD ON EITHER END OF THE WORKSITE UNTIL IT IS SAFE TO PASS AS REQUIRED. RECOMMENDED CONE SPACING CENTRELINE ON APPROACH TO TC POSITION: 4M TAPER AT TRAFFIC CONTROL STATION: 4M	1
		2
		3
		4
		5
	LEGEND EXISTING ROAD PROPOSED CONES WORKSITE	6
	TRAFFIC MANAGEMENT BRANCH WESTERN AUSTRALIA METROPOLITAN REGIONS TRAFFIC MANAGEMENT BRANCH WATERLOO CRESCENT EAST PERTH 6004	

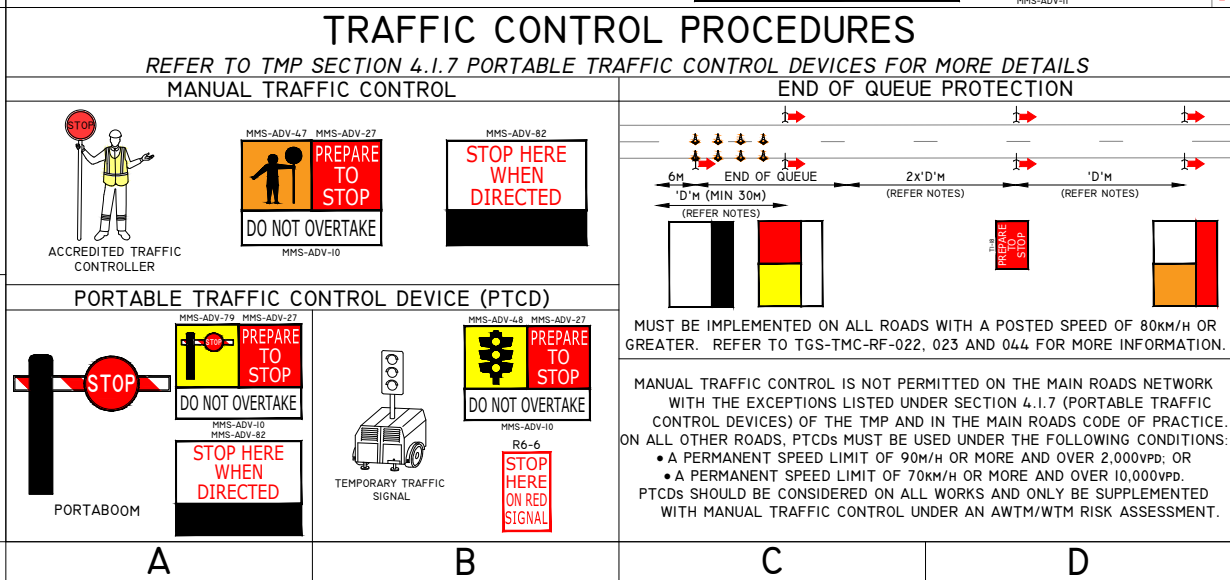

TABLES	
SIGN SPACING	
AGTMM PART 3 - TABLE 2.2	
SPEED LIMIT (KM/H)	DISTANCE ('D') (M)
55 OR LESS	15
56 TO 65	45
GREATER THAN 65	EQUAL TO SPEED OF TRAFFIC IN KM/H
E	F

WATERLOO CRESCENT TELEPHONE (08) 138 138		EAST PERTH 6004	
DATE OF DRAWING 2025 JULY		SCALE -	
LOCAL GOVERNMENT AUTHORITY -		POSTED SPEED 50-110KM/H	
ROAD AUTHORITY MAIN ROADS WA		WORKSITE SPEED 40KM/H	
CHECKED BY TYLER HARTLEY		SIGNATURE 	
ACCREDITATION RTM-0066			
DESIGNED BY MICHAEL REED		SIGNATURE 	
ACCREDITATION AWTM-23-11536-02			
GENERIC TRAFFIC GUIDANCE SCHEME TRAFFIC HOLD SETUPS 4-WAY INTERSECTION WORKSITE WITHIN 1.2M			8
DRAWING NO 0922-01531-TH-011		REVISION 6	