

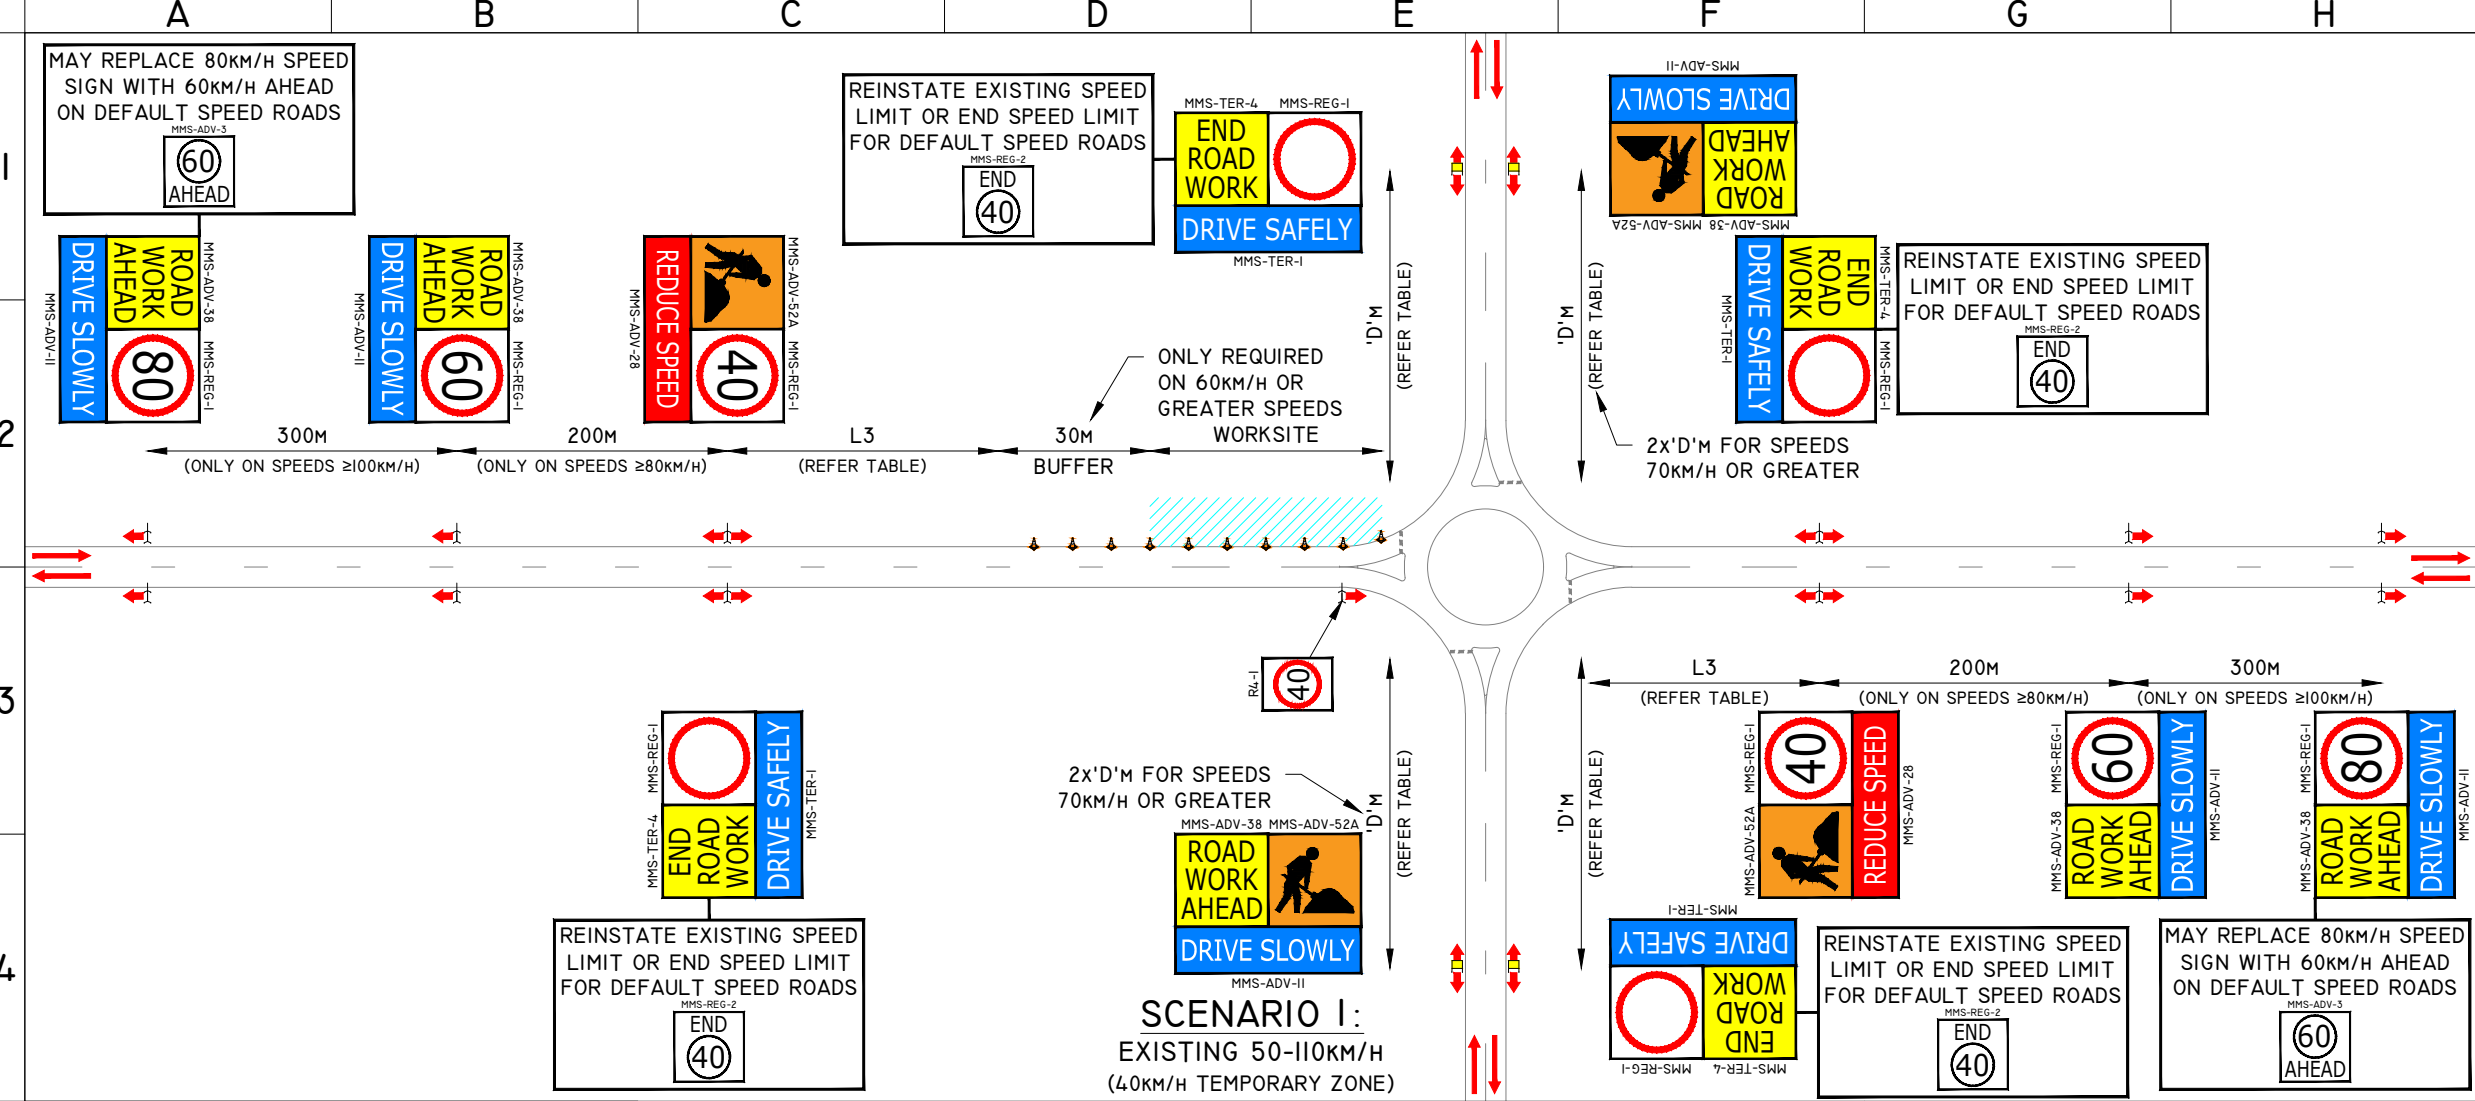


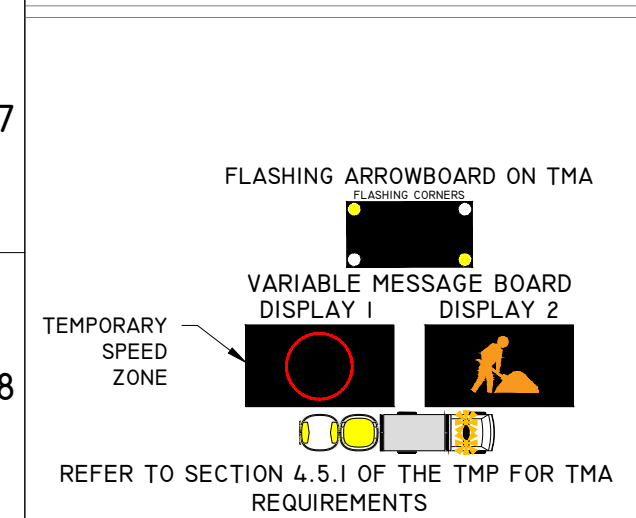

SHADOW VEHICLE INSET
(ONLY REQUIRED ON POSTED SPEEDS 80km/h OR GREATER)
SHADOW VEHICLE MAY BE DISPENSED WITH UNDER RISK ASSESSMENT UNDERTAKEN BY AN AWTM AS PART OF THE TM ADVICE OR A WTM ON SITE. IN THE ABSENCE OF SHADOW VEHICLE A LOOKOUT PERSON IS REQUIRED. REFER TO SECTION 4.5 OF THE TMP FOR MORE DETAILS.

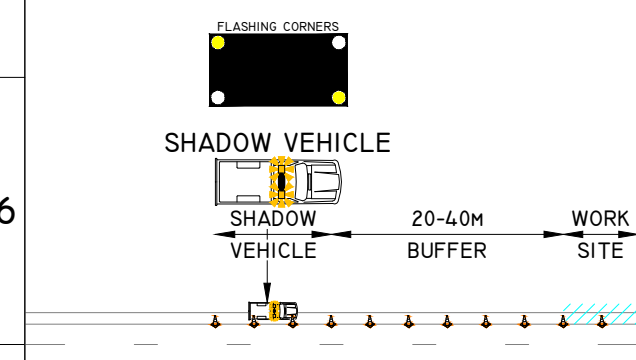

NOTES

TOLERANCES
POSITION OF SIGNS:
MINIMUM 10% LESS THAN THE DISTANCE OR LENGTHS GIVEN.
MAXIMUM 25% MORE THAN THE DISTANCES OR LENGTHS GIVEN.
SPACING OF DELINEATING DEVICES:
MAXIMUM 10% MORE THAN THE SPACING GIVEN.
NO MINIMUM.
AGTTM PART 6 SECTION 6.8.

DOCUMENTATION
IF REQUIRED, AN APPROVAL BY THE TRAFFIC MANAGEMENT SUPERVISOR MUST BE SOUGHT, THAN AN ON-SITE VARIATION MADE AND CHANGES RECORDED IN THE DAILY DAIRY. FOR MORE INFORMATION REFER TO SECTION 9.3 OF THE TMP.

- A RISK ASSESSMENT MUST BE CARRIED OUT TO DETERMINE THE REQUIREMENTS OF AFTERCARE.
- ALL SIGN LOCATIONS ARE TO BE CHECKED ON SITE PRIOR TO SETOUT AND POSITIONS ADJUSTED AS PER THE 'TOLERANCES'.
- FOR BOX EDGED SIGN ALTERNATIVES, CONSULT AWTM PRIOR TO IMPLEMENTATION.
- ALL CONTRADICTORY SIGNS WITHIN THE TM SETUP TO BE COVERED BY SUITABLY OPAQUE MATERIAL.
- MAXIMUM LENGTH OF 40km/h SPEED ZONE MUST BE 500m.
- SETUP IS INDICATIVE ONLY AND CAN BE MIRRORRED ON ALL APPROACHES TO THE ROUNDABOUT AS REQUIRED.

PEDESTRIAN MANAGEMENT

- 'PEDESTRIAN WATCH YOUR STEP' SIGN TO BE INSTALLED ON EACH APPROACH WHERE WORKS MAY ENCROACH ONTO OR ADJACENT TO EXISTING FOOTPATH FACILITIES.
- TM PERSONNEL TO MONITOR AND ESCORT PEDESTRIANS THROUGH THE WORK AREA AS REQUIRED.
- PEDESTRIANS MAY BE HELD ON EITHER END OF THE WORKSITE UNTIL IT IS SAFE TO PASS AS REQUIRED.

RECOMMENDED CONE SPACING
AGTTM PART 3 - TABLE 5.3
ALL PURPOSES:
(≤ 50km/h): 4M
PROTECTING FRESHLY PAINTED LINES:
(≤ 70km/h): 24M

1

2

3

4

5

TABLES	
SIGN SPACING	
AGTTM PART 3 - TABLE 2.2	
SPEED LIMIT (KM/H)	DISTANCE ('D')
55 OR LESS	15
56 TO 65	45
GREATER THAN 65	EQUAL TO SPEED OF TRAFFIC IN KM/H
MAIN ROADS WA CoP SECTION 6.5.2 - TABLE 6	
SPEED LIMIT (KM/H)	L3 (M)
60 OR LESS	45
70	70
80 OR GREATER	90

LEGEND

EXISTING ROAD

PROPOSED CONES

WORKSITE

mainroads
WESTERN AUSTRALIA

METROPOLITAN REGIONS
TRAFFIC MANAGEMENT BRANCH
WATERLOO CRESCENT EAST PERTH 6004
TELEPHONE (08) 138 138

DATE OF DRAWING 2025 JULY	SCALE -
LOCAL GOVERNMENT AUTHORITY -	POSTED SPEED 50-110km/h
ROAD AUTHORITY MAIN ROADS WA	WORKSITE SPEED 40km/h
CHECKED BY TYLER HARTLEY	SIGNATURE <i>Tyler Hartley</i>
ACCREDITATION RTM-0066	SIGNATURE <i>Michael Reed</i>
DRAWN BY MICHAEL REED	
ACCREDITATION AWTM-23-11536-02	
GENERIC TRAFFIC GUIDANCE SCHEME WORKS OFF ROAD SETUPS ON ROUNDABOUT APPROACH WORKSITE WITHIN 1.2M	
DRAWING NO 0922-01531-WR-007	REVISION 6

6

7

8